ETABS

SCHEMATIC DESIGN DRAWINGS

THESE DRAWINGS HAVE BEEN AUTOMATICALLY GENERATED FROM INFORMATION THAT IS BASED ONLY ON CALCULATED STRENGTH REQUIREMENTS. THE DRAWING SHEETS ARE A REPRESENTATION OF THE DESIGN OUTPUT IN A SCHEMATIC FORM AND ARE NOT FOR CONSTRUCTION. ALL DETAILS SHOULD BE REVIEWED FOR COMPLIANCE WITH LOCAL DETAILING CODES AND OTHER REQUIREMENTS.

THE INFORMATION ON THESE DRAWINGS MUST BE CHECKED BY A QUALIFIED AND EXPERIENCED ENGINEER. THE ENGINEER MUST INDEPENDENTLY VERIFY THE RESULTS AND TAKE PROFESSIONAL RESPONSIBILITY FOR THE FINAL INFORMATION THAT IS PRESENTED.

CONSIDERABLE TIME, EFFORT AND EXPENSE HAVE GONE INTO THE DEVELOPMENT AND TESTING OF THIS SOFTWARE. HOWEVER, THE USER ACCEPTS AND UNDERSTANDS THAT NO WARRANTY IS EXPRESSED OR IMPLIED BY THE DEVELOPERS OR THE DISTRIBUTORS ON THE ACCURACY OR THE RELIABILITY OF THIS PRODUCT.

List of Drawings

Sheet N	Sheet Title	Rev. No	Remarks
S-00	Cover Sheet		
S-01	List of Drawings		
S-02	BG-1 Layout Plan		
S-03	BG-1 Rebar Table		
S-04	BG-2 Layout Plan		
S-05	BG-2 Rebar Table		
S-06	BG-3 Layout Plan		
S-07	BG-3 Rebar Table		
S-08	BG-4 Layout Plan		
S-09	BG-4 Rebar Table		
S-10	SG-PR RC Beam Typical Plan		
S-11	SG-PR RC Beam Rebar Table		
S-12	CSG-01 Layout Plan		
S-13	RC Column Layout		
S-14	RC Column Elevation Summary		
S-15	WS-1:Section-Story1		
S-16	WS-1:Section-Story3		
S-17	WS-1:Section-Story5		
S-18	WS-1:E-2		
S-19	WS-1:E-2 (No Bars)		
S-20	WS-2:Base Plan		
S-21	WS-2:Section-Story2		
S-22	WS-2:Section-Story4		
S-23	WS-2:E-1		
S-24	WS-2:E-1 (No Bars)		
S-25	WS-3:Base Plan		
S-26	WS-3:Section-Story2		
S-27	WS-3:Section-Story4		
S-28	WS-3:E-1		
S-29	WS-3:E-1 (No Bars)		
S-30	WS-4:Base Plan		
S-31	WS-4:Section-Story2		
S-32	WS-4:Section-Story4		
S-33	WS-4:E-1		
S-34	WS-4:E-1 (No Bars)		
S-35	Layout Plan		
S-36	CB-1:Elevation (No bars)		
S-37	CB-1:Rebar Profiles		
S-38	CB-1:Beam Table		
S-39	CB-2:Elevation (No bars)		
S-40	CB-2:Elevation		
S-41	CB-2:Rebar Profiles		
S-42	CB-2:BOQ		
S-43	CB-3:Elevation-All Bars		
S-44	CB-3:Beam Table		
S-45	CB-4:Elevation (No bars)		
S-46	CB-4:Elevation		
S-47	CB-4:Rebar Profiles		
S-48	CB-4:Beam Table		
S-49	CB-5:Elevation (No bars)		
S-50	CB-5:Elevation		
S-51	CB-5:Rebar Profiles		
S-52	CB-5:Beam Table		
S-53	CB-6:Elevation		
S-54	CB-6:Section-1		
S-55	CB-7:Elevation (No bars)		
S-56	CB-7:Rebar Profiles		
S-57	CB-7:BOQ		
S-58	CB-8:Elevation		
S-59	CB-8:Rebar Profiles		
S-60	CB-8:BOQ		
S-61	CB-9:Elevation-All Bars		
S-62	CB-9:Section-1		
S-63	CB-9:Rebar Weights		
S-64	CS-11: Section-2		
S-65	WS-1:Section-Story2		
S-66	WS-1:Section-Story4		
S-67	WS-1:E-1		
S-68	WS-1:E-1 (No Bars)		

www.csiamerica.com


No	Description	Date

List of Drawings

Project Number	
Date	
Drawn By	
Checked By	

S-01

Scale

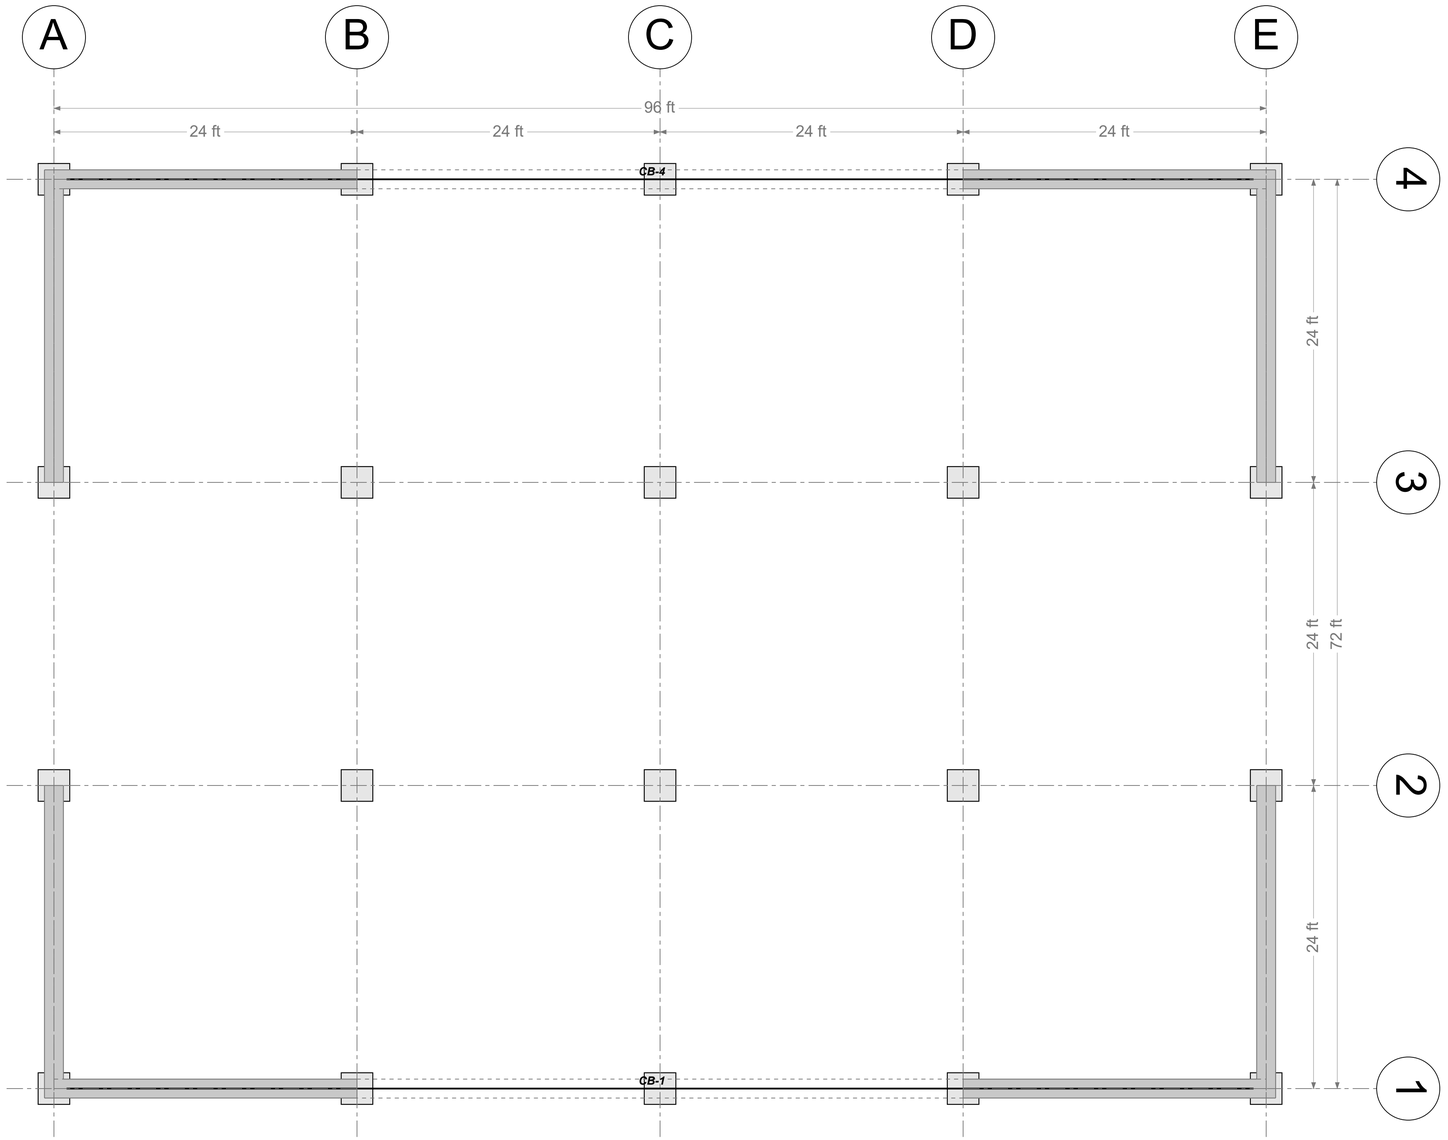

BG-1 Layout Plan
(Scale = 1"=6'-0")

www.csiamerica.com

No	Description	Date

BG-1 Layout Plan

Project Number	
Date	
Drawn By	
Checked By	

S-02

Scale

Story4:BG-1 - Rebar Table

Beam Label	Span/Support	Width	Depth	Bar A	Bar B	Bar C	Bar D	Bar E	Bar F	Bar G	Zone A	Zone B	Zone C	Zone D	Zone E	Elevation Type
CB-1	Support-1	-	-	2-#6A	2-#6B	-	-	-	-	-	-	-	-	-	-	Elevation 1
-	Span-1	18	30	-	-	-	-	-	-	-	#4@4.5	#4@14	#4@15	#4@14	#4@4.5	-
-	Support-2	-	-	-	-	2-#6C	2-#6D	-	-	-	-	-	-	-	-	-
-	Span-2	18	30	-	-	-	-	-	-	-	#4@4.5	#4@14	#4@15	#4@14.5	#4@4.5	-
-	Support-3	-	-	-	-	2-#6C	2-#6D	-	-	-	-	-	-	-	-	-
-	Span-3	18	30	-	-	-	-	-	-	-	#4@4.5	#4@14.5	#4@15	#4@14	#4@4.5	-
-	Support-4	-	-	-	-	2-#6C	2-#6D	-	-	-	-	-	-	-	-	-
-	Span-4	18	30	-	-	-	-	-	-	-	#4@4.5	-	#4@14	-	#4@4.5	-
-	Support-5	-	-	-	-	2-#6C	2-#6D	-	-	-	-	-	-	-	-	-
-	Span-5	18	30	-	-	-	-	-	-	-	#4@4.5	-	#4@14	-	#4@4.5	-
-	Support-6	-	-	2-#6A	2-#6B	-	-	-	-	-	-	-	-	-	-	-
CB-4	Support-1	-	-	2-#6A	2-#6B	-	-	-	-	-	-	-	-	-	-	Elevation 1
-	Span-1	18	30	-	-	-	-	-	-	-	#4@4.5	#4@14	#4@15	#4@14	#4@4.5	-
-	Support-2	-	-	-	-	2-#6C	2-#6D	-	-	-	-	-	-	-	-	-
-	Span-2	18	30	-	-	-	-	-	-	-	#4@4.5	#4@14	#4@15	#4@14.5	#4@4.5	-
-	Support-3	-	-	-	-	2-#6C	2-#6D	-	-	-	-	-	-	-	-	-
-	Span-3	18	30	-	-	-	-	-	-	-	#4@4.5	#4@14.5	#4@15	#4@14	#4@4.5	-
-	Support-4	-	-	-	-	2-#6C	2-#6D	-	-	-	-	-	-	-	-	-
-	Span-4	18	30	-	-	-	-	-	-	-	#4@4.5	-	#4@14	-	#4@4.5	-
-	Support-5	-	-	-	-	2-#6C	2-#6D	-	-	-	-	-	-	-	-	-
-	Span-5	18	30	-	-	-	-	-	-	-	#4@4.5	-	#4@14	-	#4@4.5	-
-	Support-6	-	-	2-#6A	2-#6B	-	-	-	-	-	-	-	-	-	-	-

Story4:BG-1-BOQ Summary

Sr. No.	Item	Quantity	Unit
1	Longitudinal Bars	1.43	ton
2	Ties and Stirrups	0.95	ton
3	Total Rebars	2.38	ton
4	Total Beam Length	192	ft
5	Total Beam Volume	720	cu ft
6	Weight/Volume	6.62	lb/cu ft
Note	Does not include weight of Typical Bars		

Story4:BG-1-Rebar Weight Summary

Sr. No.	Size	Area (in²)	Length (ft)	Weight (ton)
1	#4	0.2	2,795.04	0.95
2	#6	0.44	1,914.04	1.43
Note	Does not include Typical Bars			

www.csiamerica.com


No	Description	Date

BG-1 Rebar Table

Project Number	
Date	
Drawn By	
Checked By	

S-03

Scale

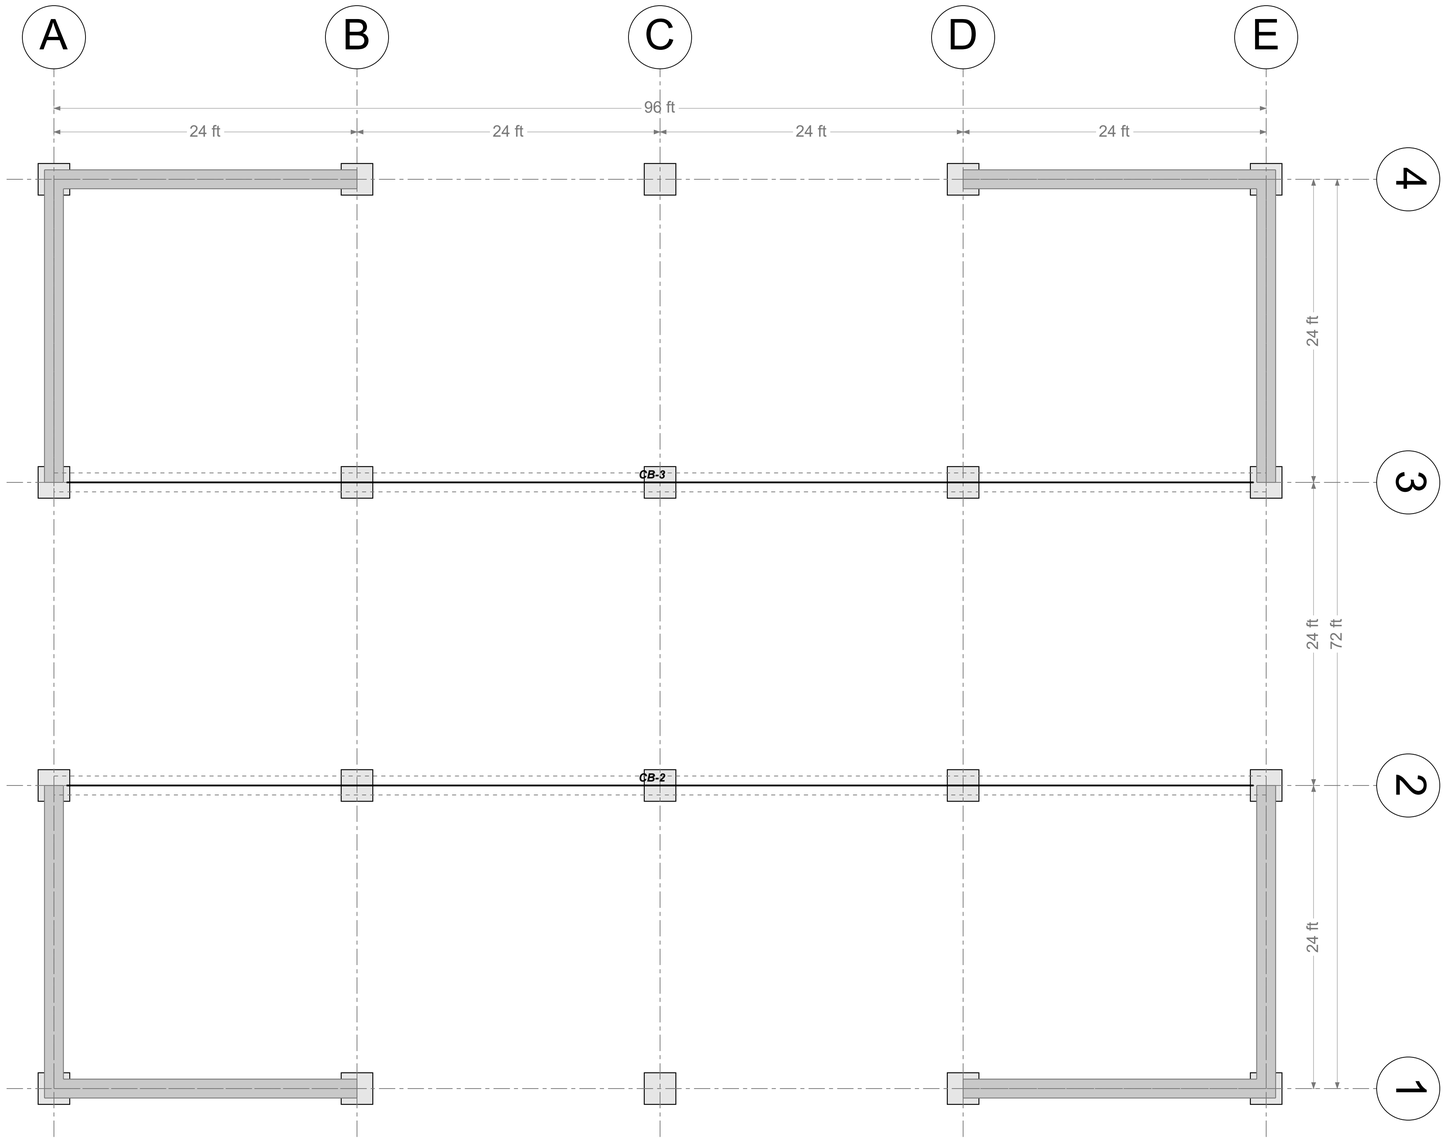

BG-2 Layout Plan
(Scale = 1"=6'-0")

www.csiamerica.com

No	Description	Date

BG-2 Layout Plan

Project Number	
Date	
Drawn By	
Checked By	

S-04

Scale

Story4:BG-2 - Rebar Table

Beam Label	Span/Support	Width	Depth	Bar A	Bar B	Bar C	Bar D	Bar E	Bar F	Bar G	Zone A	Zone B	Zone C	Zone D	Zone E	Elevation Type
CB-2	Support-1	-	-	2-#6A	2-#6B	-	-	-	-	-	-	-	-	-	-	Elevation 1
-	Span-1	18	30	-	-	-	-	-	-	-	#4@4.5	#4@12.5	#4@15	#4@13	#4@4.5	-
-	Support-2	-	-	-	-	2-#6C	2-#6D	-	-	-	-	-	-	-	-	-
-	Span-2	18	30	-	-	-	-	-	-	-	#4@4.5	#4@12.5	#4@15	#4@12.5	#4@4.5	-
-	Support-3	-	-	-	-	2-#6C	2-#6D	-	-	-	-	-	-	-	-	-
-	Span-3	18	30	-	-	-	-	-	-	-	#4@4.5	#4@12.5	#4@15	#4@12.5	#4@4.5	-
-	Support-4	-	-	-	-	2-#6C	2-#6D	-	-	-	-	-	-	-	-	-
-	Span-4	18	30	-	-	-	-	-	-	-	#4@4.5	#4@13	#4@15	#4@12.5	#4@4.5	-
-	Support-5	-	-	2-#6A	2-#6B	-	-	-	-	-	-	-	-	-	-	-
CB-3	Support-1	-	-	2-#6A	2-#6B	-	-	-	-	-	-	-	-	-	-	Elevation 1
-	Span-1	18	30	-	-	-	-	-	-	-	#4@4.5	#4@12.5	#4@15	#4@13	#4@4.5	-
-	Support-2	-	-	-	-	2-#6C	2-#6D	-	-	-	-	-	-	-	-	-
-	Span-2	18	30	-	-	-	-	-	-	-	#4@4.5	#4@12.5	#4@15	#4@12.5	#4@4.5	-
-	Support-3	-	-	-	-	2-#6C	2-#6D	-	-	-	-	-	-	-	-	-
-	Span-3	18	30	-	-	-	-	-	-	-	#4@4.5	#4@12.5	#4@15	#4@12.5	#4@4.5	-
-	Support-4	-	-	-	-	2-#6C	2-#6D	-	-	-	-	-	-	-	-	-
-	Span-4	18	30	-	-	-	-	-	-	-	#4@4.5	#4@13	#4@15	#4@12.5	#4@4.5	-
-	Support-5	-	-	2-#6A	2-#6B	-	-	-	-	-	-	-	-	-	-	-

Story4:BG-2-Rebar Weight Summary

Sr. No.	Size	Area (in²)	Length (ft)	Weight (ton)
1	#4	0.2	2,175.6	0.74
2	#6	0.44	1,840.92	1.38
Note	Does not include Typical Bars			

Story4:BG-2-BOQ Summary

Sr. No.	Item	Quantity	Unit
1	Longitudinal Bars	1.38	ton
2	Ties and Stirrups	0.74	ton
3	Total Rebars	2.12	ton
4	Total Beam Length	192	ft
5	Total Beam Volume	720	cu ft
6	Weight/Volume	5.88	lb/cu ft
Note	Does not include weight of Typical Bars		

www.csiamerica.com


No	Description	Date

BG-2 Rebar Table

Project Number	
Date	
Drawn By	
Checked By	

S-05

Scale	

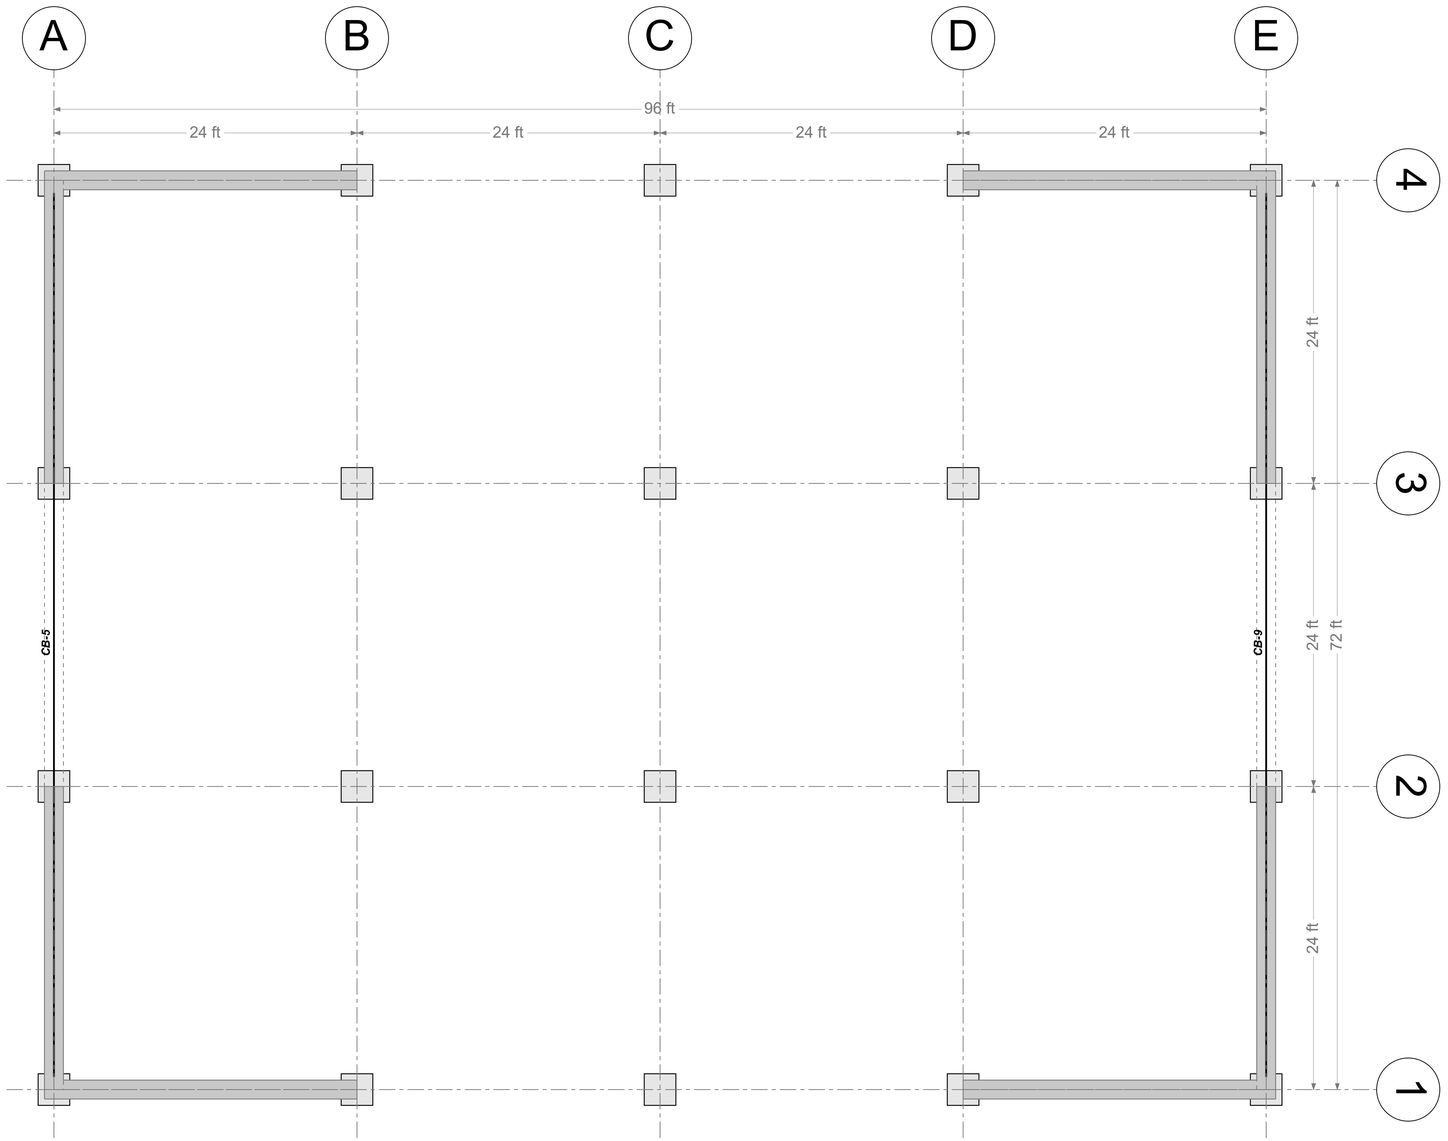

BG-3 Layout Plan
(Scale = 1"=6'-0")

www.csiamerica.com

No	Description	Date

BG-3 Layout Plan

Project Number	
Date	
Drawn By	
Checked By	

S-06

Scale

Story4:BG-3 - Rebar Table

Beam Label	Span/Support	Width	Depth	Bar A	Bar B	Bar C	Bar D	Bar E	Bar F	Bar G	Zone A	Zone B	Zone C	Zone D	Zone E	Elevation Type
CB-5	Support-1	-	-	2-#6A	2-#6B	-	-	-	-	-	-	-	-	-	-	Elevation 1
-	Span-1	18	30	-	-	-	-	-	-	-	#4@4.5	#4@14	#4@15	#4@14	#4@4.5	-
-	Support-2	-	-	-	-	2-#6C	2-#6D	-	-	-	-	-	-	-	-	-
-	Span-2	18	30	-	-	-	-	-	-	-	#4@4.5	#4@14	#4@15	#4@14	#4@4.5	-
-	Support-3	-	-	-	-	2-#6C	2-#6D	-	-	-	-	-	-	-	-	-
-	Span-3	18	30	-	-	-	-	-	-	-	#4@4.5	-	#4@14	-	#4@4.5	-
-	Support-4	-	-	-	-	2-#6C	2-#6D	-	-	-	-	-	-	-	-	-
-	Span-4	18	30	-	-	-	-	-	-	-	#4@4.5	-	#4@14	-	#4@4.5	-
-	Support-5	-	-	2-#6A	2-#6B	-	-	-	-	-	-	-	-	-	-	-
CB-9	Support-1	-	-	2-#6A	2-#6B	-	-	-	-	-	-	-	-	-	-	Elevation 1
-	Span-1	18	30	-	-	-	-	-	-	-	#4@4.5	#4@14	#4@15	#4@14	#4@4.5	-
-	Support-2	-	-	-	-	2-#6C	2-#6D	-	-	-	-	-	-	-	-	-
-	Span-2	18	30	-	-	-	-	-	-	-	#4@4.5	#4@14	#4@15	#4@14	#4@4.5	-
-	Support-3	-	-	-	-	2-#6C	2-#6D	-	-	-	-	-	-	-	-	-
-	Span-3	18	30	-	-	-	-	-	-	-	#4@4.5	-	#4@14	-	#4@4.5	-
-	Support-4	-	-	-	-	2-#6C	2-#6D	-	-	-	-	-	-	-	-	-
-	Span-4	18	30	-	-	-	-	-	-	-	#4@4.5	-	#4@14	-	#4@4.5	-
-	Support-5	-	-	2-#6A	2-#6B	-	-	-	-	-	-	-	-	-	-	-

Story4:BG-3-Rebar Weight Summary

Sr. No.	Size	Area (in²)	Length (ft)	Weight (ton)
1	#4	0.2	2,130.27	0.72
2	#6	0.44	1,460.77	1.09
Note	Does not include Typical Bars			

Story4:BG-3-BOQ Summary

Sr. No.	Item	Quantity	Unit
1	Longitudinal Bars	1.09	ton
2	Ties and Stirrups	0.72	ton
3	Total Rebars	1.82	ton
4	Total Beam Length	144	ft
5	Total Beam Volume	540	cu ft
6	Weight/Volume	6.73	lb/cu ft
Note	Does not include weight of Typical Bars		

www.csiamerica.com


No	Description	Date

BG-3 Rebar Table

Project Number	
Date	
Drawn By	
Checked By	

S-07

Scale	

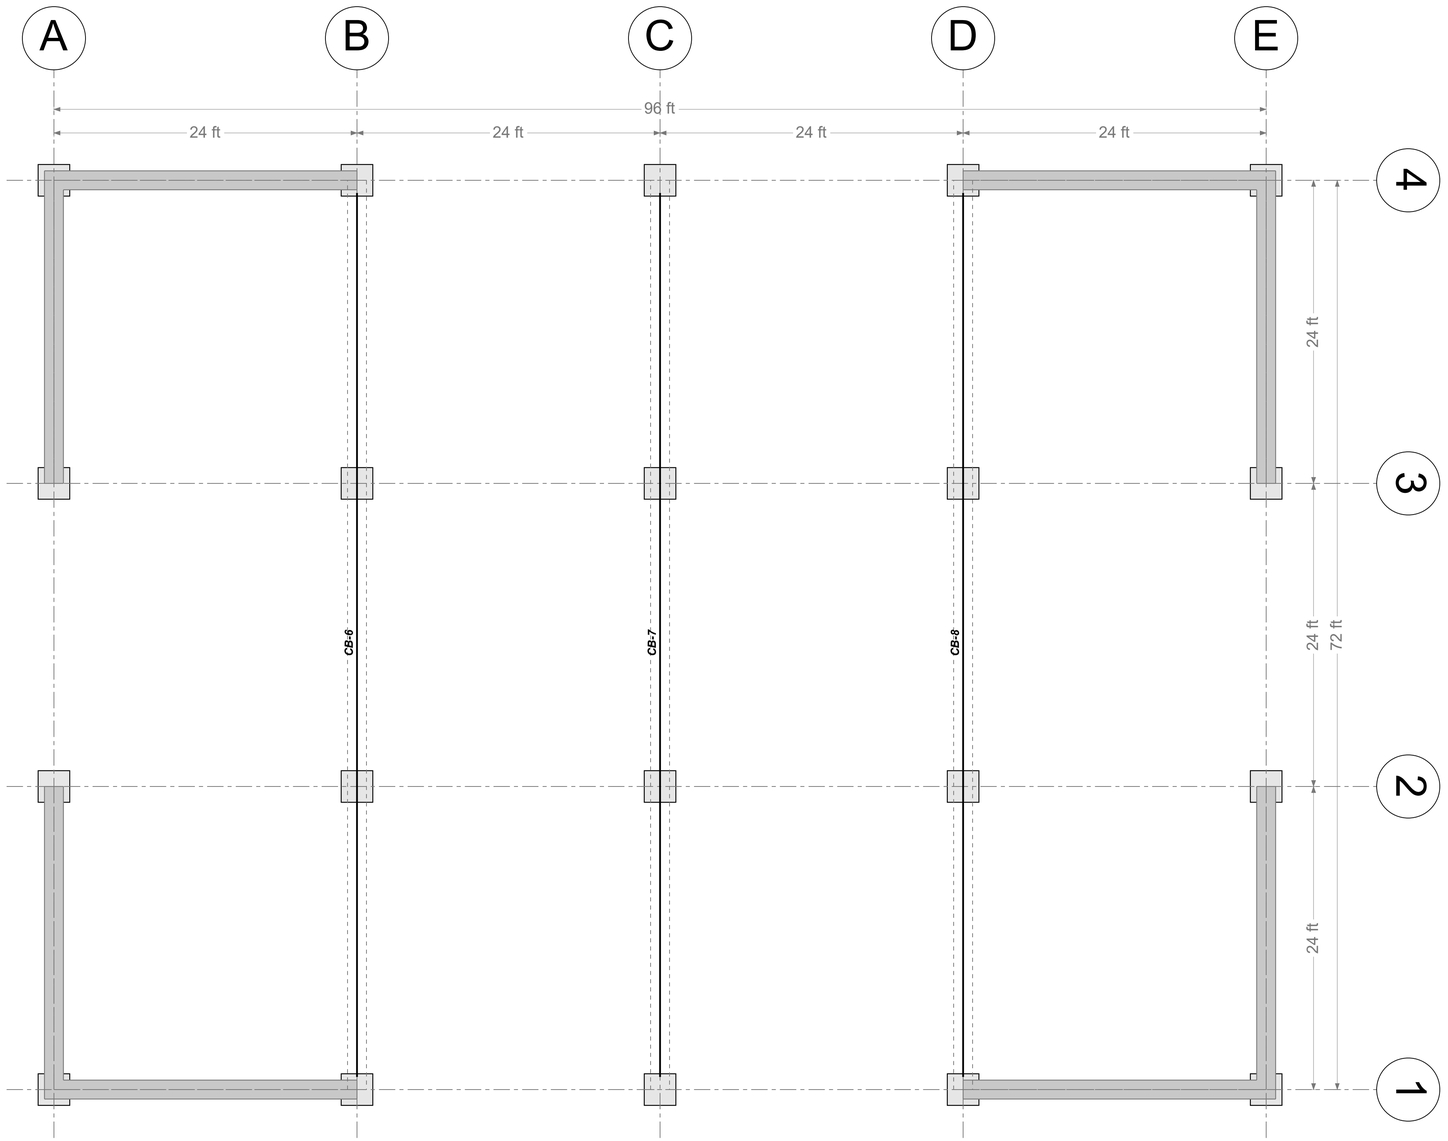

BG-4 Layout Plan
(Scale = 1"=6'-0")

www.csiamerica.com

No	Description	Date

BG-4 Layout Plan

Project Number	
Date	
Drawn By	
Checked By	

S-08

Scale

Story4:BG-4 - Rebar Table

Beam Label	Span/Support	Width	Depth	Bar A	Bar B	Bar C	Bar D	Bar E	Bar F	Bar G	Zone A	Zone B	Zone C	Zone D	Zone E	Elevation Type
CB-6	Support-1	-	-	2-#6A	2-#6B	-	-	-	-	-	-	-	-	-	-	Elevation 1
-	Span-1	18	30	-	-	-	-	-	-	-	#4@4.5	#4@12.5	#4@15	#4@13	#4@4.5	-
-	Support-2	-	-	-	-	2-#6C	2-#6D	-	-	-	-	-	-	-	-	-
-	Span-2	18	30	-	-	-	-	-	-	-	#4@4.5	#4@12.5	#4@15	#4@12.5	#4@4.5	-
-	Support-3	-	-	-	-	2-#6C	2-#6D	-	-	-	-	-	-	-	-	-
-	Span-3	18	30	-	-	-	-	-	-	-	#4@4.5	#4@13	#4@15	#4@12.5	#4@4.5	-
-	Support-4	-	-	2-#6A	2-#6B	-	-	-	-	-	-	-	-	-	-	-
CB-7	Support-1	-	-	2-#6A	2-#6B	-	-	-	-	-	-	-	-	-	-	Elevation 1
-	Span-1	18	30	-	-	-	-	-	-	-	#4@4.5	#4@12.5	#4@15	#4@13	#4@4.5	-
-	Support-2	-	-	-	-	2-#6C	2-#6D	-	-	-	-	-	-	-	-	-
-	Span-2	18	30	-	-	-	-	-	-	-	#4@4.5	#4@12.5	#4@15	#4@12.5	#4@4.5	-
-	Support-3	-	-	-	-	2-#6C	2-#6D	-	-	-	-	-	-	-	-	-
-	Span-3	18	30	-	-	-	-	-	-	-	#4@4.5	#4@13	#4@15	#4@12.5	#4@4.5	-
-	Support-4	-	-	2-#6A	2-#6B	-	-	-	-	-	-	-	-	-	-	-
CB-8	Support-1	-	-	2-#6A	2-#6B	-	-	-	-	-	-	-	-	-	-	Elevation 1
-	Span-1	18	30	-	-	-	-	-	-	-	#4@4.5	#4@12.5	#4@15	#4@13	#4@4.5	-
-	Support-2	-	-	-	-	2-#6C	2-#6D	-	-	-	-	-	-	-	-	-
-	Span-2	18	30	-	-	-	-	-	-	-	#4@4.5	#4@12.5	#4@15	#4@12.5	#4@4.5	-
-	Support-3	-	-	-	-	2-#6C	2-#6D	-	-	-	-	-	-	-	-	-
-	Span-3	18	30	-	-	-	-	-	-	-	#4@4.5	#4@13	#4@15	#4@12.5	#4@4.5	-
-	Support-4	-	-	2-#6A	2-#6B	-	-	-	-	-	-	-	-	-	-	-

Story4:BG-4-BOQ Summary

Sr. No.	Item	Quantity	Unit
1	Longitudinal Bars	1.56	ton
2	Ties and Stirrups	0.83	ton
3	Total Rebars	2.39	ton
4	Total Beam Length	216	ft
5	Total Beam Volume	810	cu ft
6	Weight/Volume	5.9	lb/cu ft
Note	Does not include weight of Typical Bars		

Story4:BG-4-Rebar Weight Summary

Sr. No.	Size	Area (in²)	Length (ft)	Weight (ton)
1	#4	0.2	2,447.55	0.83
2	#6	0.44	2,081.48	1.56
Note	Does not include Typical Bars			

www.csiamerica.com


No	Description	Date

BG-4 Rebar Table

Project Number	
Date	
Drawn By	
Checked By	

S-09

Scale

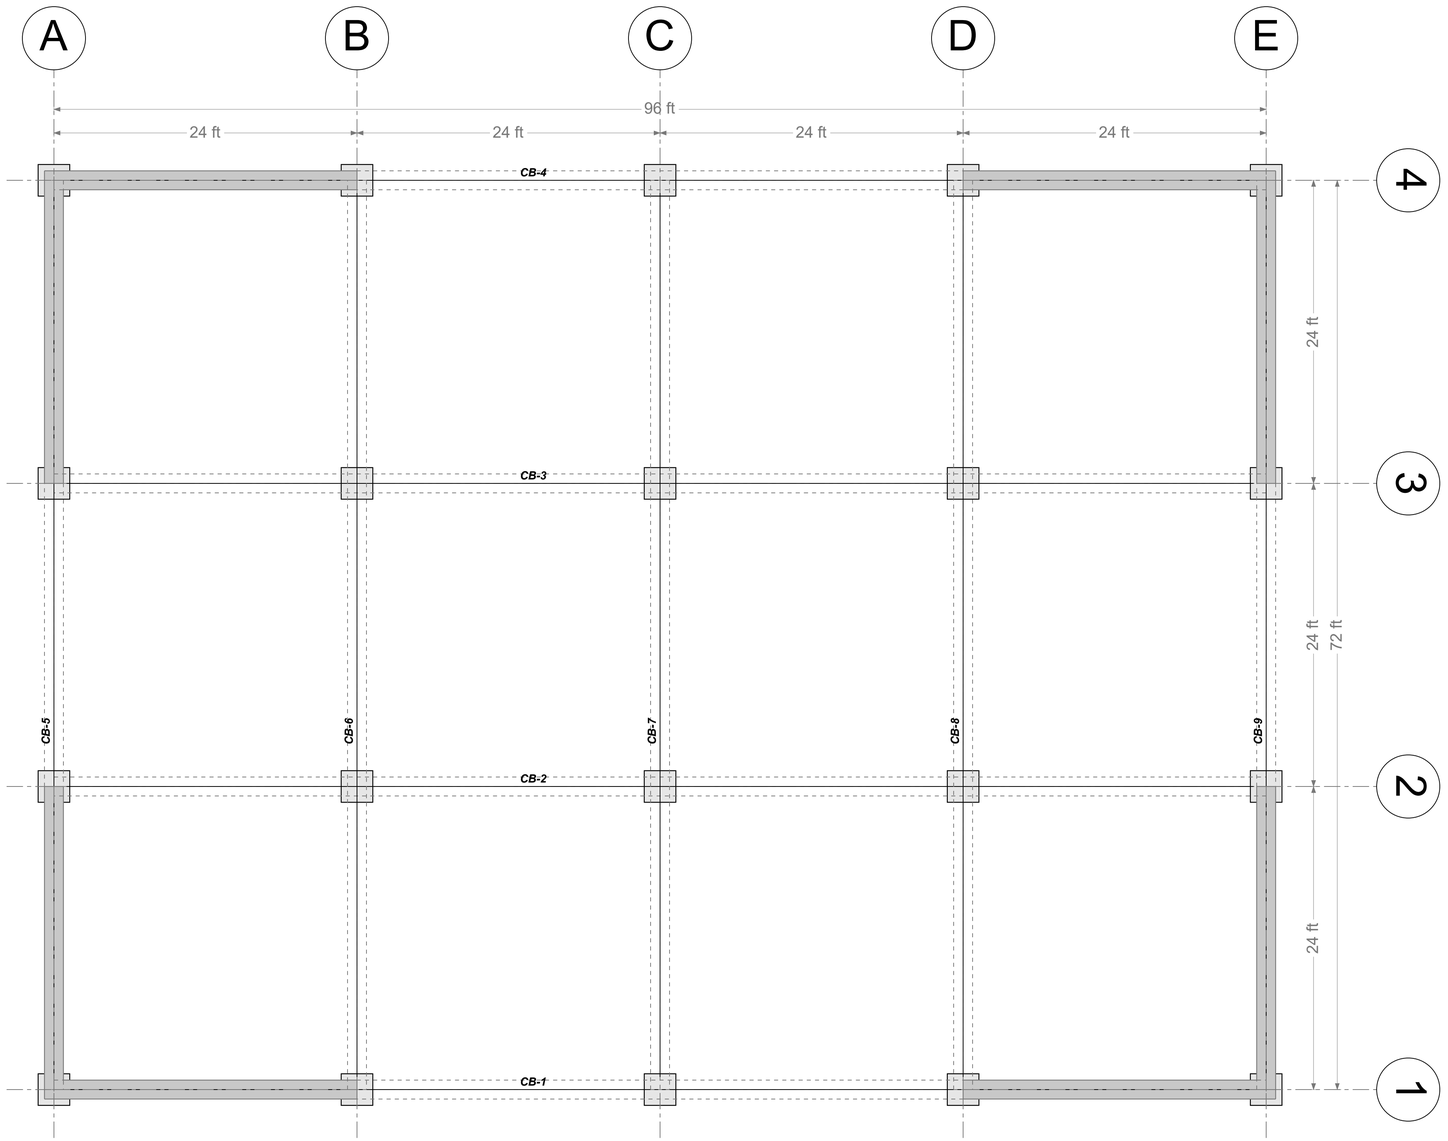

Story4 RC Beam Layout Plan

(Scale = 1"=6'-0")

www.csiamerica.com

No	Description	Date

Story4 RC Beam Layout Plan

Project Number	
Date	
Drawn By	
Checked By	

S-10

Scale

Story4 - Rebar Table

Beam Label	Span/Support	Width	Depth	Bar A	Bar B	Bar C	Bar D	Bar E	Bar F	Bar G	Zone A	Zone B	Zone C	Zone D	Zone E	Elevation Type
CB-1	Support-1	-	-	2-#6A	2-#6B	-	-	-	-	-	-	-	-	-	-	Elevatio
-	Span-1	18	30	-	-	-	-	-	-	-	#4@4.5	#4@14	#4@15	#4@14	#4@4.5	-
-	Support-2	-	-	-	-	2-#6C	2-#6D	-	-	-	-	-	-	-	-	-
-	Span-2	18	30	-	-	-	-	-	-	-	#4@4.5	#4@14	#4@15	#4@14.	#4@4.5	-
-	Support-3	-	-	-	-	2-#6C	2-#6D	-	-	-	-	-	-	-	-	-
-	Span-3	18	30	-	-	-	-	-	-	-	#4@4.5	#4@14.	#4@15	#4@14	#4@4.5	-
-	Support-4	-	-	-	-	2-#6C	2-#6D	-	-	-	-	-	-	-	-	-
-	Span-4	18	30	-	-	-	-	-	-	-	#4@4.5	-	#4@14	-	#4@4.5	-
-	Support-5	-	-	-	-	2-#6C	2-#6D	-	-	-	-	-	-	-	-	-
-	Span-5	18	30	-	-	-	-	-	-	-	#4@4.5	-	#4@14	-	#4@4.5	-
-	Support-6	-	-	2-#6A	2-#6B	-	-	-	-	-	-	-	-	-	-	-
CB-2	Support-1	-	-	2-#6A	2-#6B	-	-	-	-	-	-	-	-	-	-	Elevatio
-	Span-1	18	30	-	-	-	-	-	-	-	#4@4.5	#4@12.	#4@15	#4@13	#4@4.5	-
-	Support-2	-	-	-	-	2-#6C	2-#6D	-	-	-	-	-	-	-	-	-
-	Span-2	18	30	-	-	-	-	-	-	-	#4@4.5	#4@12.	#4@15	#4@12.	#4@4.5	-
-	Support-3	-	-	-	-	2-#6C	2-#6D	-	-	-	-	-	-	-	-	-
-	Span-3	18	30	-	-	-	-	-	-	-	#4@4.5	#4@12.	#4@15	#4@12.	#4@4.5	-
-	Support-4	-	-	-	-	2-#6C	2-#6D	-	-	-	-	-	-	-	-	-
-	Span-4	18	30	-	-	-	-	-	-	-	#4@4.5	#4@13	#4@15	#4@12.	#4@4.5	-
-	Support-5	-	-	2-#6A	2-#6B	-	-	-	-	-	-	-	-	-	-	-
CB-3	Support-1	-	-	2-#6A	2-#6B	-	-	-	-	-	-	-	-	-	-	Elevatio
-	Span-1	18	30	-	-	-	-	-	-	-	#4@4.5	#4@12.	#4@15	#4@13	#4@4.5	-
-	Support-2	-	-	-	-	2-#6C	2-#6D	-	-	-	-	-	-	-	-	-
-	Span-2	18	30	-	-	-	-	-	-	-	#4@4.5	#4@12.	#4@15	#4@12.	#4@4.5	-
-	Support-3	-	-	-	-	2-#6C	2-#6D	-	-	-	-	-	-	-	-	-
-	Span-3	18	30	-	-	-	-	-	-	-	#4@4.5	#4@12.	#4@15	#4@12.	#4@4.5	-
-	Support-4	-	-	-	-	2-#6C	2-#6D	-	-	-	-	-	-	-	-	-
-	Span-4	18	30	-	-	-	-	-	-	-	#4@4.5	#4@13	#4@15	#4@12.	#4@4.5	-
-	Support-5	-	-	2-#6A	2-#6B	-	-	-	-	-	-	-	-	-	-	-
CB-4	Support-1	-	-	2-#6A	2-#6B	-	-	-	-	-	-	-	-	-	-	Elevatio
-	Span-1	18	30	-	-	-	-	-	-	-	#4@4.5	#4@14	#4@15	#4@14	#4@4.5	-
-	Support-2	-	-	-	-	2-#6C	2-#6D	-	-	-	-	-	-	-	-	-
-	Span-2	18	30	-	-	-	-	-	-	-	#4@4.5	#4@14	#4@15	#4@14.	#4@4.5	-
-	Support-3	-	-	-	-	2-#6C	2-#6D	-	-	-	-	-	-	-	-	-
-	Span-3	18	30	-	-	-	-	-	-	-	#4@4.5	#4@14.	#4@15	#4@14	#4@4.5	-
-	Support-4	-	-	-	-	2-#6C	2-#6D	-	-	-	-	-	-	-	-	-
-	Span-4	18	30	-	-	-	-	-	-	-	#4@4.5	-	#4@14	-	#4@4.5	-
-	Support-5	-	-	-	-	2-#6C	2-#6D	-	-	-	-	-	-	-	-	-
-	Span-5	18	30	-	-	-	-	-	-	-	#4@4.5	-	#4@14	-	#4@4.5	-
-	Support-6	-	-	2-#6A	2-#6B	-	-	-	-	-	-	-	-	-	-	-
CB-5	Support-1	-	-	2-#6A	2-#6B	-	-	-	-	-	-	-	-	-	-	Elevatio
-	Span-1	18	30	-	-	-	-	-	-	-	#4@4.5	#4@14	#4@15	#4@14	#4@4.5	-
-	Support-2	-	-	-	-	2-#6C	2-#6D	-	-	-	-	-	-	-	-	-
-	Span-2	18	30	-	-	-	-	-	-	-	#4@4.5	#4@14	#4@15	#4@14	#4@4.5	-
-	Support-3	-	-	-	-	2-#6C	2-#6D	-	-	-	-	-	-	-	-	-
-	Span-3	18	30	-	-	-	-	-	-	-	#4@4.5	-	#4@14	-	#4@4.5	-
-	Support-4	-	-	-	-	2-#6C	2-#6D	-	-	-	-	-	-	-	-	-
-	Span-4	18	30	-	-	-	-	-	-	-	#4@4.5	-	#4@14	-	#4@4.5	-
-	Support-5	-	-	2-#6A	2-#6B	-	-	-	-	-	-	-	-	-	-	-
CB-6	Support-1	-	-	2-#6A	2-#6B	-	-	-	-	-	-	-	-	-	-	Elevatio
-	Span-1	18	30	-	-	-	-	-	-	-	#4@4.5	#4@12.	#4@15	#4@13	#4@4.5	-
-	Support-2	-	-	-	-	2-#6C	2-#6D	-	-	-	-	-	-	-	-	-
-	Span-2	18	30	-	-	-	-	-	-	-	#4@4.5	#4@12.	#4@15	#4@12.	#4@4.5	-
-	Support-3	-	-	-	-	2-#6C	2-#6D	-	-	-	-	-	-	-	-	-
-	Span-3	18	30	-	-	-	-	-	-	-	#4@4.5	#4@13	#4@15	#4@12.	#4@4.5	-
-	Support-4	-	-	2-#6A	2-#6B	-	-	-	-	-	-	-	-	-	-	-
CB-7	Support-1	-	-	2-#6A	2-#6B	-	-	-	-	-	-	-	-	-	-	Elevatio
-	Span-1	18	30	-	-	-	-	-	-	-	#4@4.5	#4@12.	#4@15	#4@13	#4@4.5	-
-	Support-2	-	-	-	-	2-#6C	2-#6D	-	-	-	-	-	-	-	-	-
-	Span-2	18	30	-	-	-	-	-	-	-	#4@4.5	#4@12.	#4@15	#4@12.	#4@4.5	-
-	Support-3	-	-	-	-	2-#6C	2-#6D	-	-	-	-	-	-	-	-	-
-	Span-3	18	30	-	-	-	-	-	-	-	#4@4.5	#4@13	#4@15	#4@12.	#4@4.5	-
-	Support-4	-	-	2-#6A	2-#6B	-	-	-	-	-	-	-	-	-	-	-
CB-8	Support-1	-	-	2-#6A	2-#6B	-	-	-	-	-	-	-	-	-	-	Elevatio
-	Span-1	18	30	-	-	-	-	-	-	-	#4@4.5	#4@12.	#4@15	#4@13	#4@4.5	-
-	Support-2	-	-	-	-	2-#6C	2-#6D	-	-	-	-	-	-	-	-	-
-	Span-2	18	30	-	-	-	-	-	-	-	#4@4.5	#4@12.	#4@15	#4@12.	#4@4.5	-
-	Support-3	-	-	-	-	2-#6C	2-#6D	-	-	-	-	-	-	-	-	-
-	Span-3	18	30	-	-	-	-	-	-	-	#4@4.5	#4@13	#4@15	#4@12.	#4@4.5	-
-	Support-4	-	-	2-#6A	2-#6B	-	-	-	-	-	-	-	-	-	-	-
CB-9	Support-1	-	-	2-#6A	2-#6B	-	-	-	-	-	-	-	-	-	-	Elevatio
-	Span-1	18	30	-	-	-	-	-	-	-	#4@4.5	#4@14	#4@15	#4@14	#4@4.5	-
-	Support-2	-	-	-	-	2-#6C	2-#6D	-	-	-	-	-	-	-	-	-
-	Span-2	18	30	-	-	-	-	-	-	-	#4@4.5	#4@14	#4@15	#4@14	#4@4.5	-
-	Support-3	-	-	-	-	2-#6C	2-#6D	-	-	-	-	-	-	-	-	-
-	Span-3	18	30	-	-	-	-	-	-	-	#4@4.5	-	#4@14	-	#4@4.5	-
-	Support-4	-	-	-	-	2-#6C	2-#6D	-	-	-	-	-	-	-	-	-
-	Span-4	18	30	-	-	-	-	-	-	-	#4@4.5	-	#4@14	-	#4@4.5	-
-	Support-5	-	-	2-#6A	2-#6B	-	-	-	-	-	-	-	-	-	-	-

Story4:RC Beams-BOQ Summary

Sr. No.	Item	Quantity	Unit
1	Longitudinal Bars	5.46	ton
2	Ties and Stirrups	3.25	ton
3	Total Rebars	8.71	ton
4	Total Beam Length	744	ft
5	Total Beam Volume	2,790	cu ft
6	Weight/Volume	6.25	lb/cu ft
Note	Does not include weight of Typical Bars		

Story4:RC Beams-Rebar Weight Summary

Sr. No.	Size	Area (in²)	Length (ft)	Weight (ton)
1	#4	0.2	9,548.45	3.25
2	#6	0.44	7,297.22	5.46
Note	Does not include Typical Bars			

www.csiamerica.com


No	Description	Date

Story4 RC Beam Rebar Table

Project Number	
Date	
Drawn By	
Checked By	

S-11

Scale

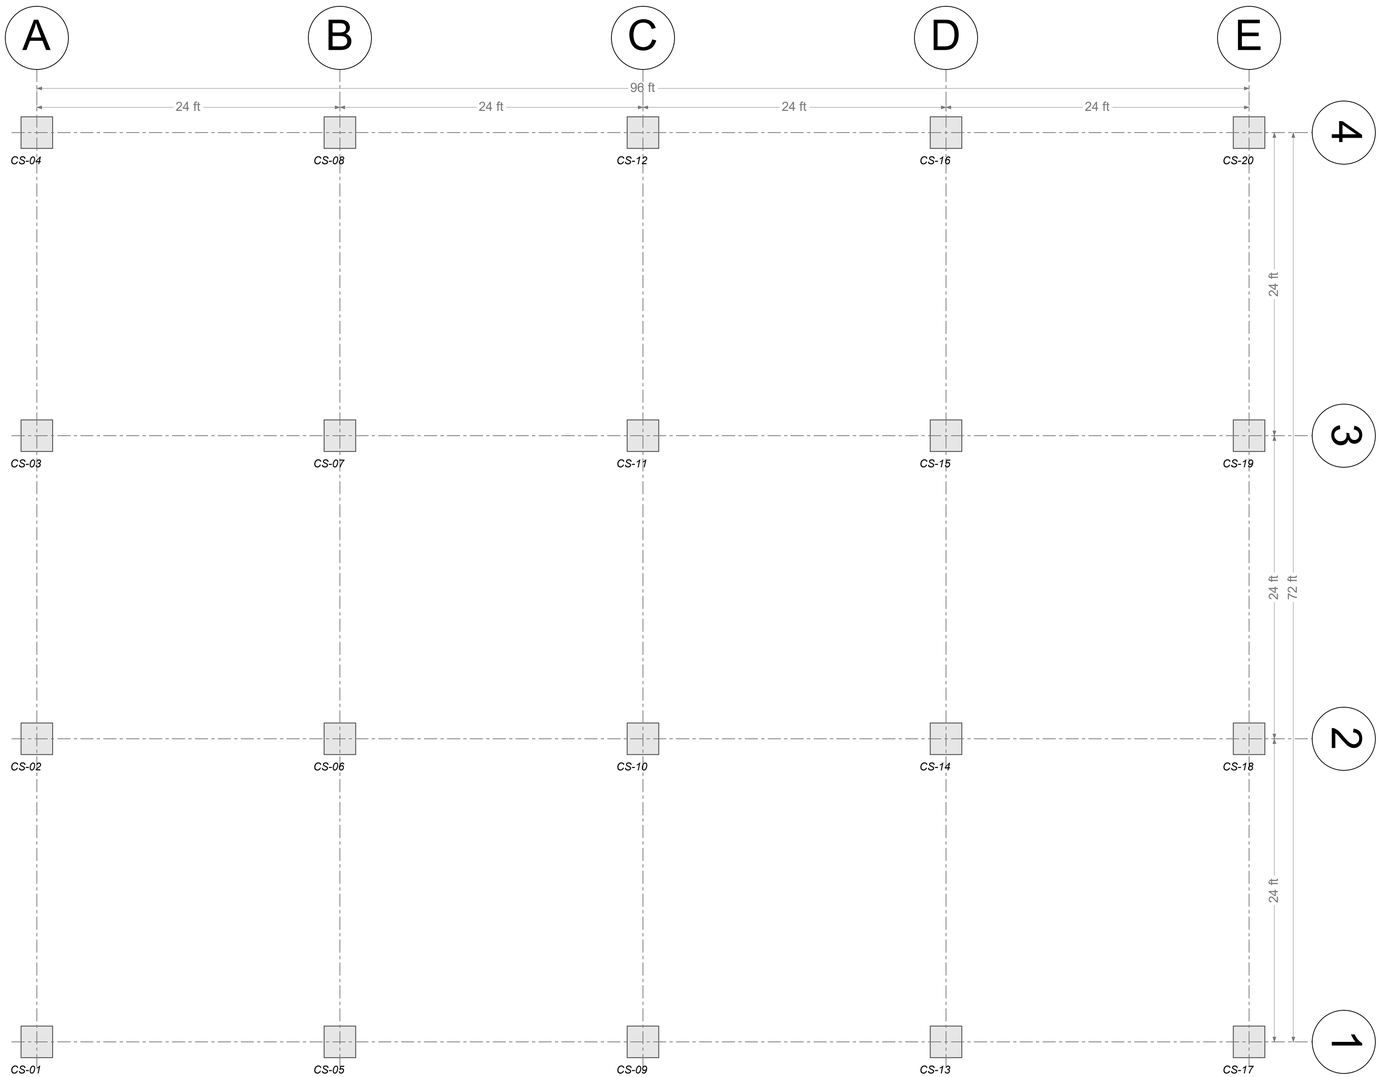

CSG-01 Layout Plan
(Scale = 1"=6'-0")

CSG-01-BOQ Summary

Sr. No.	Item	Quantity	Unit
1	Longitudinal Bars	29.2	ton
2	Ties and Stirrups	5.88	ton
3	Total Rebars	35.08	ton
4	Total Column Length	1,200	ft
5	Total Column Volume	7,500	cu ft
6	Weight/Volume	9.35	lb/cu ft

CSG-01-Rebar Weight Summary

Sr. No.	Size	Area (in²)	Length (ft)	Weight (ton)
1	#3	0.11	31,440.19	5.88
2	#9	1	9,600	16.33

www.csiamerica.com


No	Description	Date

CSG-01 Layout Plan

Project Number	
Date	
Drawn By	
Checked By	

S-12


Scale

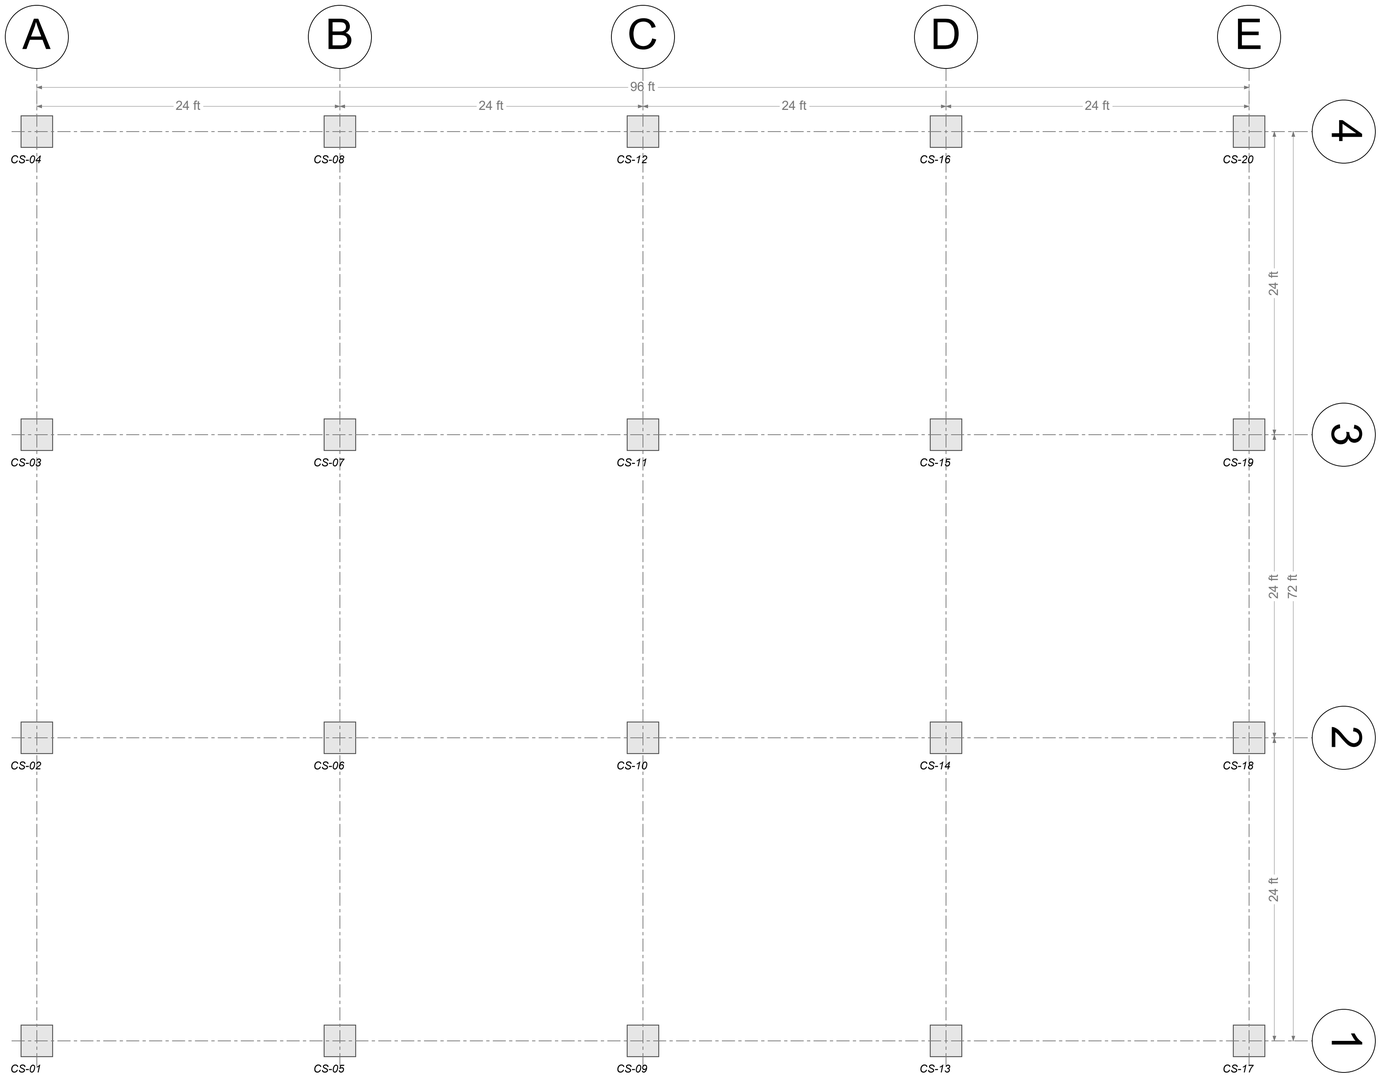

RC Column Layout Plan
(Scale = 1"=6'-0")

RC Column Section Table

Story	CSG-01
Story5	(1 No.)
Story4	
Story3	
Story2	
Story1	
Base	

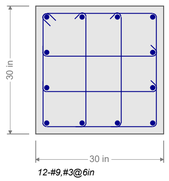

12-#9,#3@6in

www.csiamerica.com


No	Description	Date

RC Column Layout Plan

Project Number	
Date	
Drawn By	
Checked By	

S-13

Scale

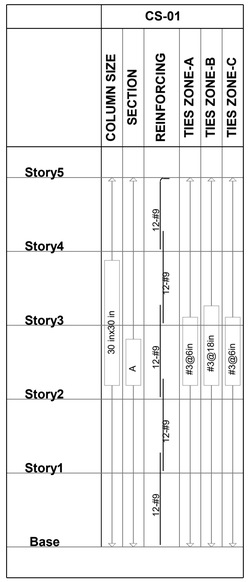


RC Column Elevation Summary
(Scale = 1"=2'-0")

RC Columns-BOQ Summary

Sr. No.	Item	Quantity	Unit
1	Longitudinal Bars	29.2	ton
2	Ties and Stirrups	5.88	ton
3	Total Rebars	35.08	ton
4	Total Column Length	1,200	ft
5	Total Column Volume	7,500	cu ft
6	Weight/Volume	9.35	lb/cu ft

RC Columns-Rebar Weight Summary

Sr. No.	Size	Area (in²)	Length (ft)	Weight (ton)
1	#3	0.11	31,440.19	5.88
2	#9	1	9,600	16.33

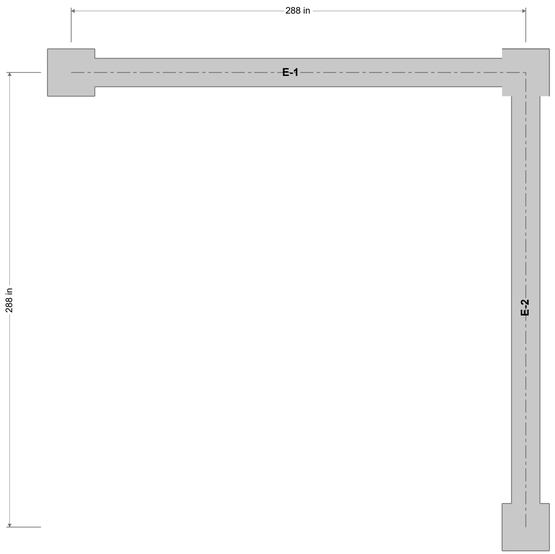

WS-1:Base Plan
(Scale = 1"=4'-0")

www.csiamerica.com


No	Description	Date

RC Column Elevation Summary


Project Number	
Date	
Drawn By	
Checked By	

S-14

Scale

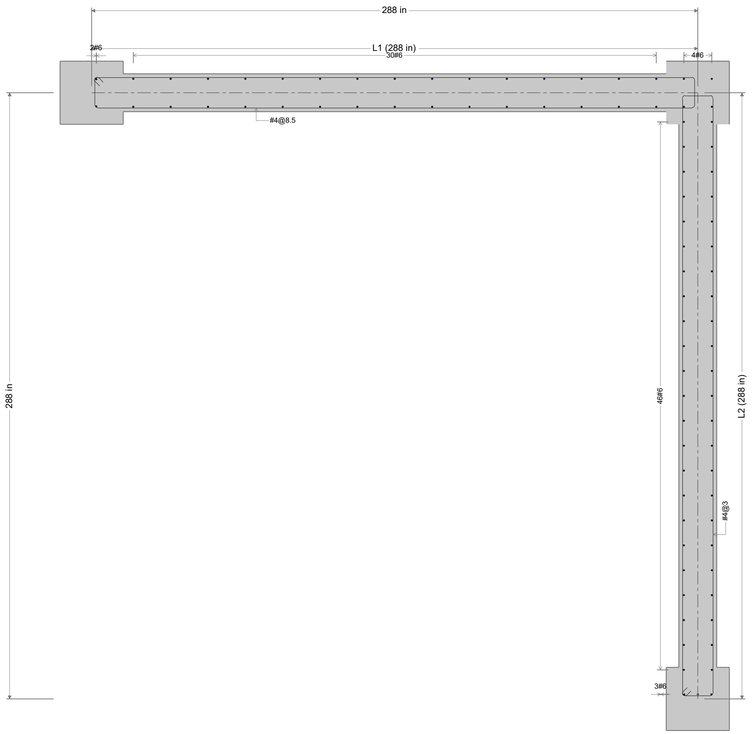

WS-1:Section-Story1
(Scale = 1"=3'-0")

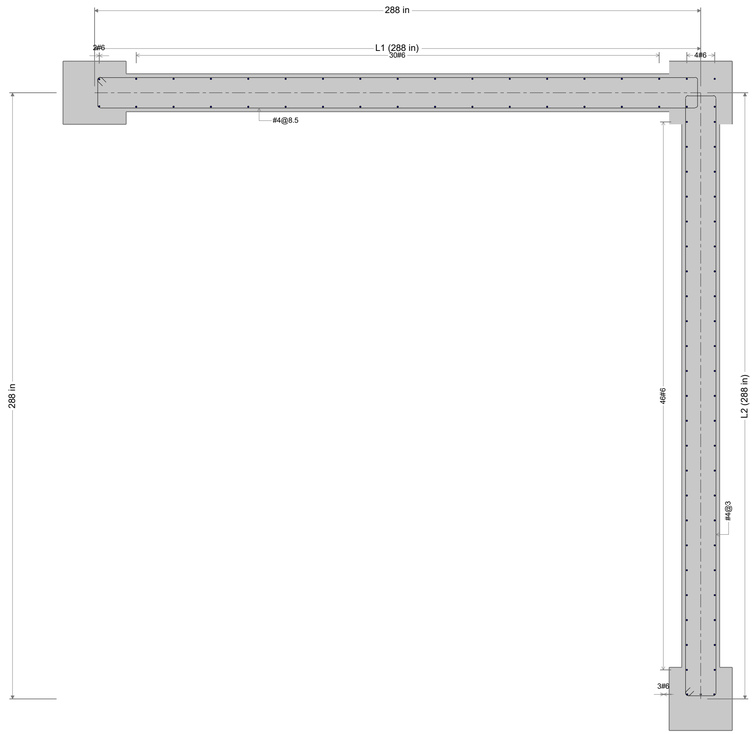

WS-1:Section-Story2
(Scale = 1"=3'-0")

www.csiamerica.com


No	Description	Date

WS-1:Section-Story1


Project Number	
Date	
Drawn By	
Checked By	

S-15

Scale

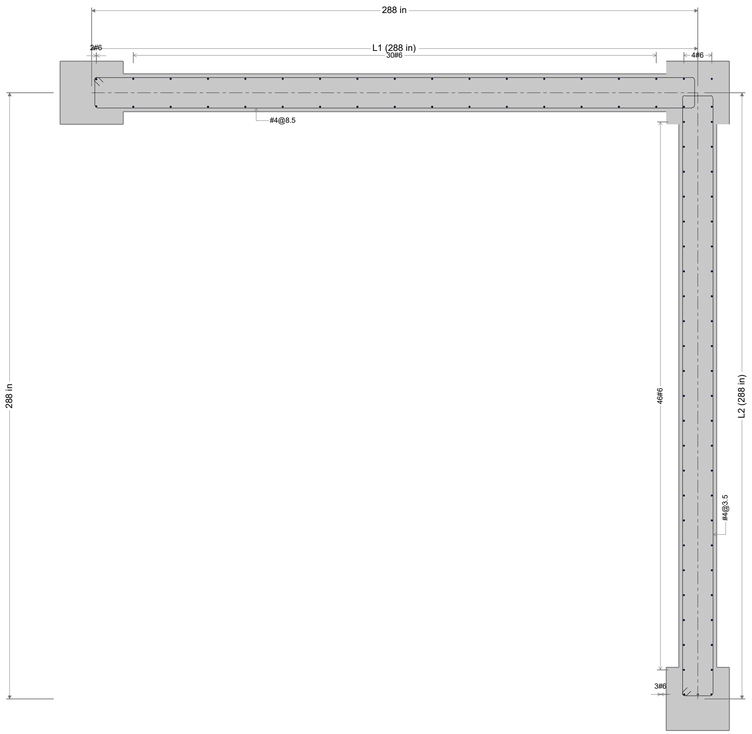

WS-1:Section-Story3
(Scale = 1"=3'-0")

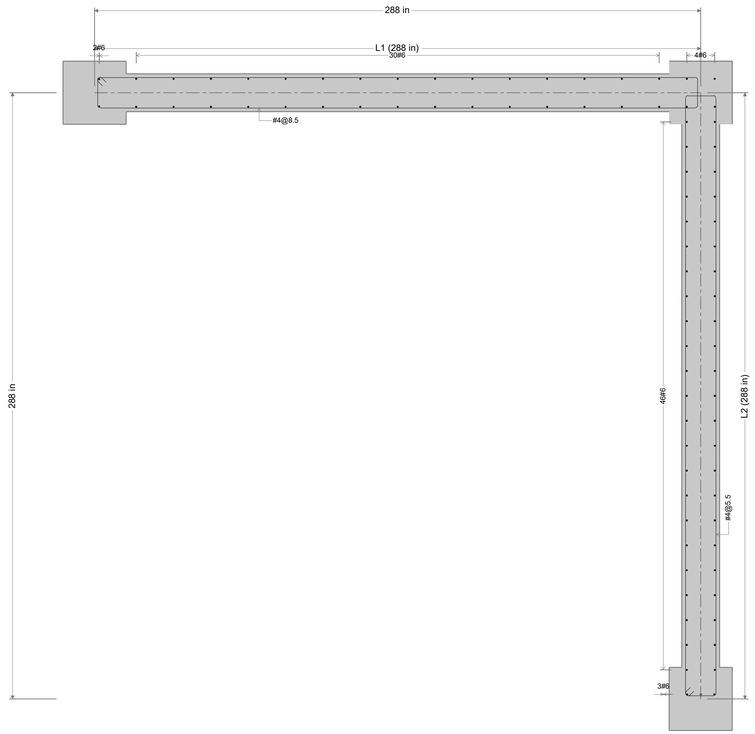

WS-1:Section-Story4
(Scale = 1"=3'-0")

www.csiamerica.com


No	Description	Date

WS-1:Section-Story3


Project Number	
Date	
Drawn By	
Checked By	

S-16

Scale

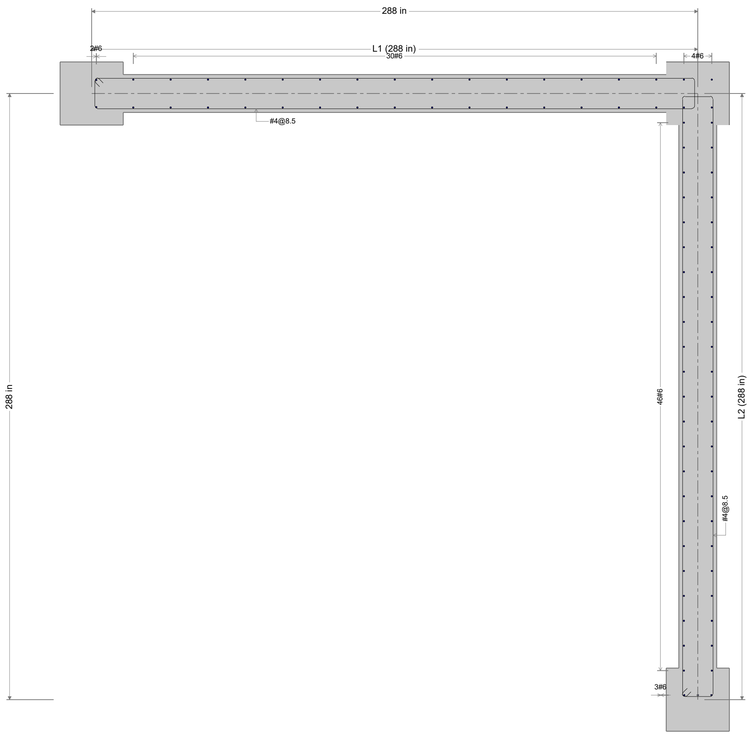

WS-1:Section-Story5
(Scale = 1"=3'-0")

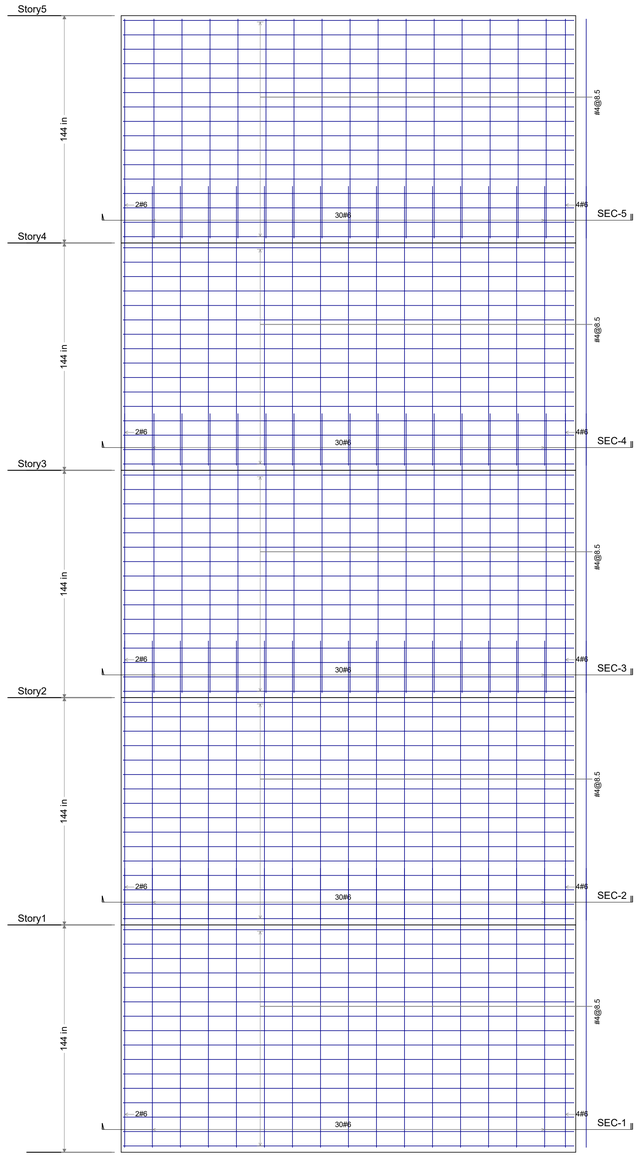

WS-1:E-1
(Scale = 1"=4'-0")

www.csiamerica.com


No	Description	Date

WS-1:Section-Story5


Project Number	
Date	
Drawn By	
Checked By	

S-17

Scale

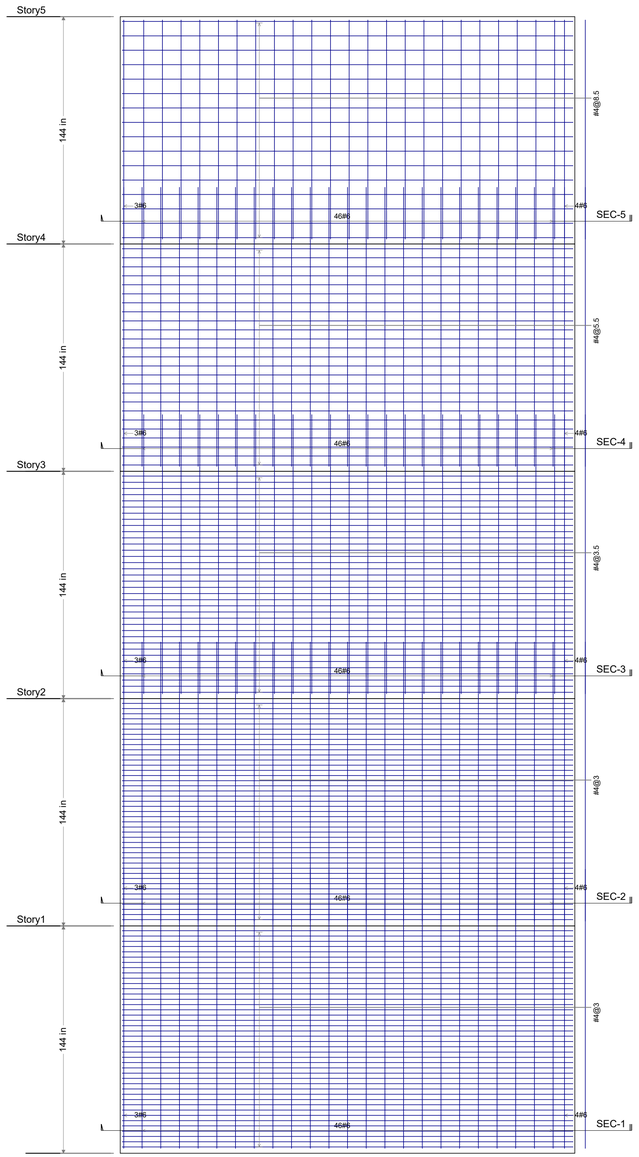

WS-1:E-2
(Scale = 1"=4'-0")

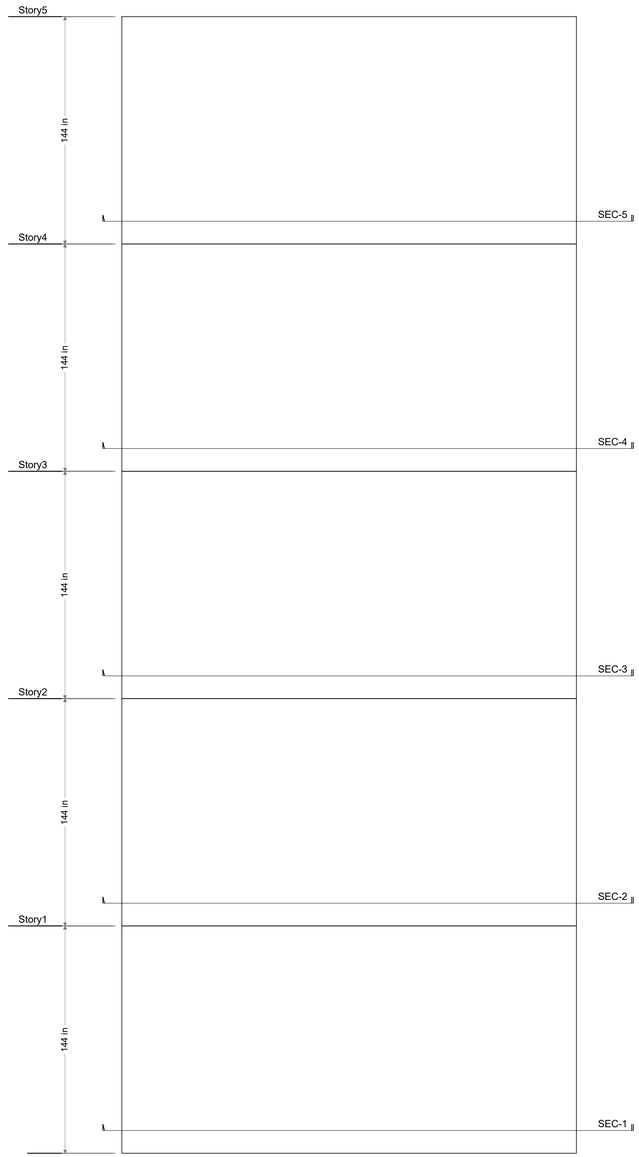

WS-1:E-1 (No Bars)
(Scale = 1"=4'-0")

www.csiamerica.com


No	Description	Date

WS-1:E-2

Project Number	
Date	
Drawn By	
Checked By	

S-18

Scale

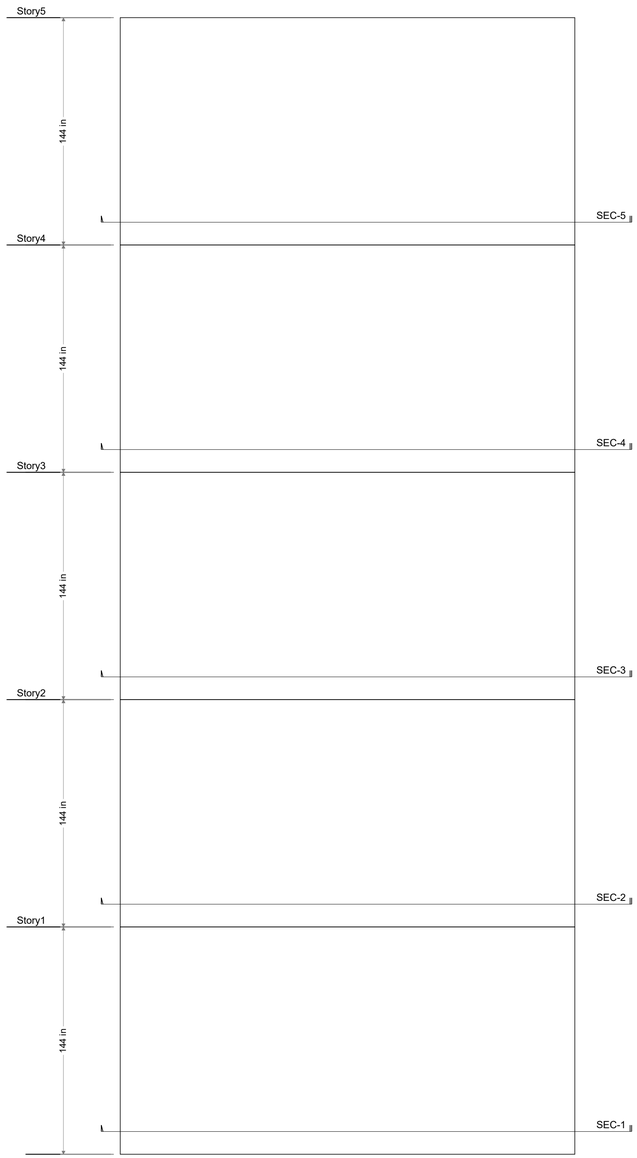

WS-1:E-2 (No Bars)
(Scale = 1"=4'-0")

WS-1-BOQ Summary

Sr. No.	Item	Quantity	Unit
1	Longitudinal Bars	4.57	ton
2	Ties and Stirrups	4.28	ton
3	Total Rebars	8.85	ton

WS-1-Rebar Weight Summary

Sr. No.	Size	Area (in²)	Length (ft)	Weight (ton)
1	#4	0.2	12,567.33	4.28
2	#6	0.44	6,105.83	4.57

www.csiamerica.com


No	Description	Date

WS-1:E-2 (No Bars)


Project Number	
Date	
Drawn By	
Checked By	

S-19

Scale

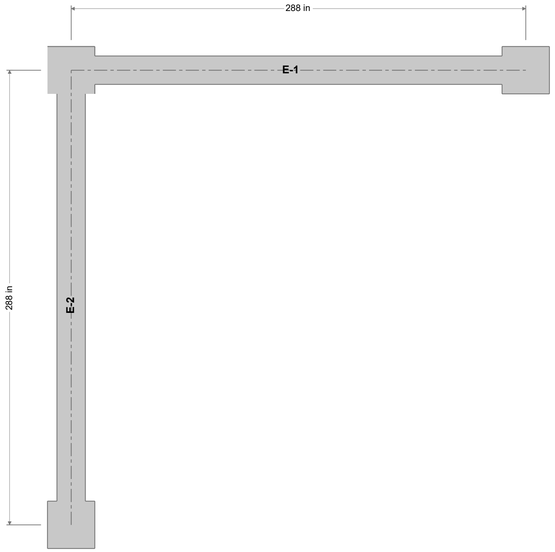

WS-2:Base Plan
(Scale = 1"=4'-0")

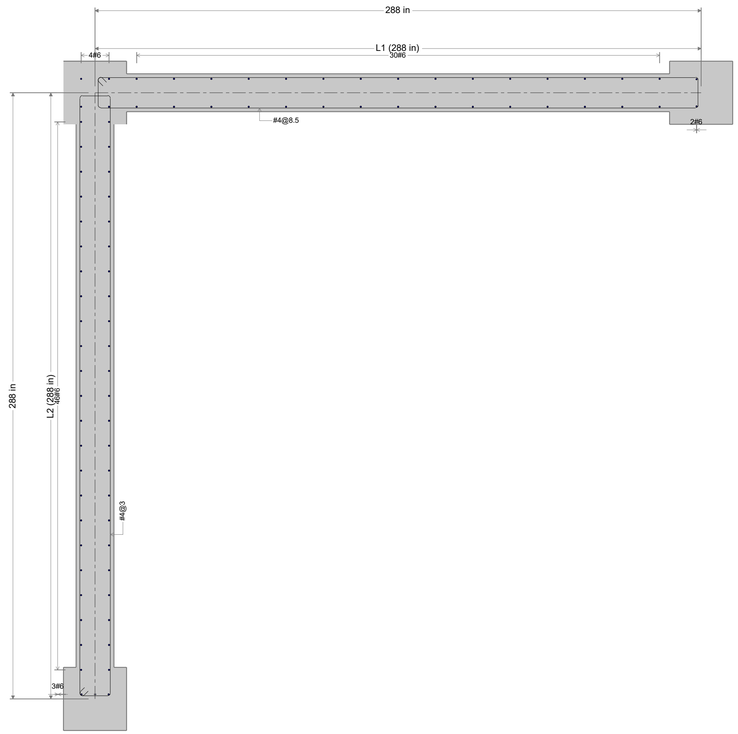

WS-2:Section-Story1
(Scale = 1"=3'-0")

www.csiamerica.com


No	Description	Date

WS-2:Base Plan


Project Number	
Date	
Drawn By	
Checked By	

S-20

Scale

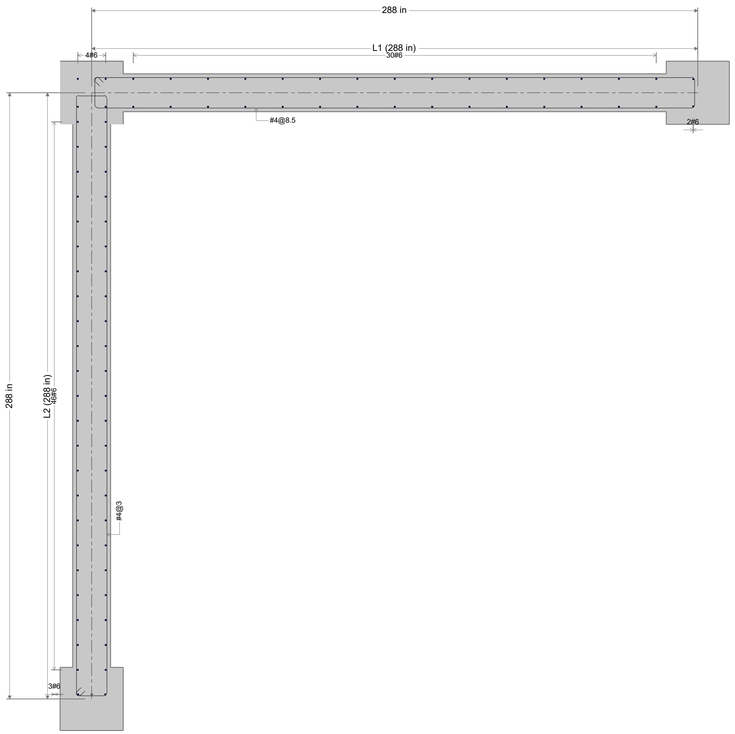

WS-2:Section-Story2
(Scale = 1"=3'-0")

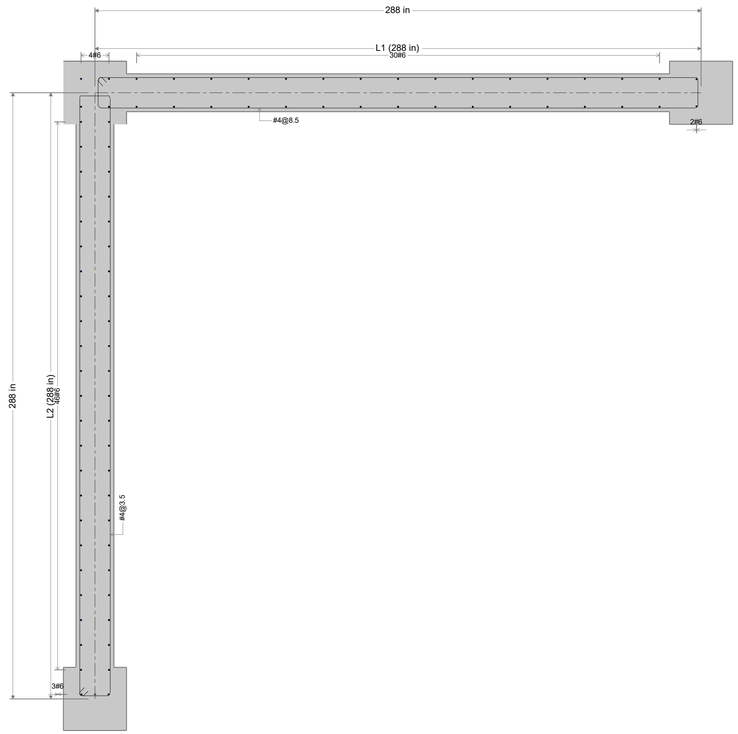

WS-2:Section-Story3
(Scale = 1"=3'-0")

www.csiamerica.com


No	Description	Date

WS-2:Section-Story2


Project Number	
Date	
Drawn By	
Checked By	

S-21

Scale

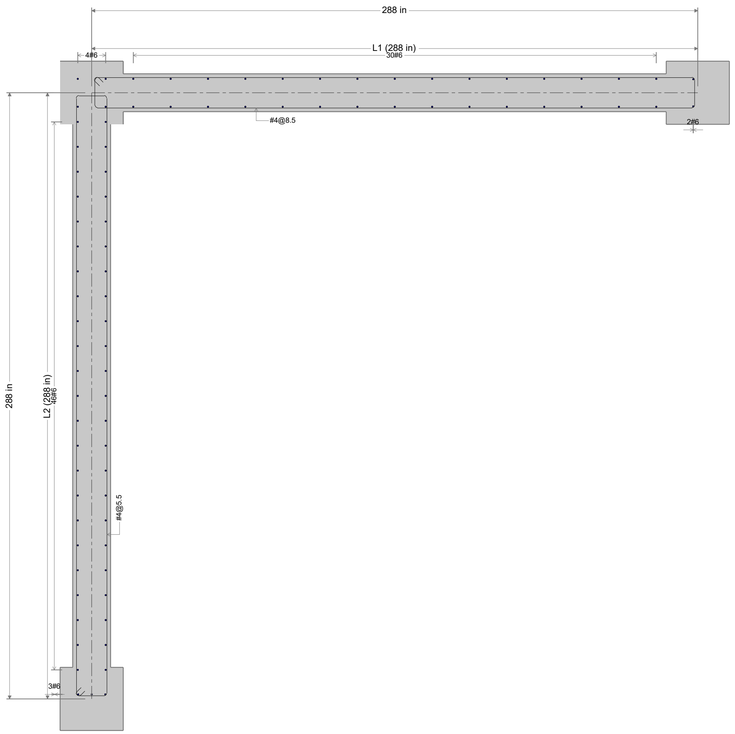

WS-2:Section-Story4
(Scale = 1"=3'-0")

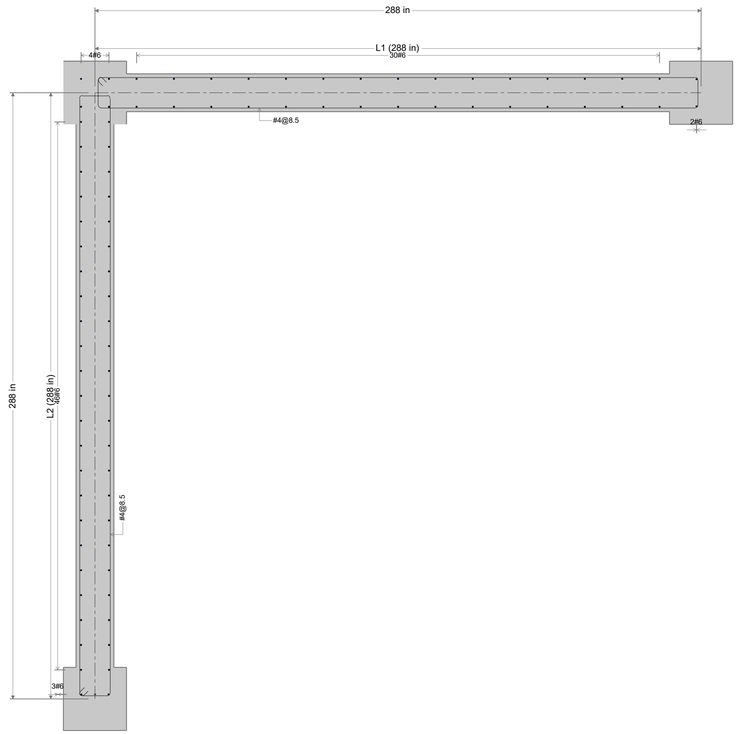

WS-2:Section-Story5
(Scale = 1"=3'-0")

www.csiamerica.com


No	Description	Date

WS-2:Section-Story4


Project Number	
Date	
Drawn By	
Checked By	

S-22

Scale

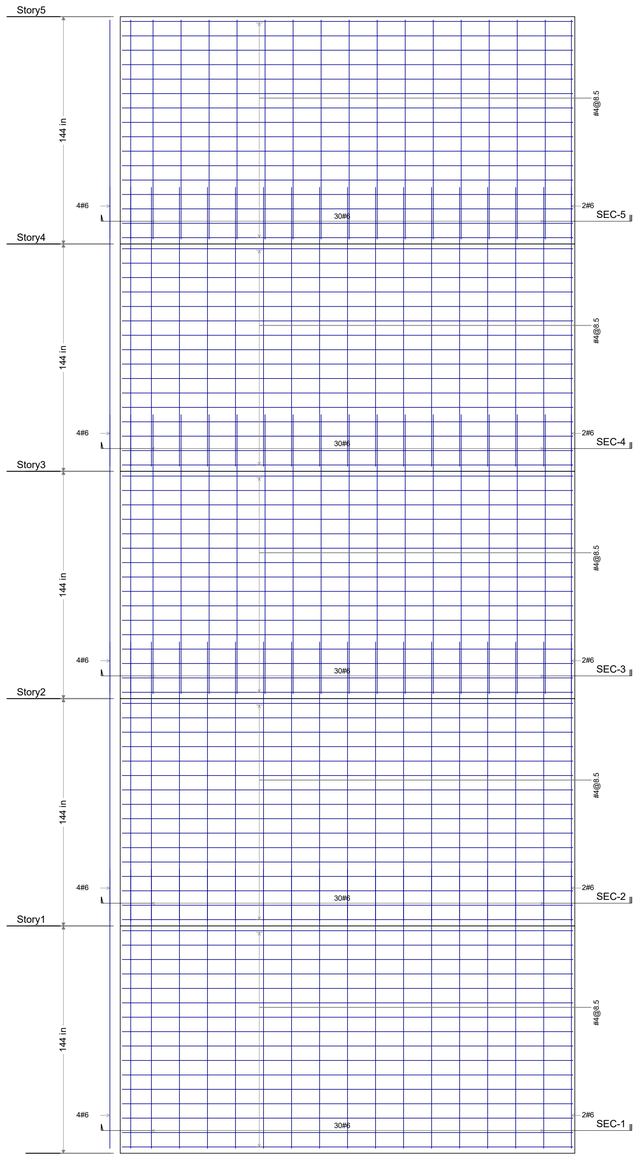

WS-2:E-1
(Scale = 1"=4'-0")

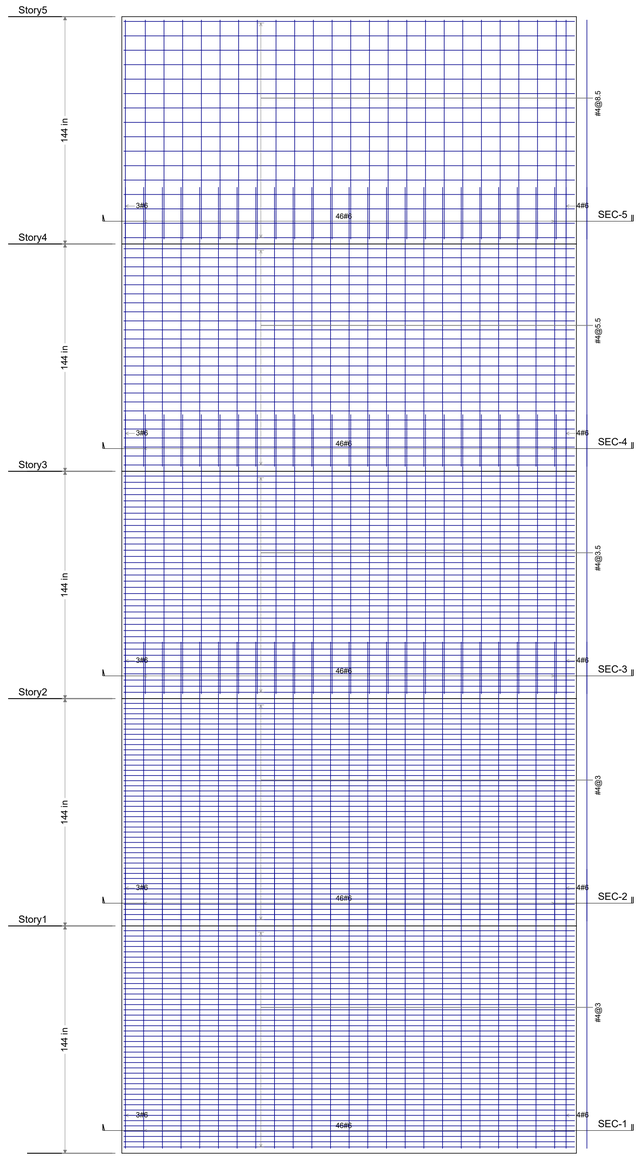

WS-2:E-2
(Scale = 1"=4'-0")

www.csiamerica.com


No	Description	Date

WS-2:E-1


Project Number	
Date	
Drawn By	
Checked By	

S-23

Scale

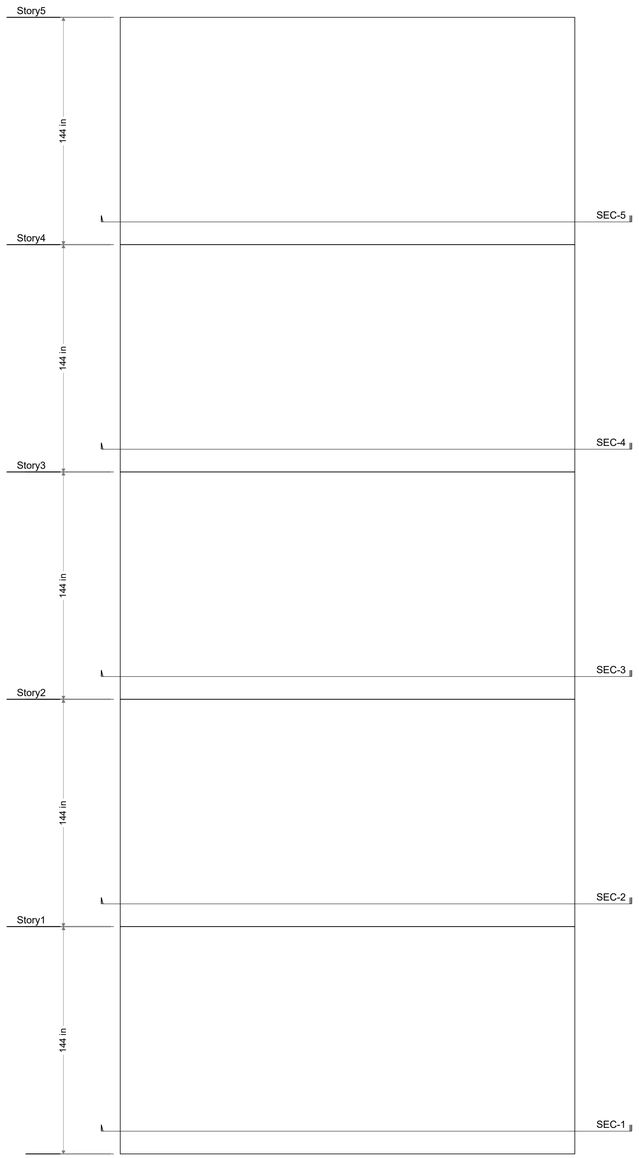

WS-2:E-1 (No Bars)
(Scale = 1"=4'-0")

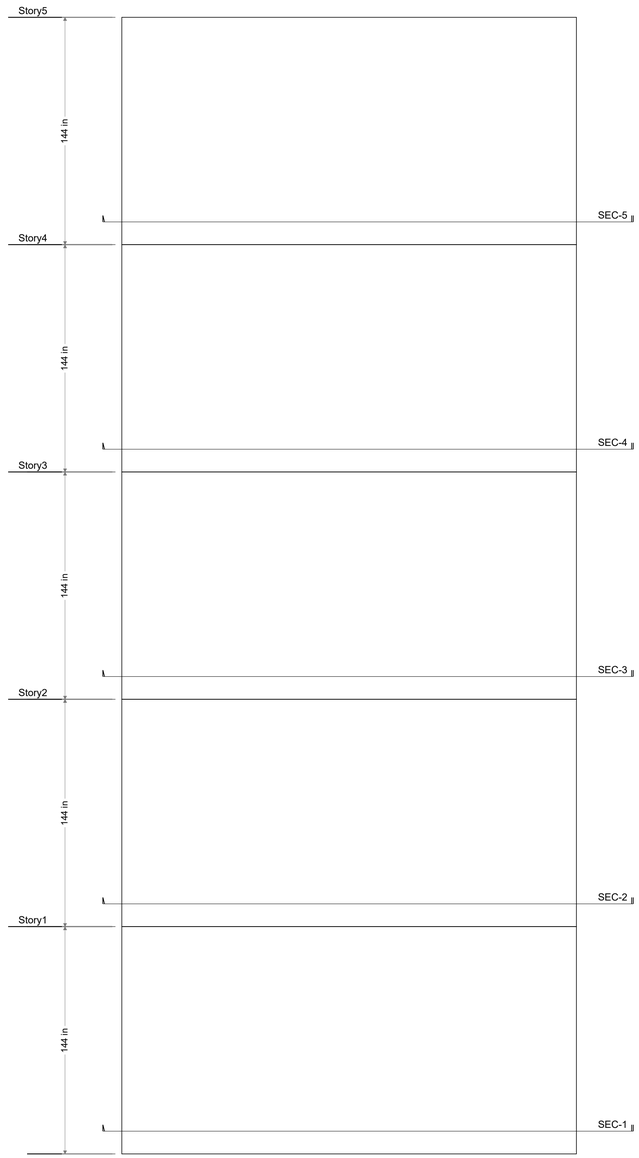

WS-2:E-2 (No Bars)
(Scale = 1"=4'-0")

WS-2-BOQ Summary

Sr. No.	Item	Quantity	Unit
1	Longitudinal Bars	4.57	ton
2	Ties and Stirrups	4.28	ton
3	Total Rebars	8.85	ton

WS-2-Rebar Weight Summary

Sr. No.	Size	Area (in²)	Length (ft)	Weight (ton)
1	#4	0.2	12,567.33	4.28
2	#6	0.44	6,105.83	4.57

www.csiamerica.com


No	Description	Date

WS-2:E-1 (No Bars)


Project Number	
Date	
Drawn By	
Checked By	

S-24

Scale

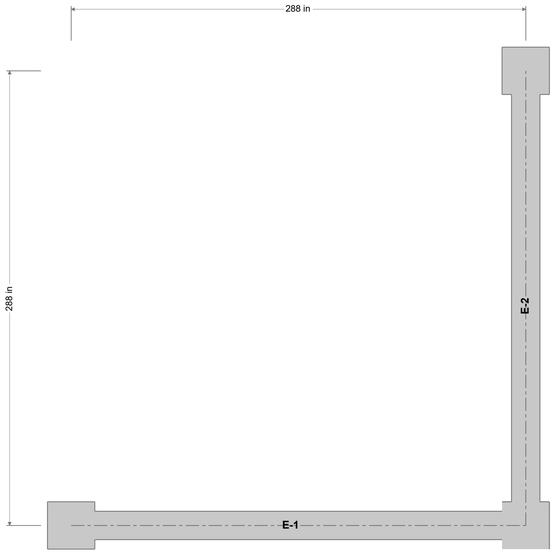

WS-3:Base Plan
(Scale = 1"=4'-0")

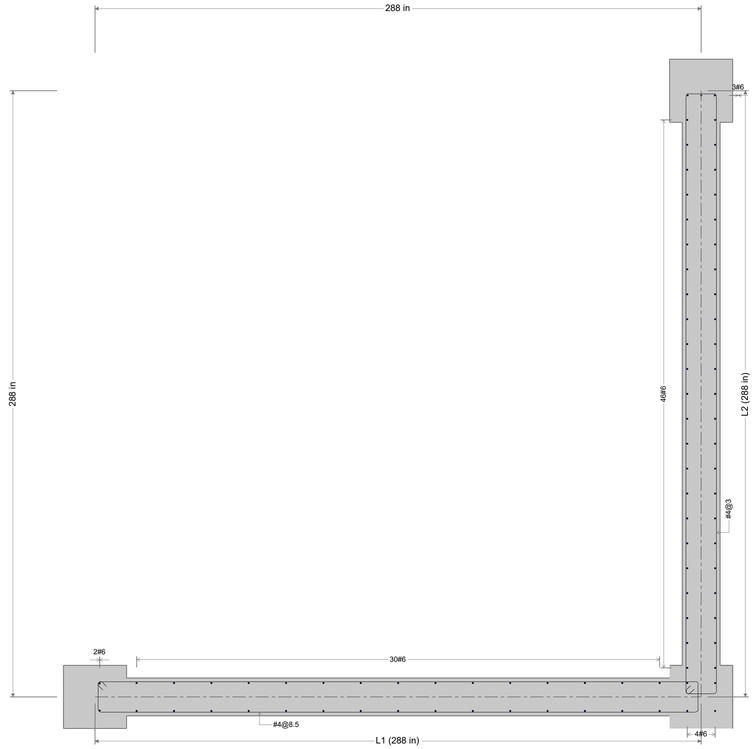

WS-3:Section-Story1
(Scale = 1"=3'-0")

www.csiamerica.com


No	Description	Date

WS-3:Base Plan


Project Number	
Date	
Drawn By	
Checked By	

S-25

Scale

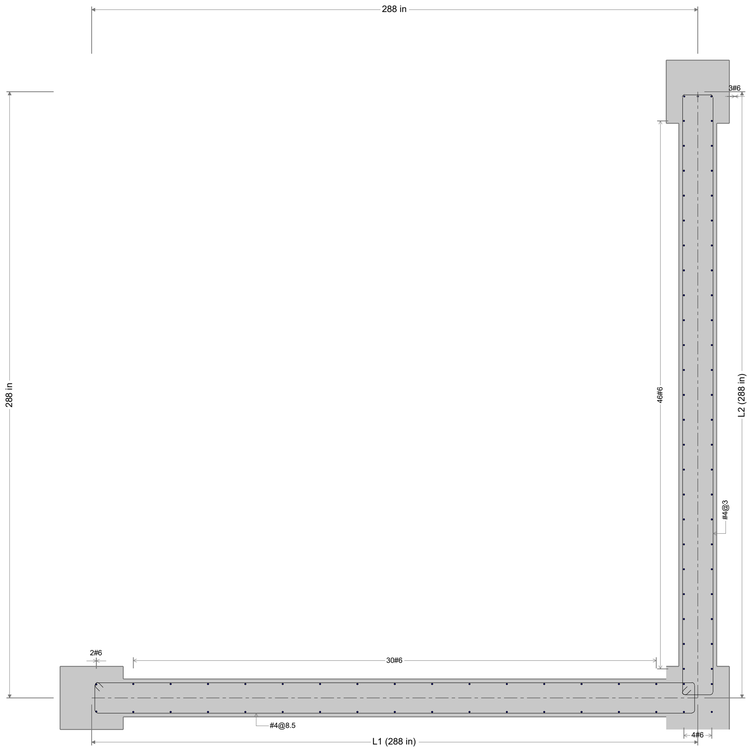

WS-3:Section-Story2
(Scale = 1"=3'-0")

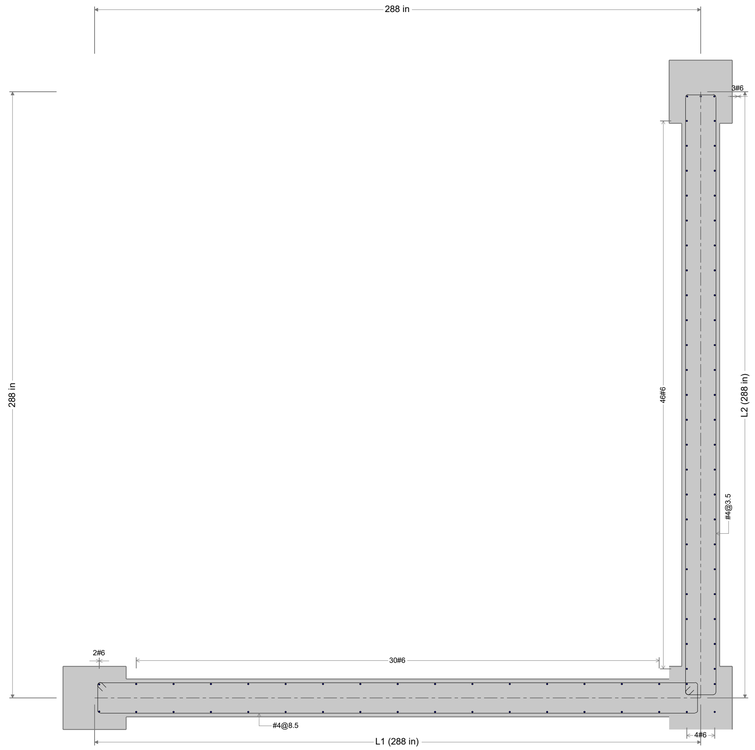

WS-3:Section-Story3
(Scale = 1"=3'-0")

www.csiamerica.com


No	Description	Date

WS-3:Section-Story2


Project Number	
Date	
Drawn By	
Checked By	

S-26

Scale

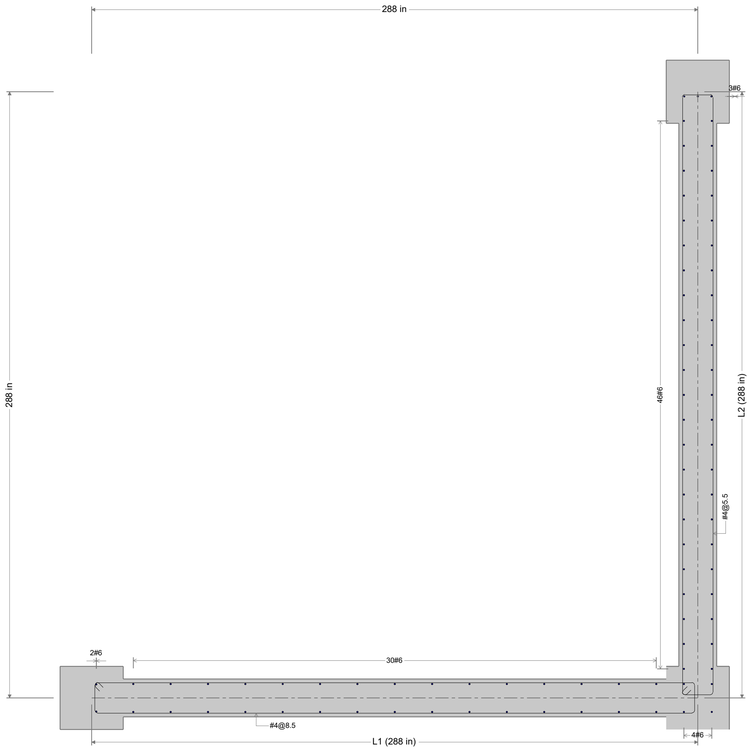

WS-3:Section-Story4
(Scale = 1"=3'-0")

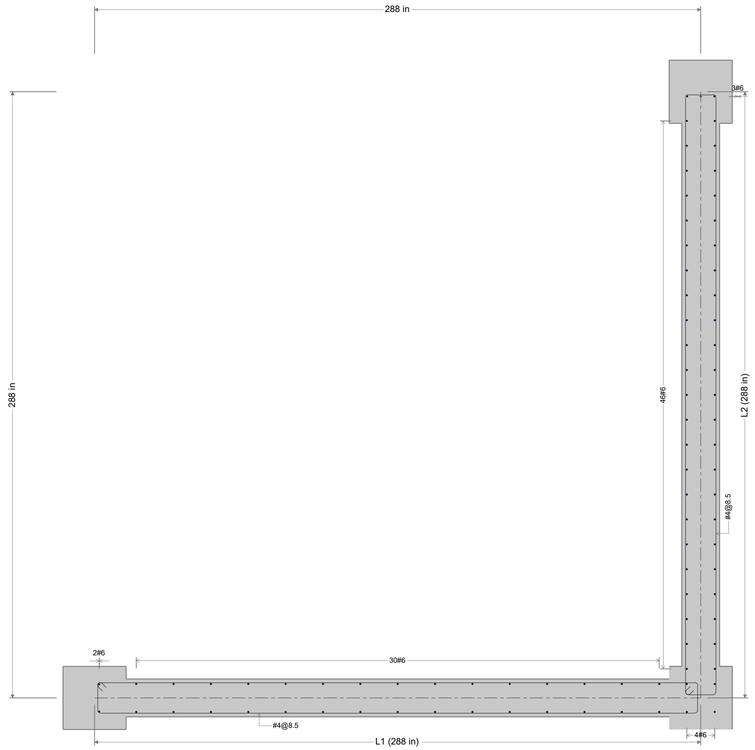

WS-3:Section-Story5
(Scale = 1"=3'-0")

www.csiamerica.com


No	Description	Date

WS-3:Section-Story4


Project Number	
Date	
Drawn By	
Checked By	

S-27

Scale

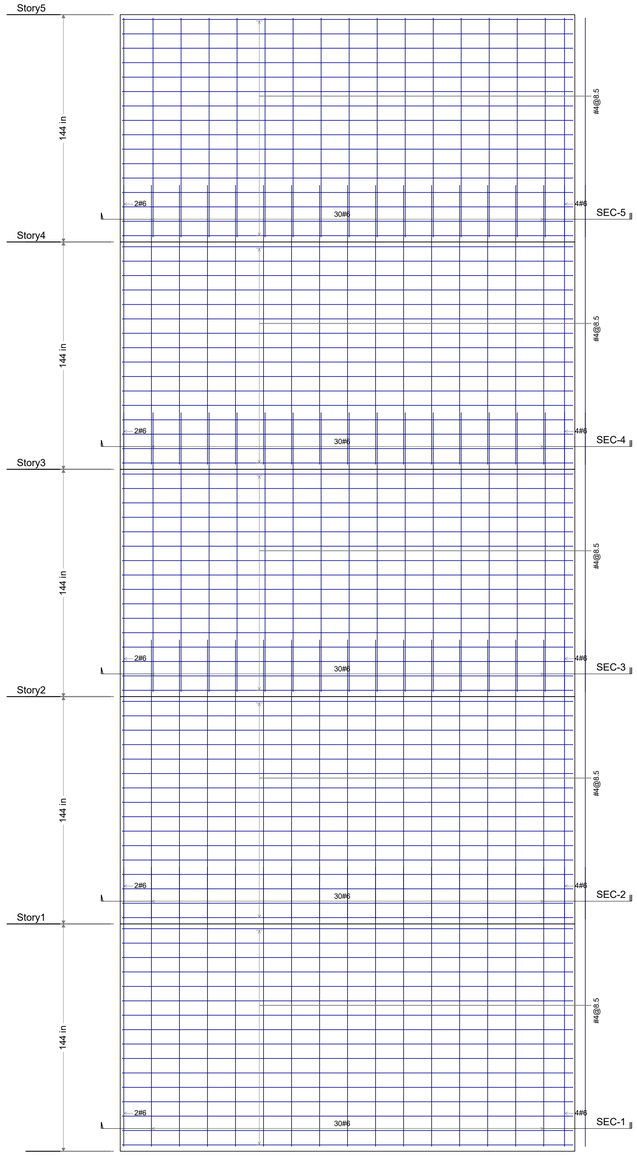

WS-3:E-1
(Scale = 1"=4'-0")

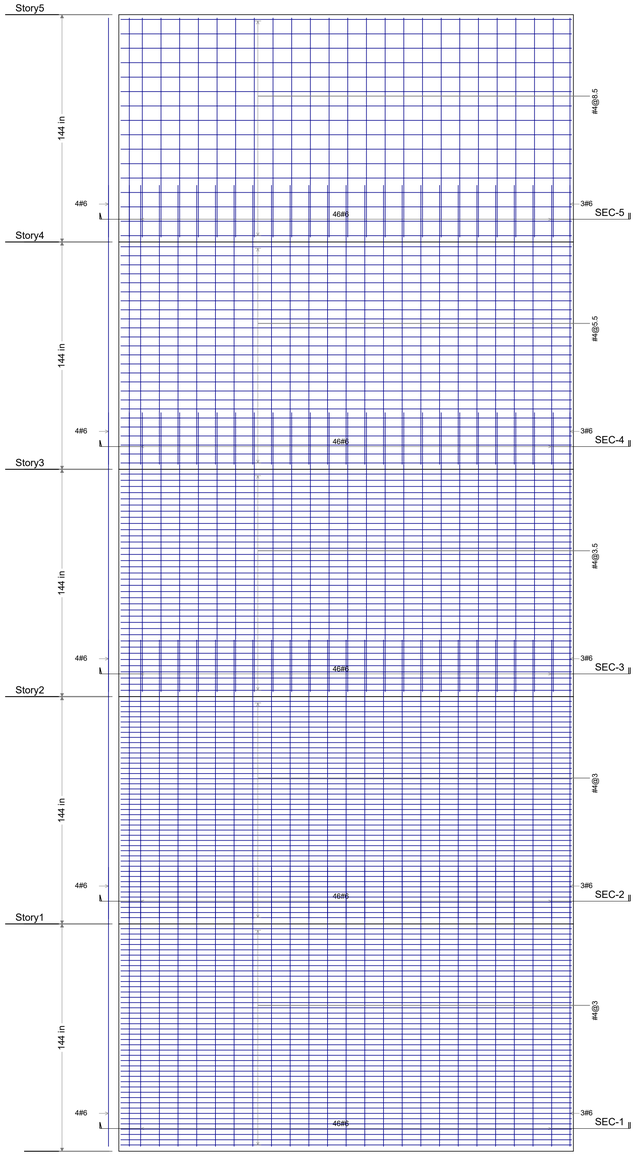

WS-3:E-2
(Scale = 1"=4'-0")

www.csiamerica.com


No	Description	Date

WS-3:E-1


Project Number	
Date	
Drawn By	
Checked By	

S-28

Scale

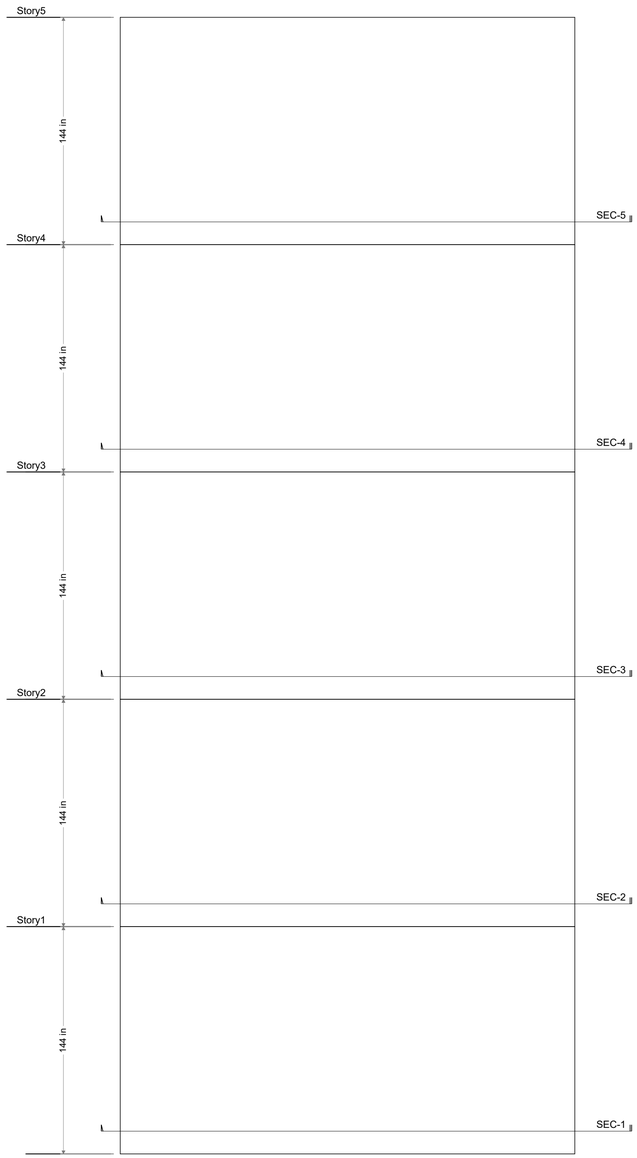

WS-3:E-1 (No Bars)
(Scale = 1"=4'-0")

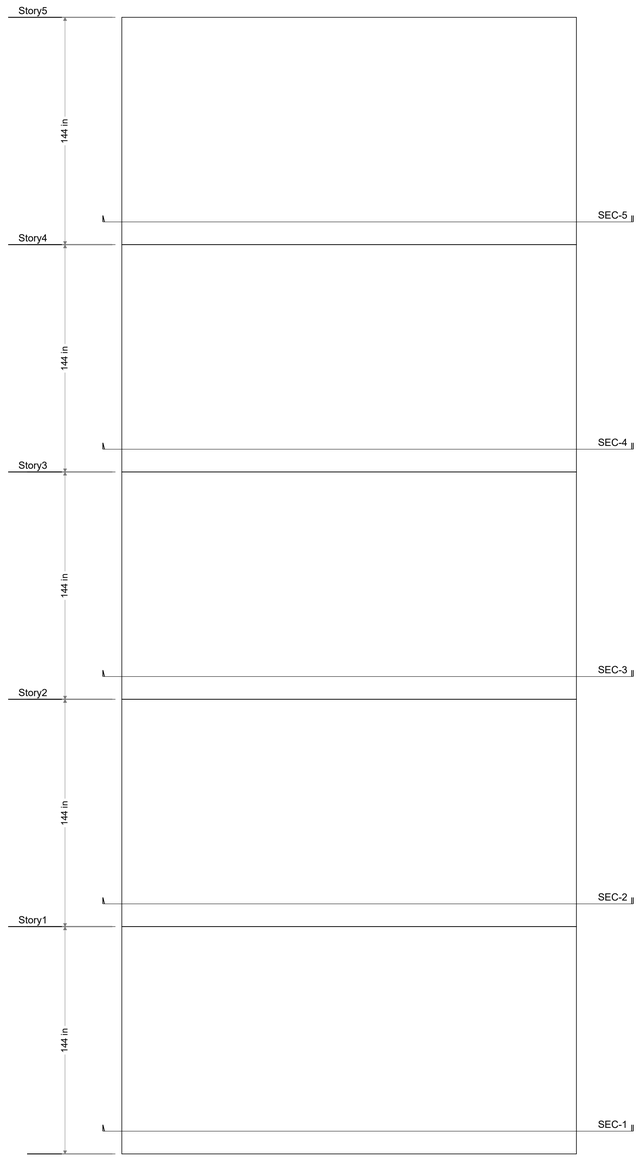

WS-3:E-2 (No Bars)
(Scale = 1"=4'-0")

WS-3-BOQ Summary

Sr. No.	Item	Quantity	Unit
1	Longitudinal Bars	4.57	ton
2	Ties and Stirrups	4.28	ton
3	Total Rebars	8.85	ton

WS-3-Rebar Weight Summary

Sr. No.	Size	Area (in²)	Length (ft)	Weight (ton)
1	#4	0.2	12,567.33	4.28
2	#6	0.44	6,105.83	4.57

www.csiamerica.com


No	Description	Date

WS-3:E-1 (No Bars)


Project Number	
Date	
Drawn By	
Checked By	

S-29

Scale

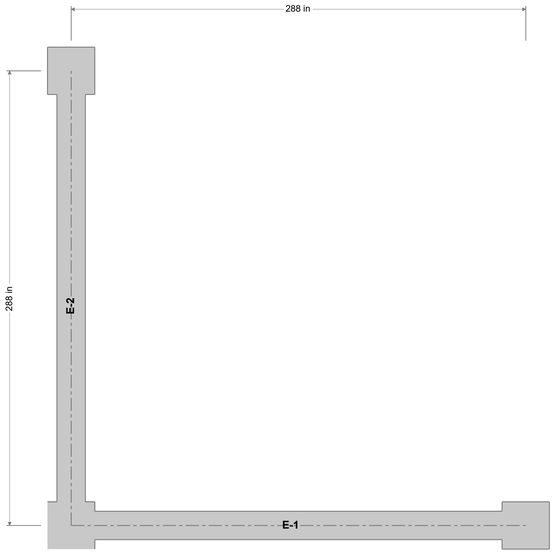

WS-4:Base Plan
(Scale = 1"=4'-0")

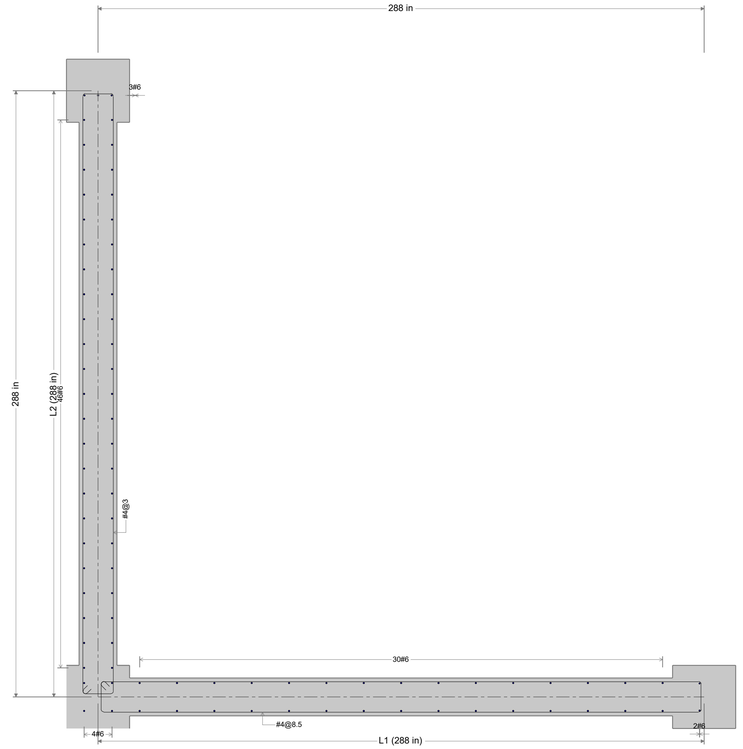

WS-4:Section-Story1
(Scale = 1"=3'-0")

www.csiamerica.com


No	Description	Date

WS-4:Base Plan


Project Number	
Date	
Drawn By	
Checked By	

S-30

Scale

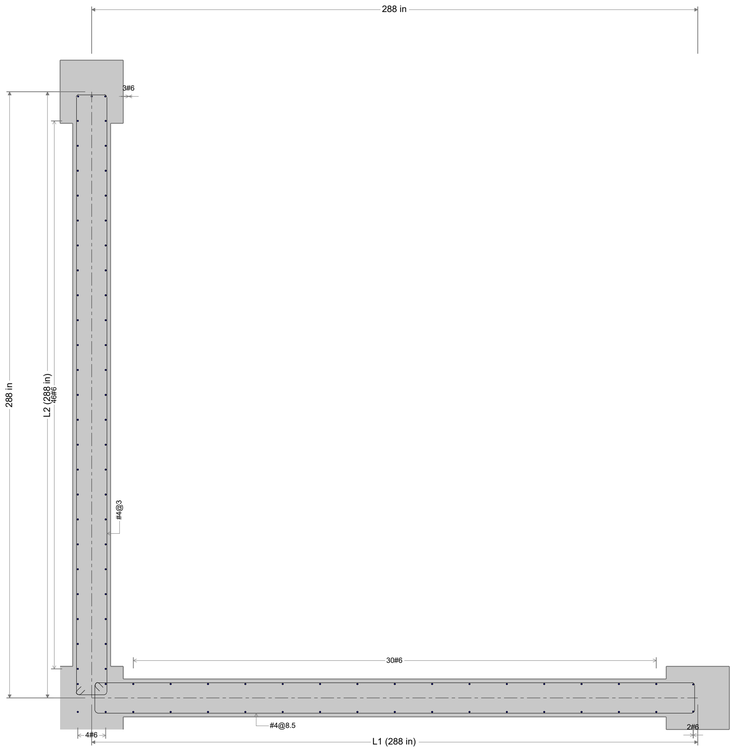

WS-4:Section-Story2
(Scale = 1"=3'-0")

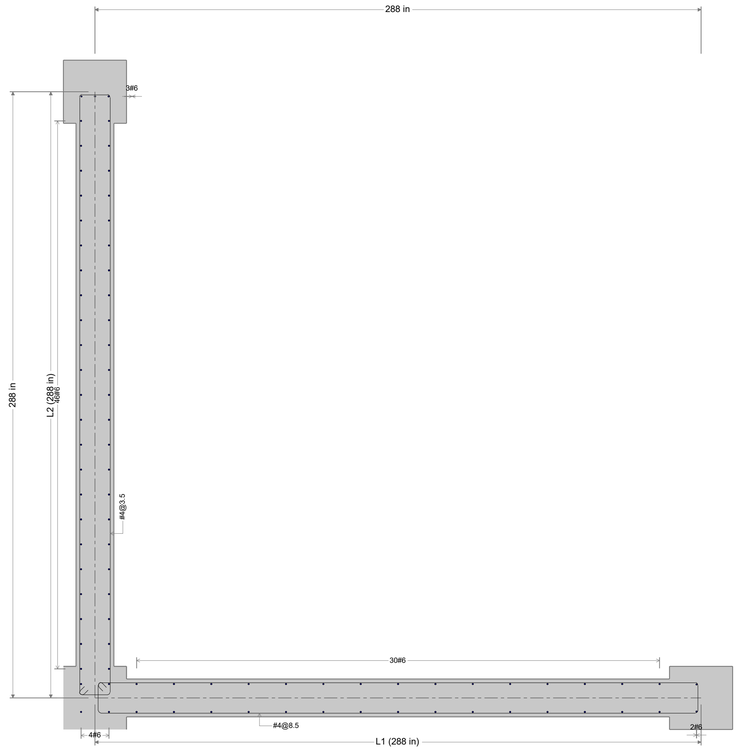

WS-4:Section-Story3
(Scale = 1"=3'-0")

www.csiamerica.com


No	Description	Date

WS-4:Section-Story2


Project Number	
Date	
Drawn By	
Checked By	

S-31

Scale	

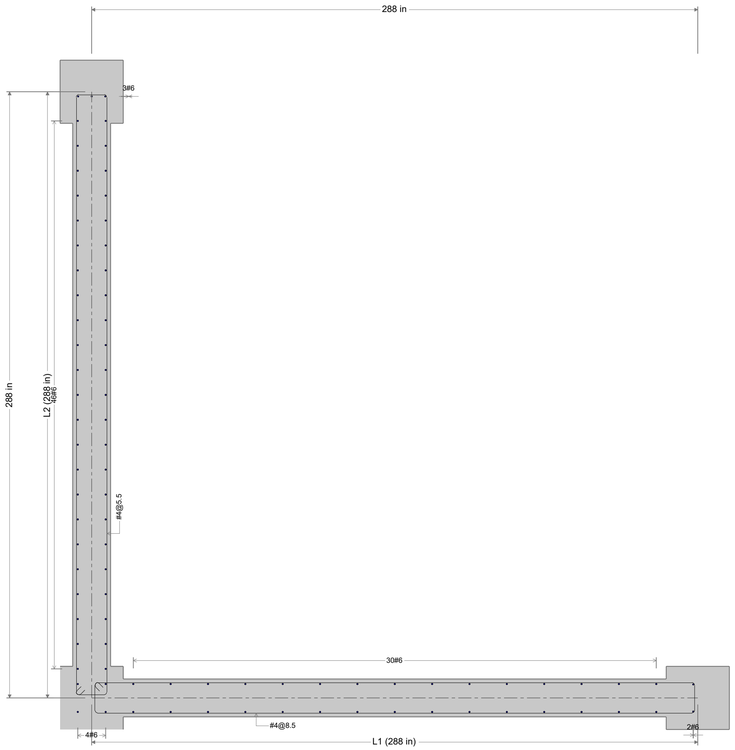

WS-4:Section-Story4
(Scale = 1"=3'-0")

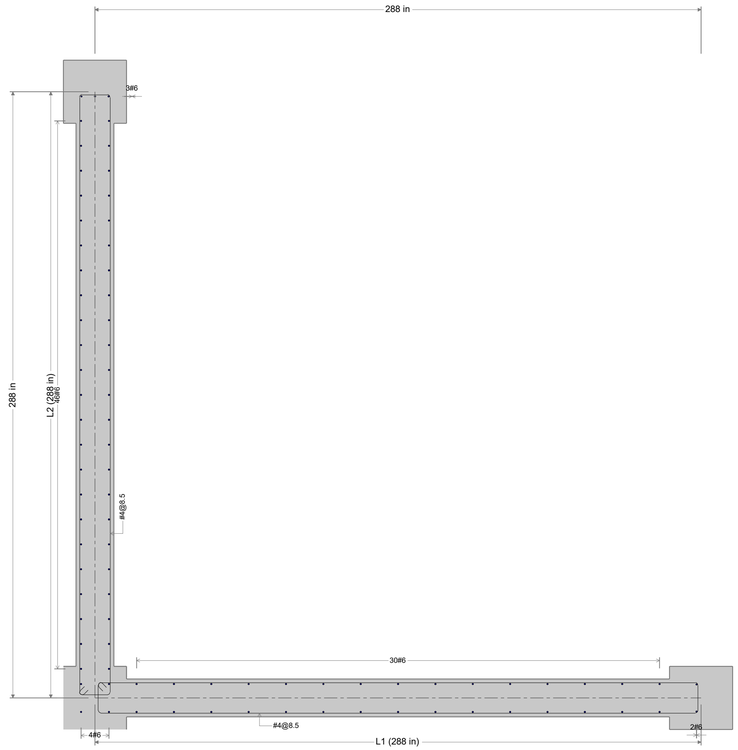

WS-4:Section-Story5
(Scale = 1"=3'-0")

www.csiamerica.com


No	Description	Date

WS-4:Section-Story4


Project Number	
Date	
Drawn By	
Checked By	

S-32

Scale	

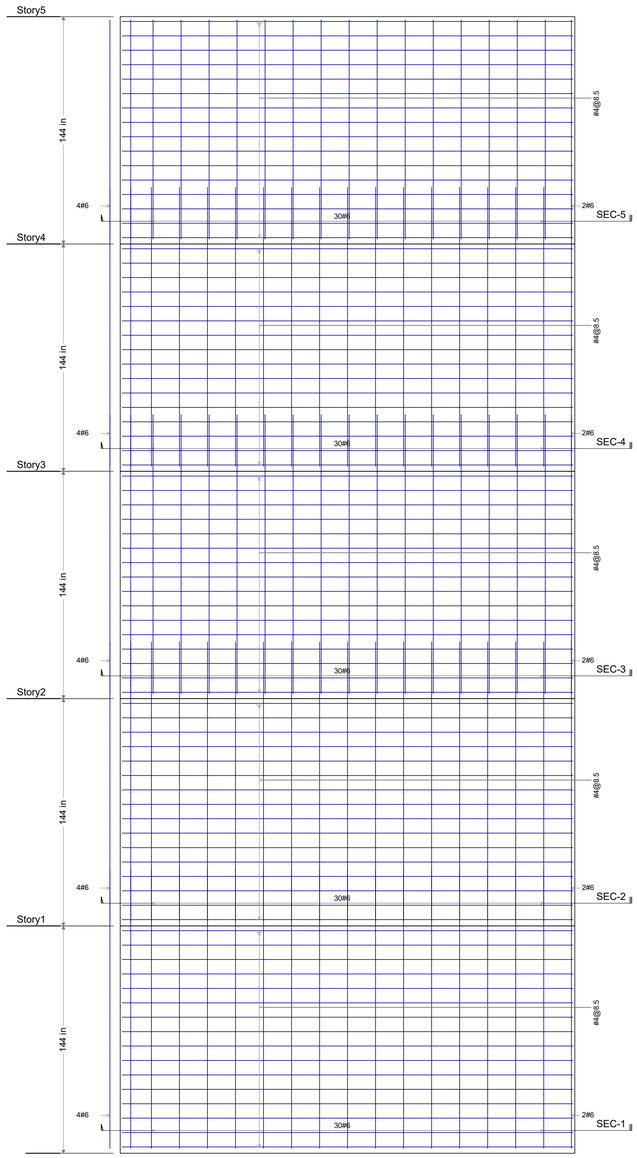

WS-4:E-1
(Scale = 1"=4'-0")

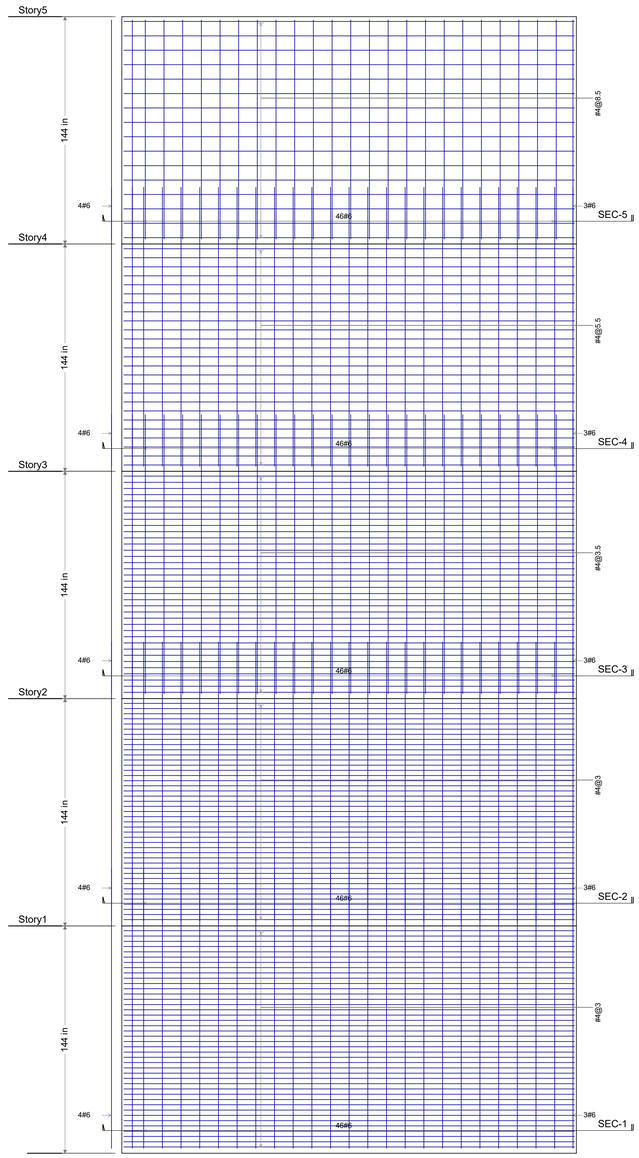

WS-4:E-2
(Scale = 1"=4'-0")

www.csiamerica.com


No	Description	Date

WS-4:E-1


Project Number	
Date	
Drawn By	
Checked By	

S-33

Scale

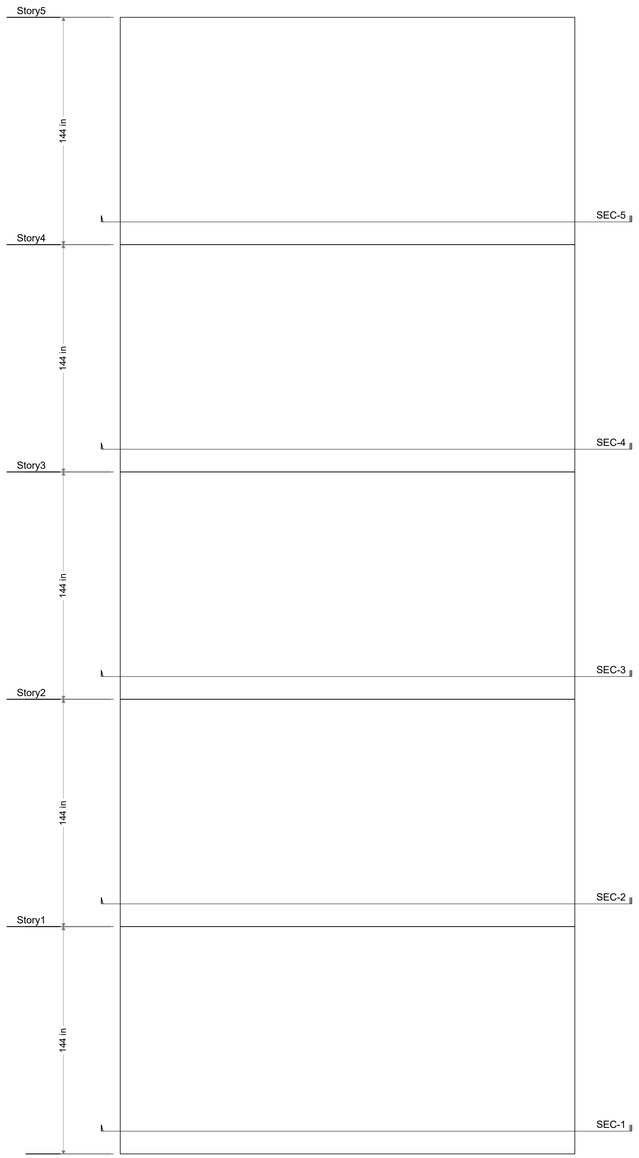

WS-4:E-1 (No Bars)
(Scale = 1"=4'-0")

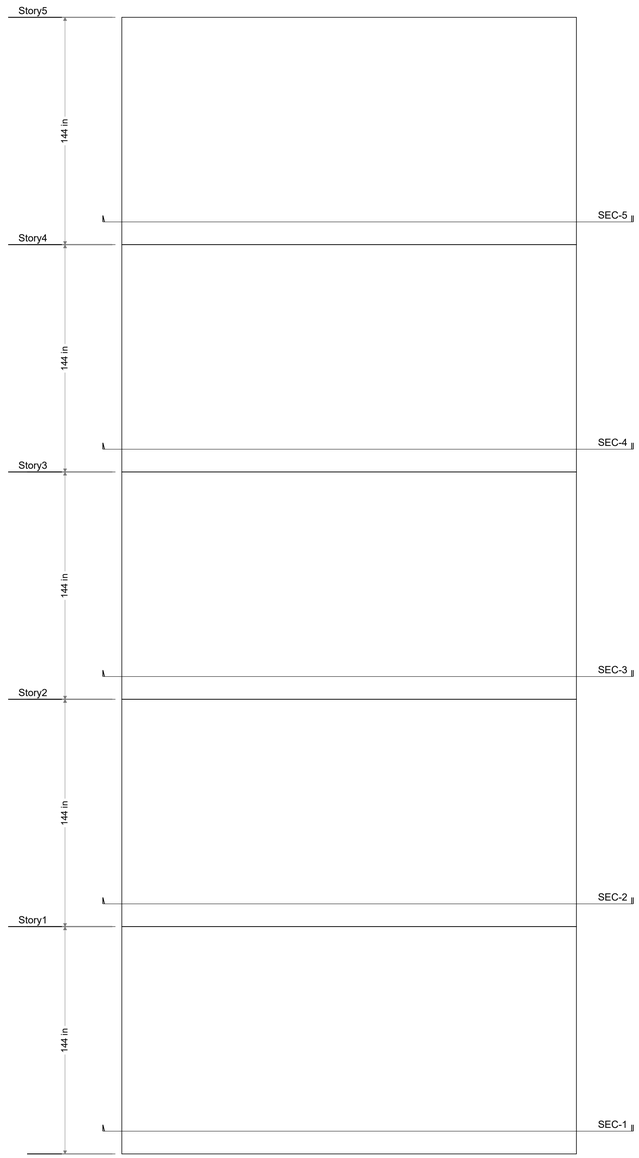

WS-4:E-2 (No Bars)
(Scale = 1"=4'-0")

WS-4-BOQ Summary

Sr. No.	Item	Quantity	Unit
1	Longitudinal Bars	4.57	ton
2	Ties and Stirrups	4.28	ton
3	Total Rebars	8.85	ton

WS-4-Rebar Weight Summary

Sr. No.	Size	Area (in²)	Length (ft)	Weight (ton)
1	#4	0.2	12,567.33	4.28
2	#6	0.44	6,105.83	4.57

www.csiamerica.com


No	Description	Date

WS-4:E-1 (No Bars)

Project Number	
Date	
Drawn By	
Checked By	

S-34

Scale

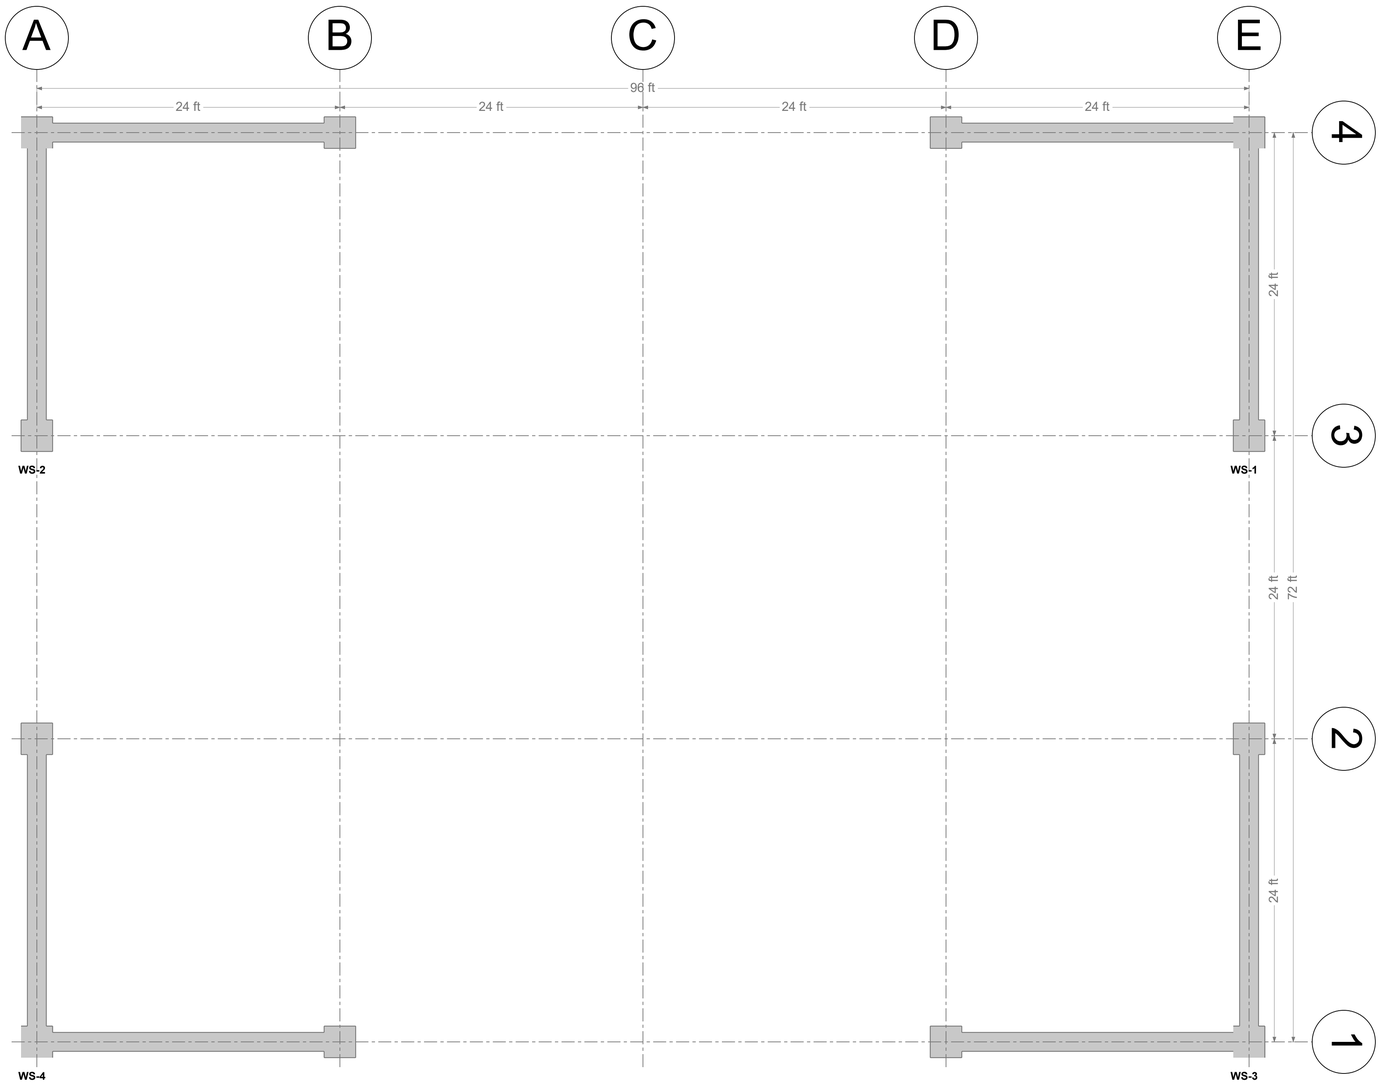

Layout Plan
(Scale = 1"=6'-0")

Wall Stacks-Rebar Weight Summary

Sr. No.	Size	Area (in²)	Length (ft)	Weight (ton)
1	#4	0.2	50,269.32	17.11
2	#6	0.44	24,423.33	18.28

Wall Stacks-BOQ Summary

Sr. No.	Item	Quantity	Unit
1	Longitudinal Bars	18.28	ton
2	Ties and Stirrups	17.11	ton
3	Total Rebars	35.39	ton

www.csiamerica.com


No	Description	Date

Layout Plan


Project Number	
Date	
Drawn By	
Checked By	

S-35


Scale

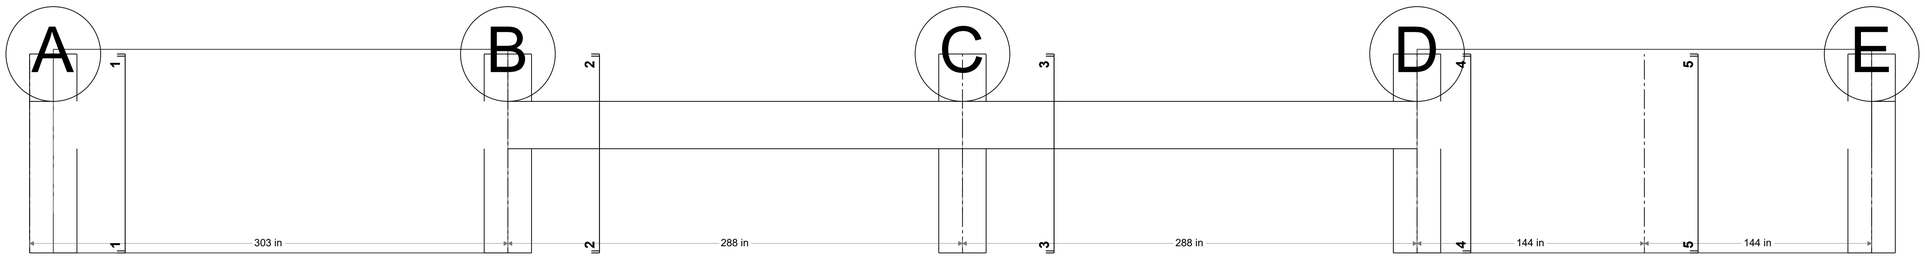

CB-1:Elevation (No bars)
(Scale = 1"=4'-0")

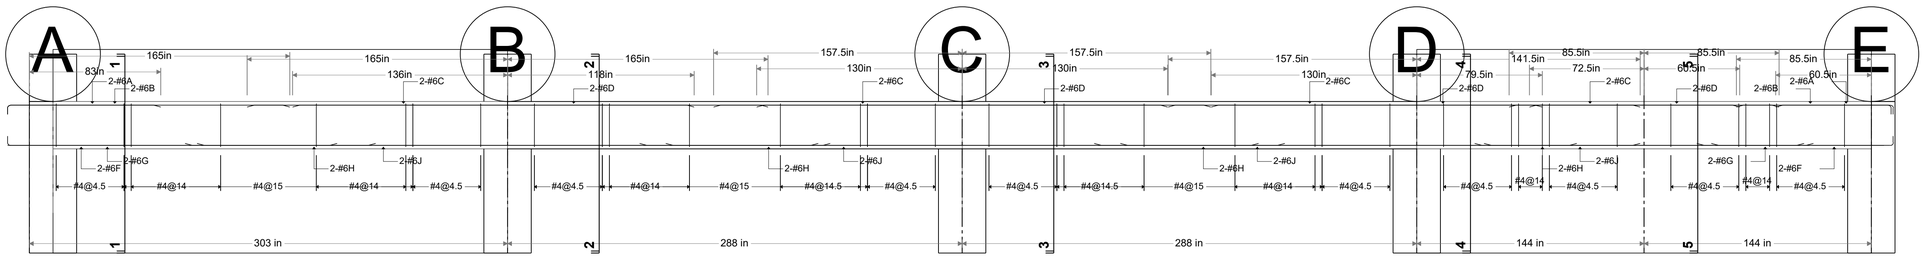

CB-1:Elevation
(Scale = 1"=4'-0")

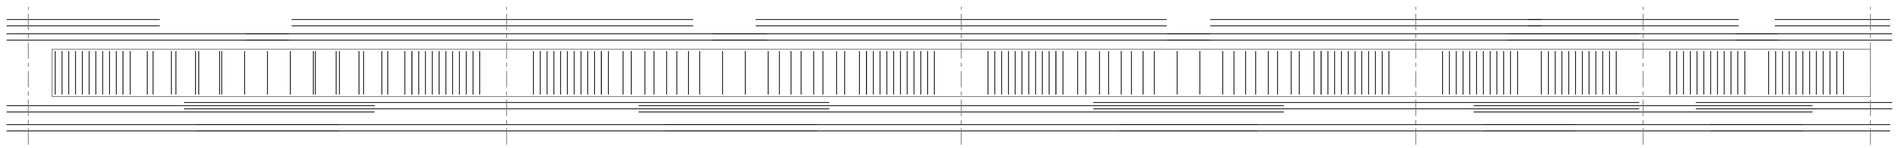

CB-1:Elevation-All Bars
(Scale = 1"=4'-0")

www.csiamerica.com


No	Description	Date

CB-1:Elevation (No bars)

Project Number	
Date	
Drawn By	
Checked By	


S-36

Scale

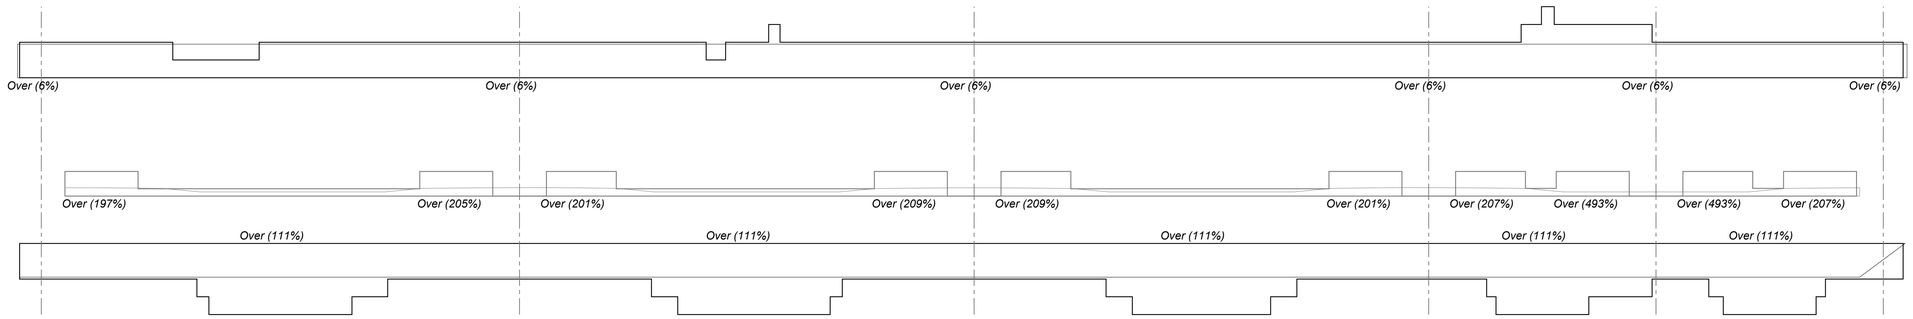


CB-1:Rebar Profiles

(Scale = 1"=4'-0")

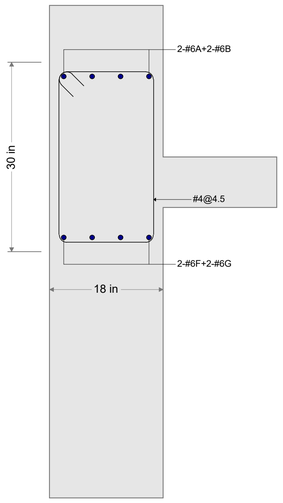


CB-1:Section-1

(Scale = 1"=1'-0")

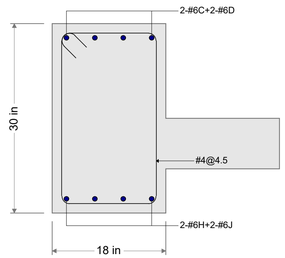


CB-1:Section-2

(Scale = 1"=1'-0")

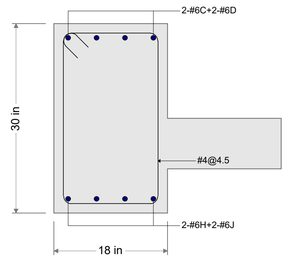


CB-1:Section-3

(Scale = 1"=1'-0")

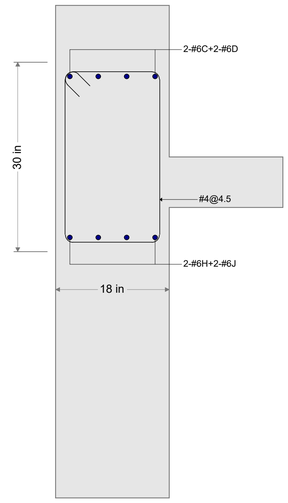

CB-1:Section-4

(Scale = 1"=1'-0")

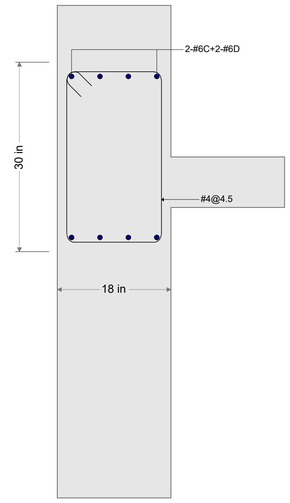

CB-1:Section-5

(Scale = 1"=1'-0")

www.csiamerica.com

No	Description	Date

CB-1:Rebar Profiles

Project Number	
Date	
Drawn By	
Checked By	

S-37

Scale

Story4:CB-1 - Rebar Table

Beam Label	Span/Support	Width	Depth	Bar A	Bar B	Bar C	Bar D	Bar E	Bar F	Bar G	Zone A	Zone B	Zone C	Zone D	Zone E	Elevation Type
CB-1	Support-1	-	-	2-#6A	2-#6B	-	-	-	-	-	-	-	-	-	-	Elevation 1
-	Span-1	18	30	-	-	-	-	-	-	-	#4@4.5	#4@14	#4@15	#4@14	#4@4.5	-
-	Support-2	-	-	-	-	2-#6C	2-#6D	-	-	-	-	-	-	-	-	-
-	Span-2	18	30	-	-	-	-	-	-	-	#4@4.5	#4@14	#4@15	#4@14.5	#4@4.5	-
-	Support-3	-	-	-	-	2-#6C	2-#6D	-	-	-	-	-	-	-	-	-
-	Span-3	18	30	-	-	-	-	-	-	-	#4@4.5	#4@14.5	#4@15	#4@14	#4@4.5	-
-	Support-4	-	-	-	-	2-#6C	2-#6D	-	-	-	-	-	-	-	-	-
-	Span-4	18	30	-	-	-	-	-	-	-	#4@4.5	-	#4@14	-	#4@4.5	-
-	Support-5	-	-	-	-	2-#6C	2-#6D	-	-	-	-	-	-	-	-	-
-	Span-5	18	30	-	-	-	-	-	-	-	#4@4.5	-	#4@14	-	#4@4.5	-
-	Support-6	-	-	2-#6A	2-#6B	-	-	-	-	-	-	-	-	-	-	-

Story4:CB-1-BOQ Summary

Sr. No.	Item	Quantity	Unit
1	Longitudinal Bars	0.72	ton
2	Ties and Stirrups	0.48	ton
3	Total Rebars	1.19	ton
4	Total Beam Length	96	ft
5	Total Beam Volume	360	cu ft
6	Weight/Volume	6.62	lb/cu ft
Note	Does not include weight of Typical Bars		

Story4:CB-1-Rebar Weight Summary

Sr. No.	Size	Area (in²)	Length (ft)	Weight (ton)
1	#4	0.2	1,397.52	0.48
2	#6	0.44	957.02	0.72
Note	Does not include Typical Bars			

www.csiamerica.com


No	Description	Date

CB-1:Beam Table

Project Number	
Date	
Drawn By	
Checked By	

S-38

Scale

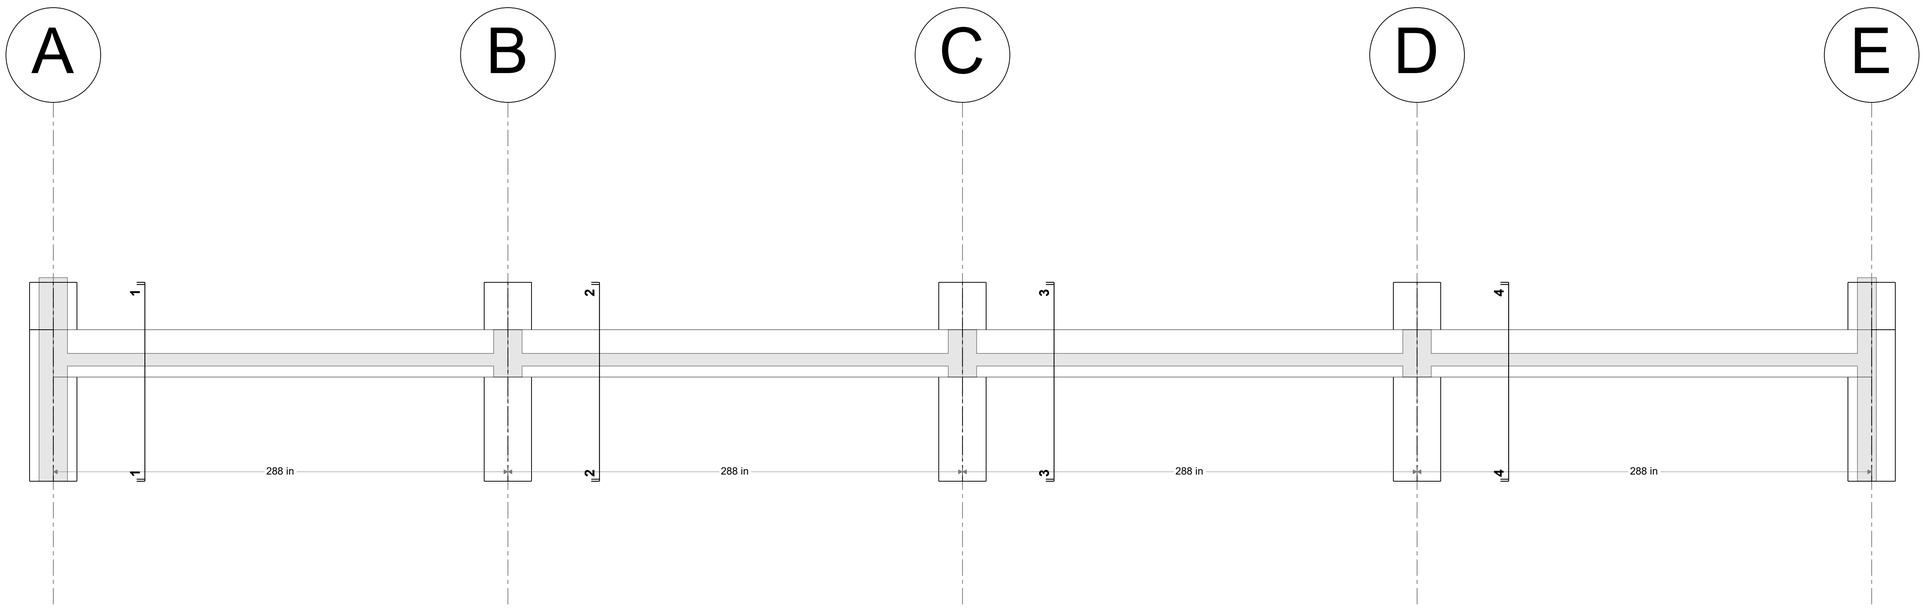

CB-2:Elevation (No bars)
(Scale = 1''=4'-0'')

www.csiamerica.com


No	Description	Date

CB-2:Elevation (No bars)


Project Number	
Date	
Drawn By	
Checked By	

S-39

Scale

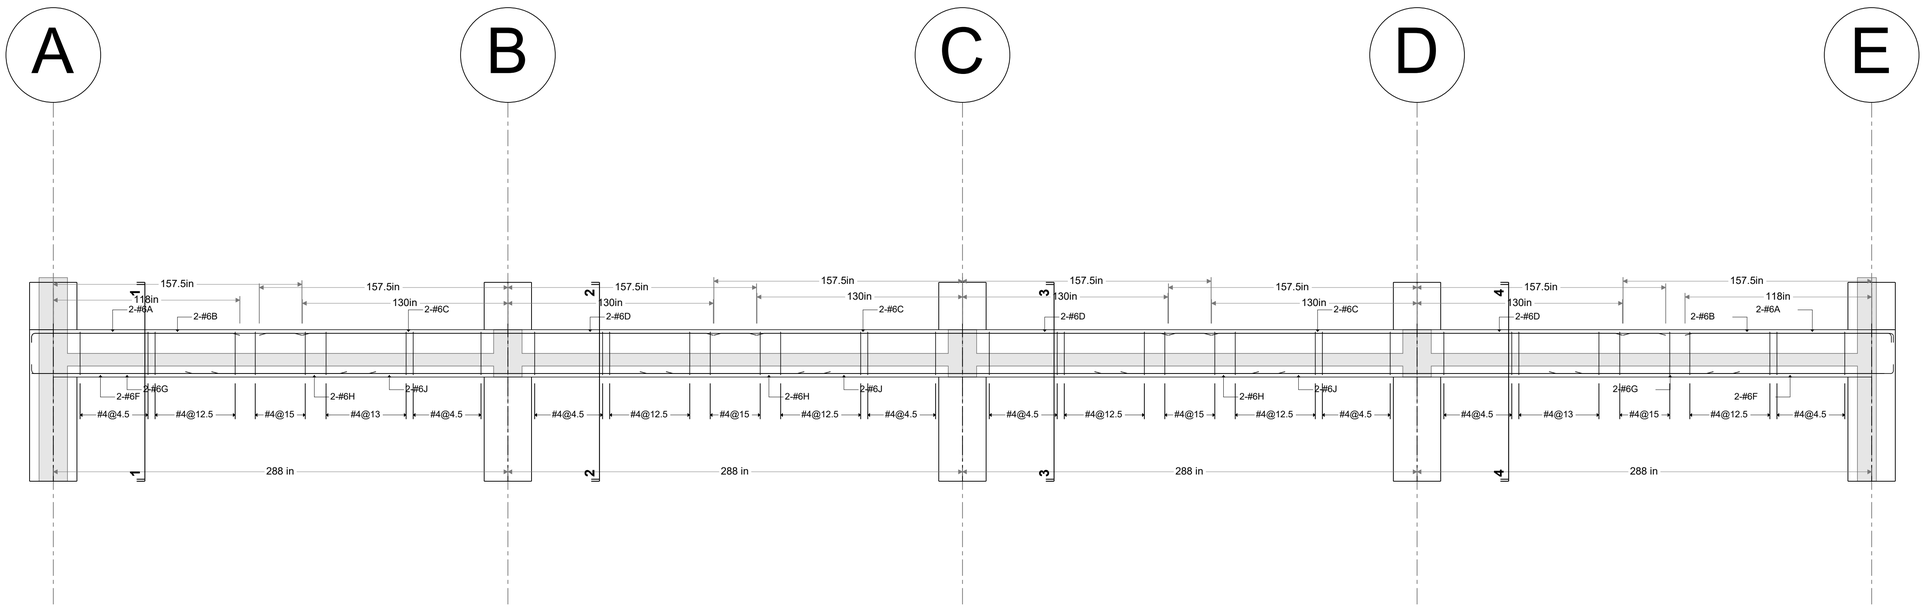

CB-2:Elevation
(Scale = 1"=4'-0")

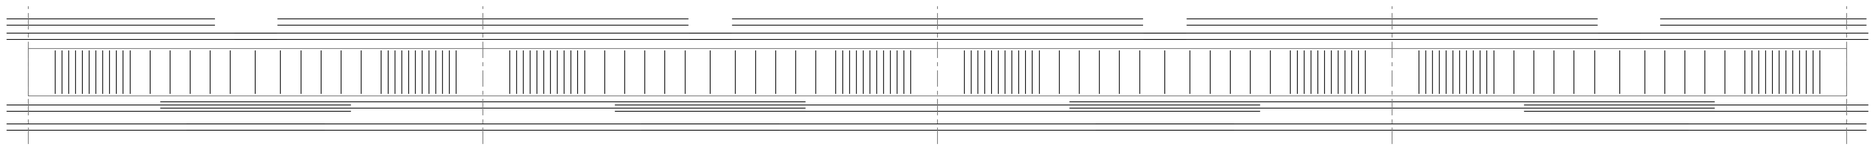

CB-2:Elevation-All Bars
(Scale = 1"=4'-0")

www.csiamerica.com


No	Description	Date

CB-2:Elevation


Project Number	
Date	
Drawn By	
Checked By	

S-40


Scale	

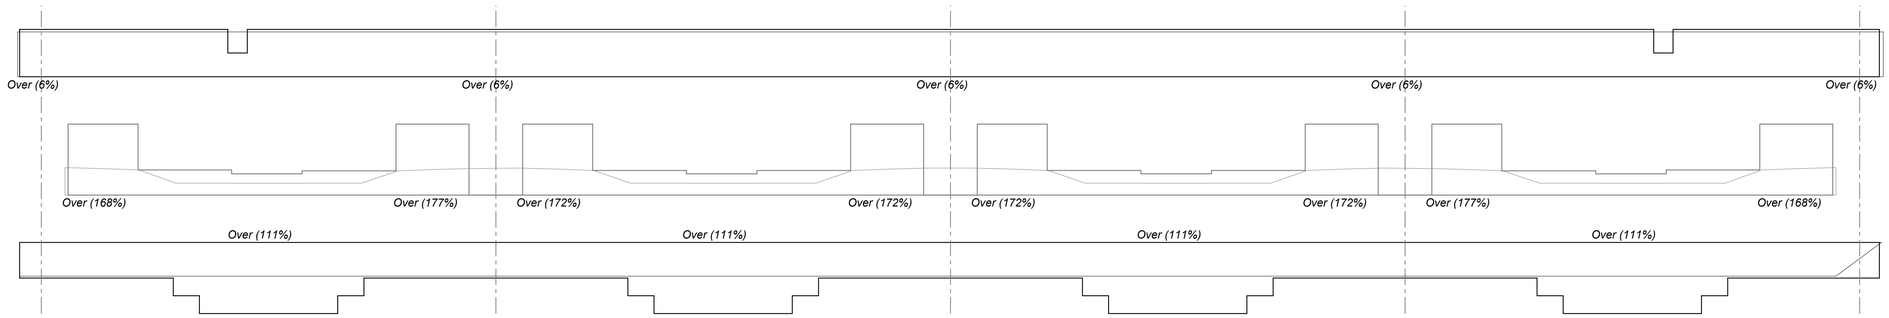


CB-2:Rebar Profiles
(Scale = 1"=4'-0")

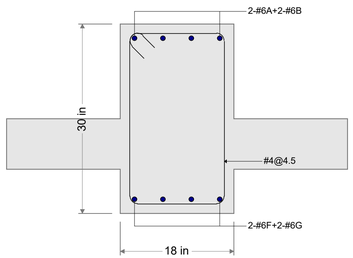


CB-2:Section-1
(Scale = 1"=1'-0")

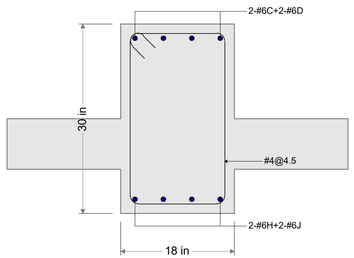

CB-2:Section-2
(Scale = 1"=1'-0")

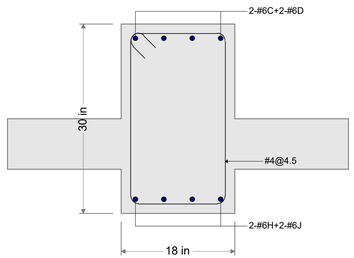

CB-2:Section-3
(Scale = 1"=1'-0")

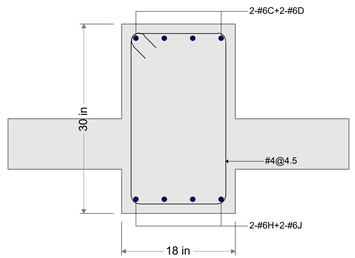

CB-2:Section-4
(Scale = 1"=1'-0")

Story4:CB-2 - Rebar Table

Beam Label	Span/Support	Width	Depth	Bar A	Bar B	Bar C	Bar D	Bar E	Bar F	Bar G	Zone A	Zone B	Zone C	Zone D	Zone E	Elevation Type
CB-2	Support-1	-	-	2-#6A	2-#6B	-	-	-	-	-	-	-	-	-	-	Elevation 1
-	Span-1	18	30	-	-	-	-	-	-	-	#4@4.5	#4@12.5	#4@15	#4@13	#4@4.5	-
-	Support-2	-	-	-	-	2-#6C	2-#6D	-	-	-	-	-	-	-	-	-
-	Span-2	18	30	-	-	-	-	-	-	-	#4@4.5	#4@12.5	#4@15	#4@12.5	#4@4.5	-
-	Support-3	-	-	-	-	2-#6C	2-#6D	-	-	-	-	-	-	-	-	-
-	Span-3	18	30	-	-	-	-	-	-	-	#4@4.5	#4@12.5	#4@15	#4@12.5	#4@4.5	-
-	Support-4	-	-	-	-	2-#6C	2-#6D	-	-	-	-	-	-	-	-	-
-	Span-4	18	30	-	-	-	-	-	-	-	#4@4.5	#4@13	#4@15	#4@12.5	#4@4.5	-
-	Support-5	-	-	2-#6A	2-#6B	-	-	-	-	-	-	-	-	-	-	-

www.csiamerica.com

No	Description	Date

CB-2:Rebar Profiles

Project Number	
Date	
Drawn By	
Checked By	

S-41


Scale

Story4:CB-2-BOQ Summary


Sr. No.	Item	Quantity	Unit
1	Longitudinal Bars	0.69	ton
2	Ties and Stirrups	0.37	ton
3	Total Rebars	1.06	ton
4	Total Beam Length	96	ft
5	Total Beam Volume	360	cu ft
6	Weight/Volume	5.88	lb/cu ft
Note	Does not include weight of Typical Bars		

Story4:CB-2-Rebar Weight Summary

Sr. No.	Size	Area (in²)	Length (ft)	Weight (ton)
1	#4	0.2	1,087.8	0.37
2	#6	0.44	920.46	0.69
Note	Does not include Typical Bars			

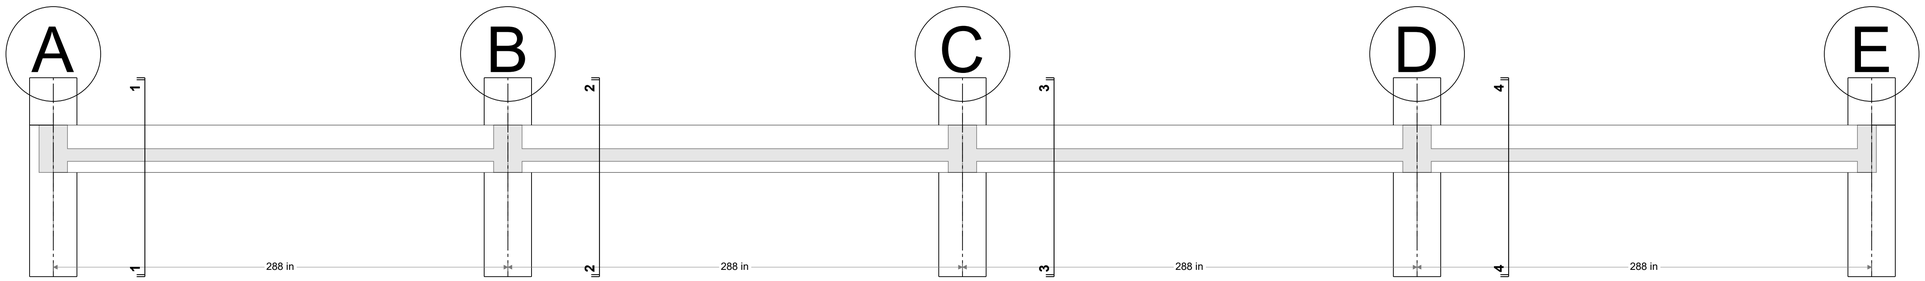

CB-3:Elevation (No bars)
(Scale = 1"=4'-0")

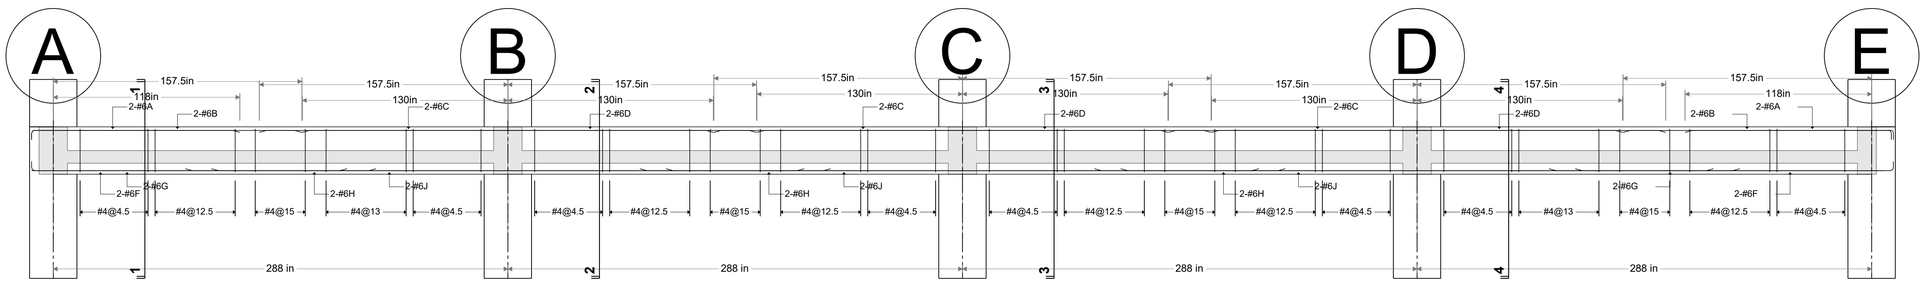

CB-3:Elevation
(Scale = 1"=4'-0")

www.csiamerica.com


No	Description	Date

CB-2:BOQ


Project Number	
Date	
Drawn By	
Checked By	

S-42


Scale

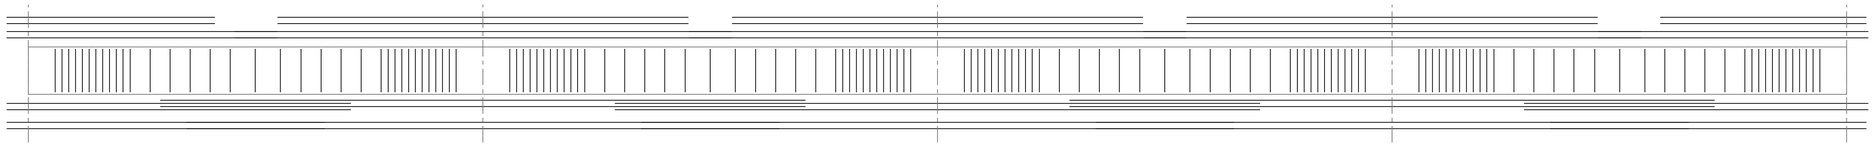


CB-3:Elevation-All Bars
(Scale = 1"=4'-0")

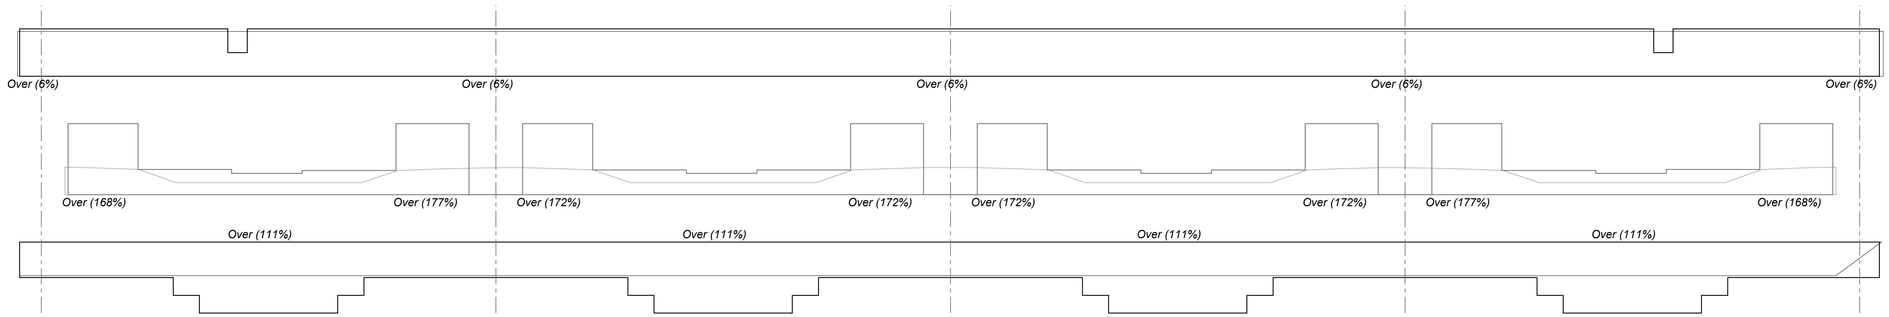


CB-3:Rebar Profiles
(Scale = 1"=4'-0")

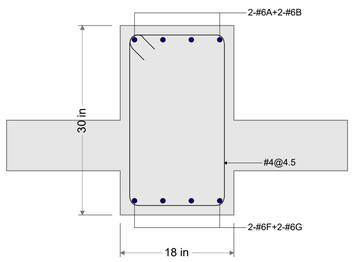


CB-3:Section-1
(Scale = 1"=1'-0")

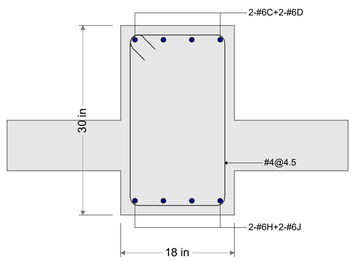

CB-3:Section-2
(Scale = 1"=1'-0")

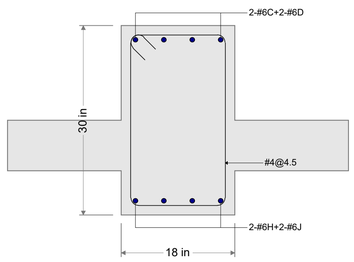

CB-3:Section-3
(Scale = 1"=1'-0")

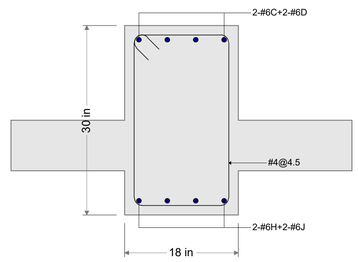

CB-3:Section-4
(Scale = 1"=1'-0")

www.csiamerica.com

No	Description	Date

CB-3:Elevation-All Bars

Project Number	
Date	
Drawn By	
Checked By	

S-43

Scale

Story4:CB-3 - Rebar Table

Beam Label	Span/Support	Width	Depth	Bar A	Bar B	Bar C	Bar D	Bar E	Bar F	Bar G	Zone A	Zone B	Zone C	Zone D	Zone E	Elevation Type
CB-3	Support-1	-	-	2-#6A	2-#6B	-	-	-	-	-	-	-	-	-	-	Elevation 1
-	Span-1	18	30	-	-	-	-	-	-	-	#4@4.5	#4@12.5	#4@15	#4@13	#4@4.5	-
-	Support-2	-	-	-	-	2-#6C	2-#6D	-	-	-	-	-	-	-	-	-
-	Span-2	18	30	-	-	-	-	-	-	-	#4@4.5	#4@12.5	#4@15	#4@12.5	#4@4.5	-
-	Support-3	-	-	-	-	2-#6C	2-#6D	-	-	-	-	-	-	-	-	-
-	Span-3	18	30	-	-	-	-	-	-	-	#4@4.5	#4@12.5	#4@15	#4@12.5	#4@4.5	-
-	Support-4	-	-	-	-	2-#6C	2-#6D	-	-	-	-	-	-	-	-	-
-	Span-4	18	30	-	-	-	-	-	-	-	#4@4.5	#4@13	#4@15	#4@12.5	#4@4.5	-
-	Support-5	-	-	2-#6A	2-#6B	-	-	-	-	-	-	-	-	-	-	-

Story4:CB-3-BOQ Summary

Sr. No.	Item	Quantity	Unit
1	Longitudinal Bars	0.69	ton
2	Ties and Stirrups	0.37	ton
3	Total Rebars	1.06	ton
4	Total Beam Length	96	ft
5	Total Beam Volume	360	cu ft
6	Weight/Volume	5.88	lb/cu ft
Note	Does not include weight of Typical Bars		

Story4:CB-3-Rebar Weight Summary

Sr. No.	Size	Area (in²)	Length (ft)	Weight (ton)
1	#4	0.2	1,087.8	0.37
2	#6	0.44	920.46	0.69
Note	Does not include Typical Bars			

www.csiamerica.com


No	Description	Date

CB-3:Beam Table

Project Number	
Date	
Drawn By	
Checked By	

S-44

Scale

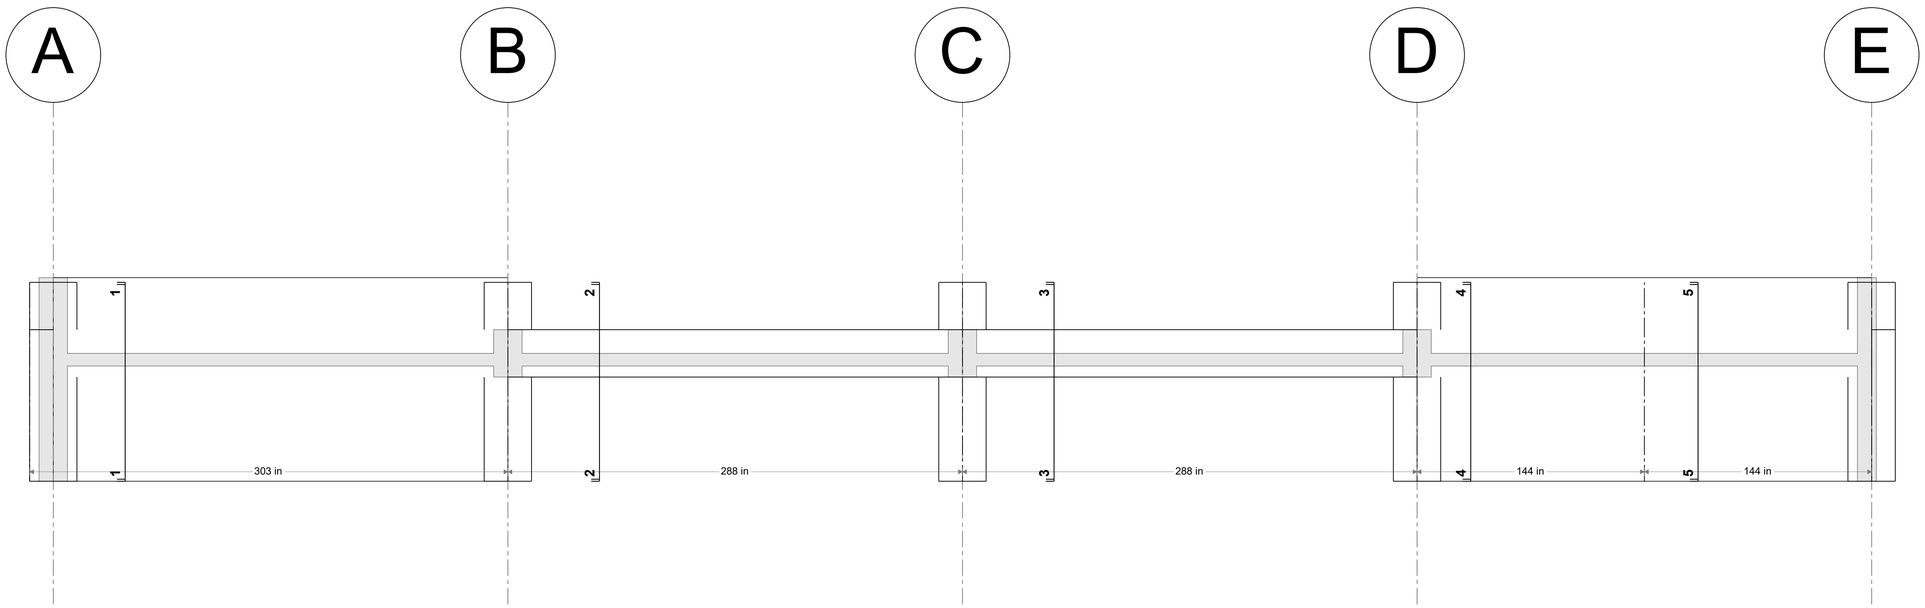

CB-4:Elevation (No bars)
(Scale = 1''=4'-0'')

www.csiamerica.com


No	Description	Date

CB-4:Elevation (No bars)


Project Number	
Date	
Drawn By	
Checked By	

S-45

Scale

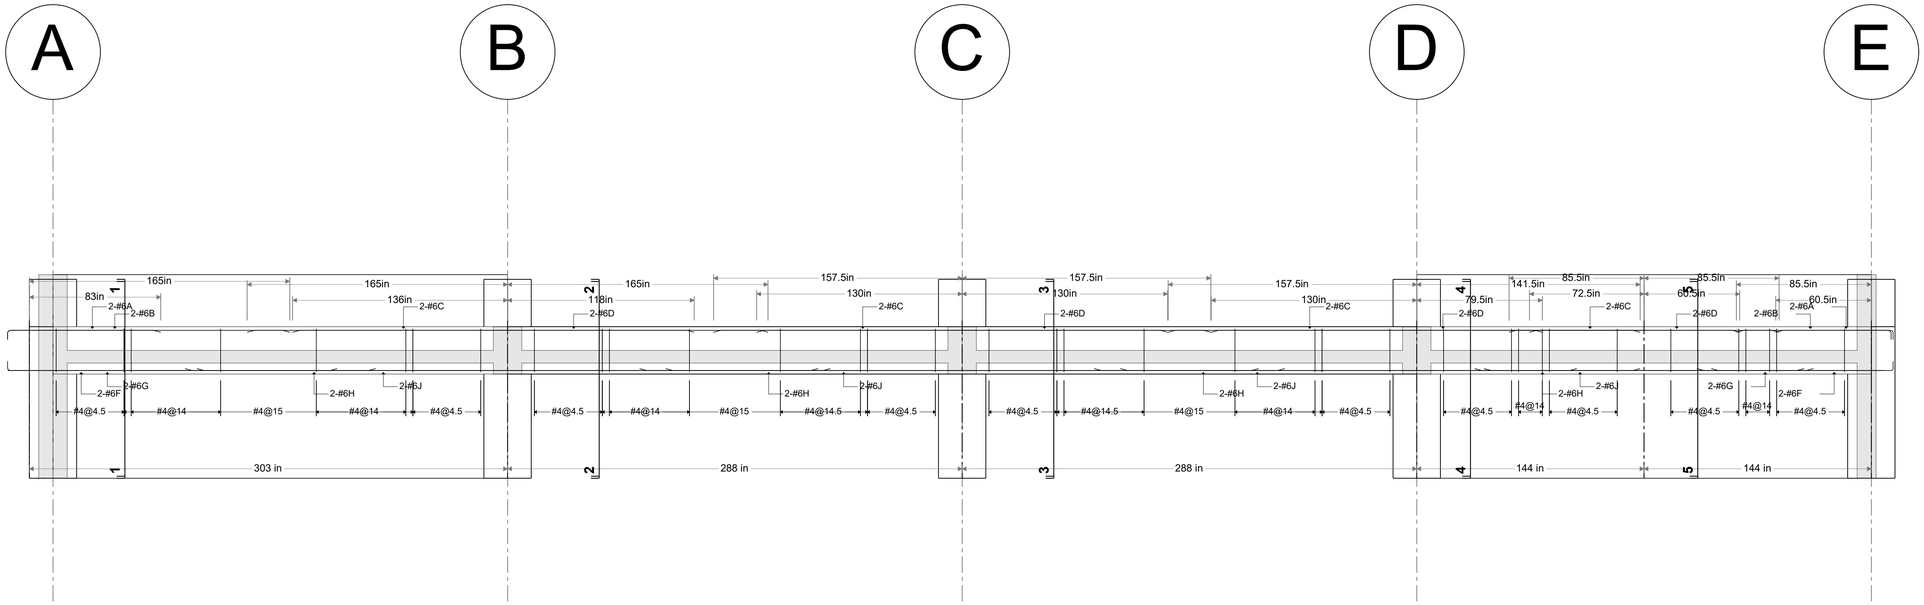

CB-4:Elevation
(Scale = 1"=4'-0")

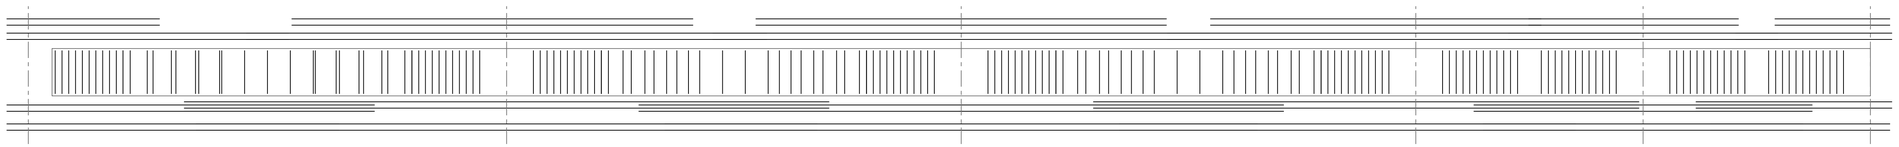

CB-4:Elevation-All Bars
(Scale = 1"=4'-0")

www.csiamerica.com


No	Description	Date

CB-4:Elevation


Project Number	
Date	
Drawn By	
Checked By	

S-46

Scale

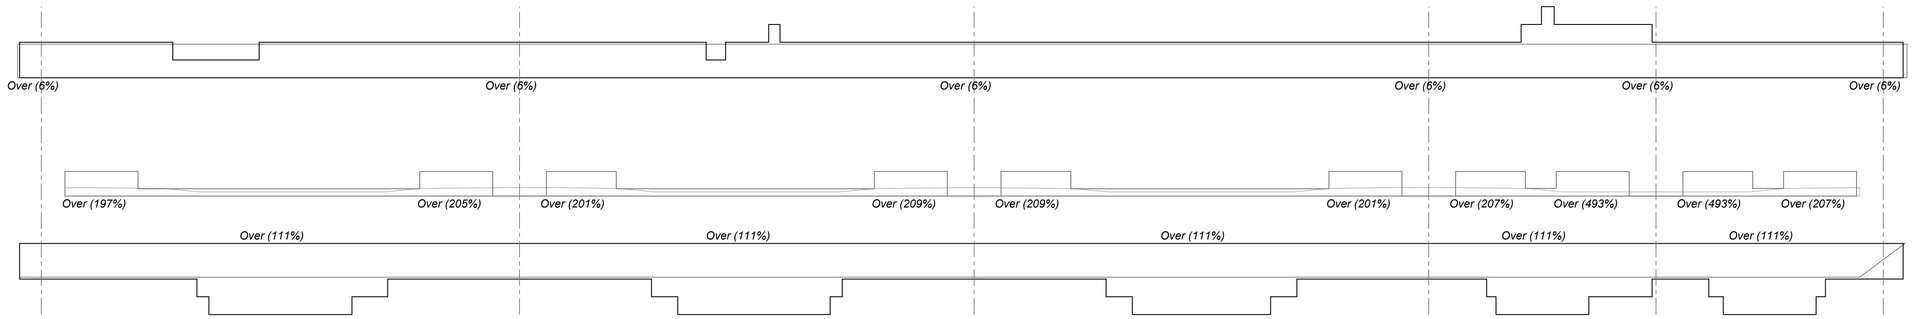


CB-4:Rebar Profiles
(Scale = 1"=4'-0")

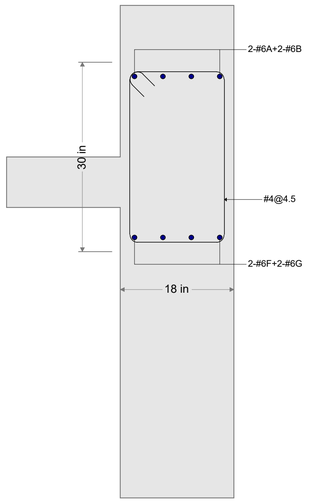


CB-4:Section-1
(Scale = 1"=1'-0")

CB-4:Section-2
(Scale = 1"=1'-0")

CB-4:Section-3
(Scale = 1"=1'-0")

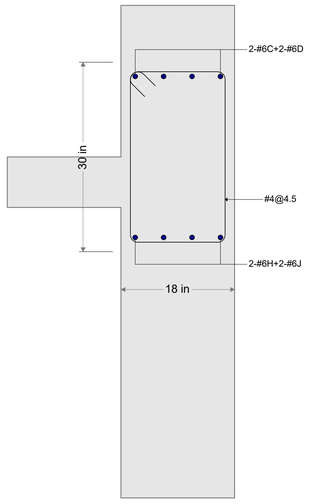

CB-4:Section-4
(Scale = 1"=1'-0")

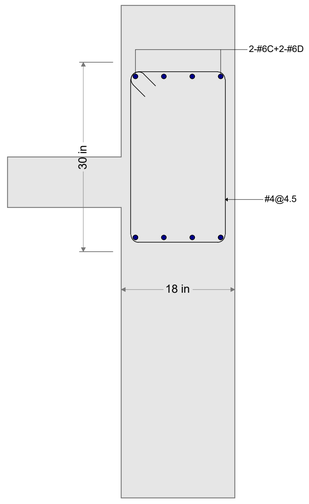

CB-4:Section-5
(Scale = 1"=1'-0")

www.csiamerica.com

No	Description	Date

CB-4:Rebar Profiles

Project Number	
Date	
Drawn By	
Checked By	

S-47

Scale

Story4:CB-4 - Rebar Table

Beam Label	Span/Support	Width	Depth	Bar A	Bar B	Bar C	Bar D	Bar E	Bar F	Bar G	Zone A	Zone B	Zone C	Zone D	Zone E	Elevation Type
CB-4	Support-1	-	-	2-#6A	2-#6B	-	-	-	-	-	-	-	-	-	-	Elevation 1
-	Span-1	18	30	-	-	-	-	-	-	-	#4@4.5	#4@14	#4@15	#4@14	#4@4.5	-
-	Support-2	-	-	-	-	2-#6C	2-#6D	-	-	-	-	-	-	-	-	-
-	Span-2	18	30	-	-	-	-	-	-	-	#4@4.5	#4@14	#4@15	#4@14.5	#4@4.5	-
-	Support-3	-	-	-	-	2-#6C	2-#6D	-	-	-	-	-	-	-	-	-
-	Span-3	18	30	-	-	-	-	-	-	-	#4@4.5	#4@14.5	#4@15	#4@14	#4@4.5	-
-	Support-4	-	-	-	-	2-#6C	2-#6D	-	-	-	-	-	-	-	-	-
-	Span-4	18	30	-	-	-	-	-	-	-	#4@4.5	-	#4@14	-	#4@4.5	-
-	Support-5	-	-	-	-	2-#6C	2-#6D	-	-	-	-	-	-	-	-	-
-	Span-5	18	30	-	-	-	-	-	-	-	#4@4.5	-	#4@14	-	#4@4.5	-
-	Support-6	-	-	2-#6A	2-#6B	-	-	-	-	-	-	-	-	-	-	-

Story4:CB-4-BOQ Summary

Sr. No.	Item	Quantity	Unit
1	Longitudinal Bars	0.72	ton
2	Ties and Stirrups	0.48	ton
3	Total Rebars	1.19	ton
4	Total Beam Length	96	ft
5	Total Beam Volume	360	cu ft
6	Weight/Volume	6.62	lb/cu ft
Note	Does not include weight of Typical Bars		

Story4:CB-4-Rebar Weight Summary

Sr. No.	Size	Area (in²)	Length (ft)	Weight (ton)
1	#4	0.2	1,397.52	0.48
2	#6	0.44	957.02	0.72
Note	Does not include Typical Bars			

www.csiamerica.com


No	Description	Date

CB-4:Beam Table

Project Number	
Date	
Drawn By	
Checked By	

S-48

Scale

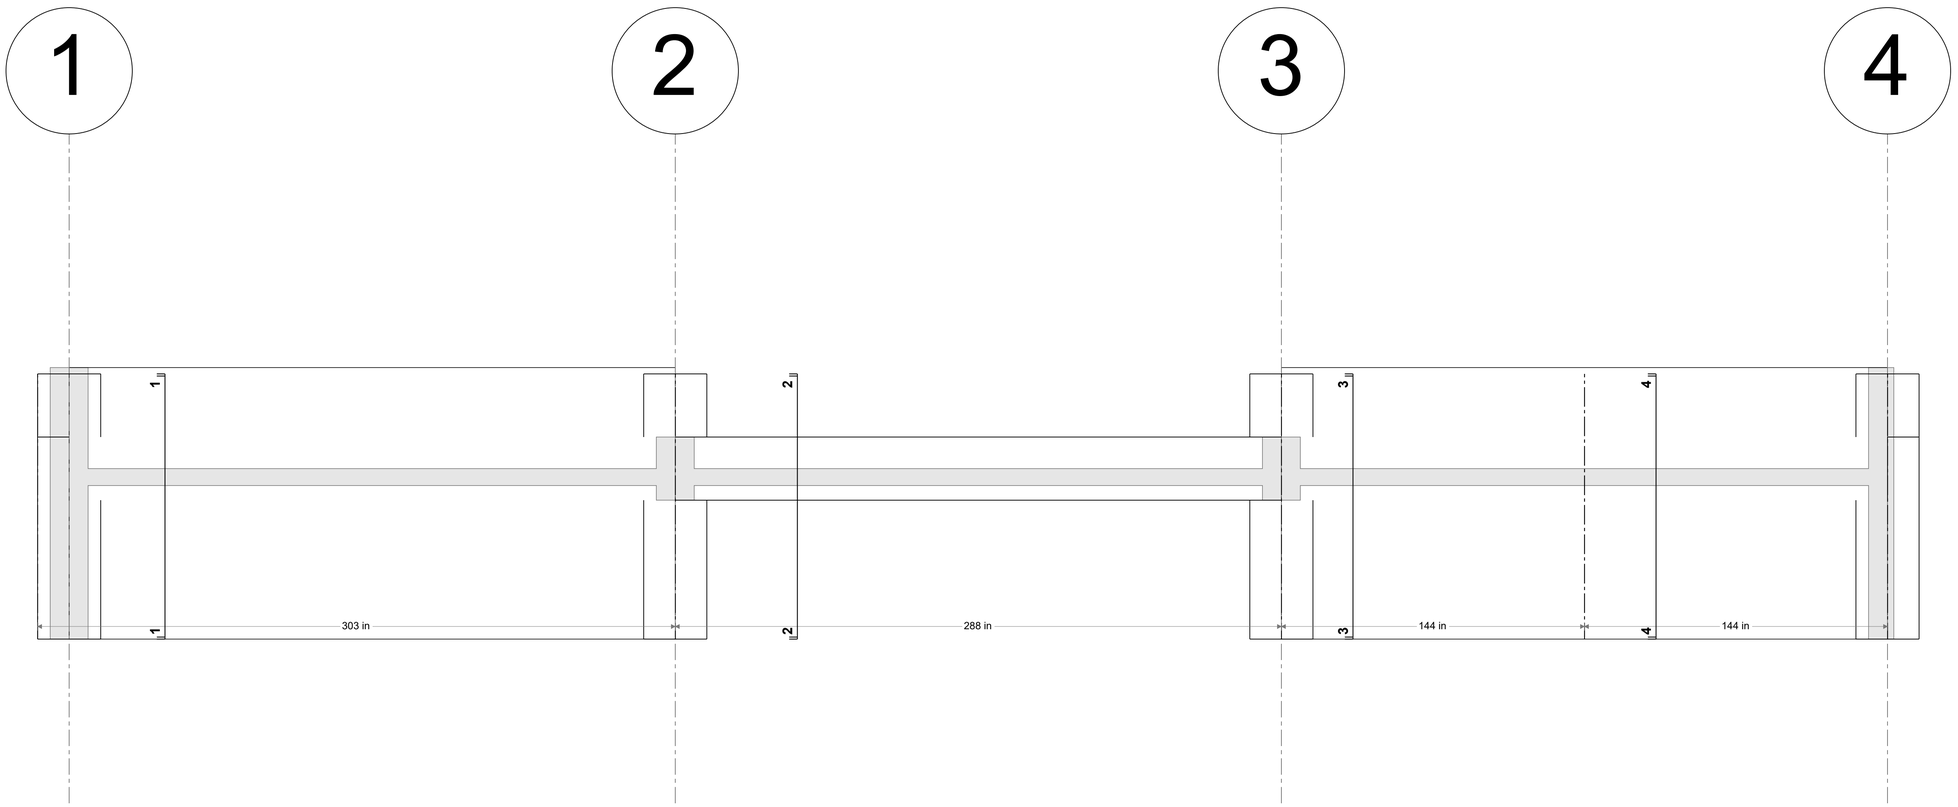

CB-5:Elevation (No bars)
(Scale = 1"=3'-0")

www.csiamerica.com


No	Description	Date

CB-5:Elevation (No bars)


Project Number	
Date	
Drawn By	
Checked By	

S-49

Scale

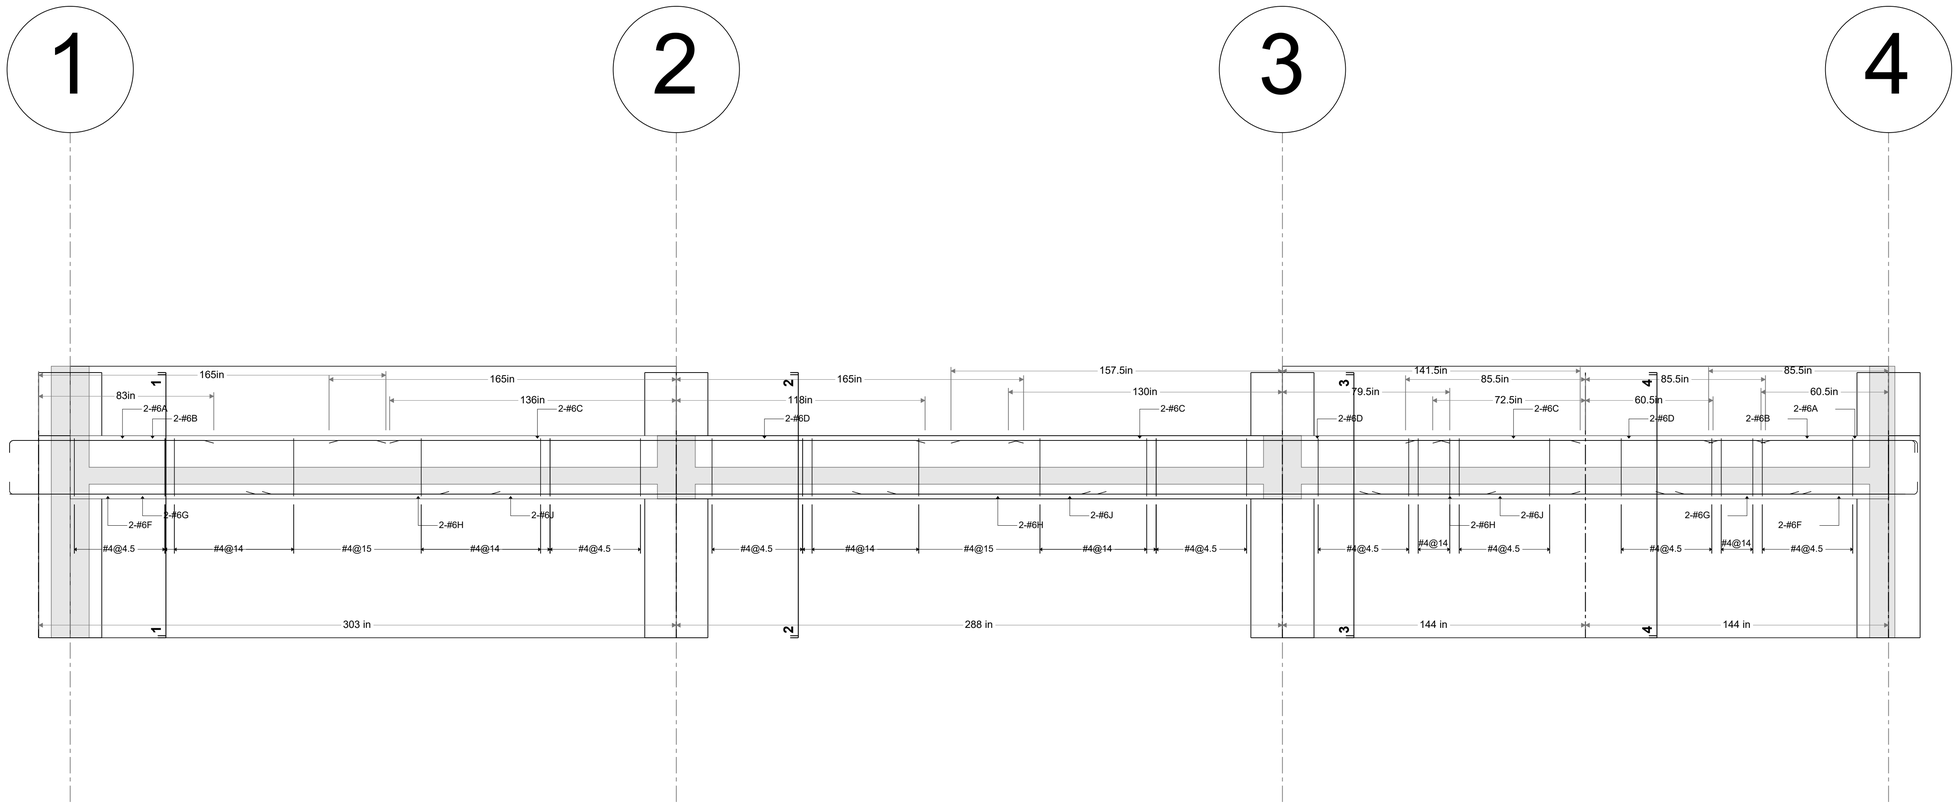

CB-5:Elevation
(Scale = 1"=3'-0")

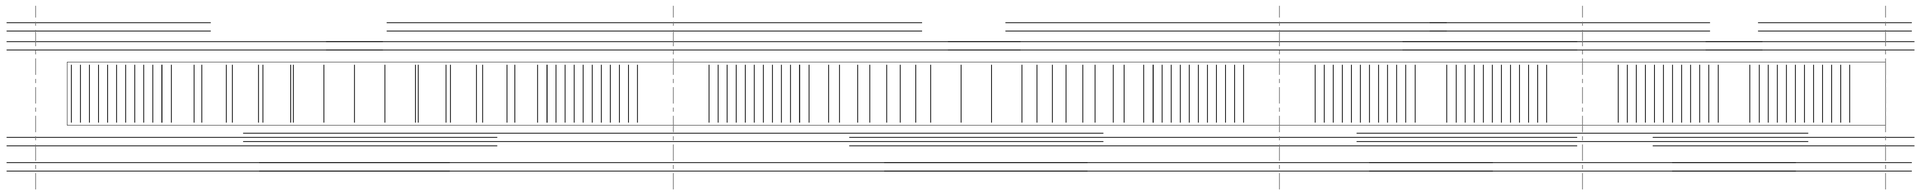

CB-5:Elevation-All Bars
(Scale = 1"=3'-0")

www.csiamerica.com


No	Description	Date

CB-5:Elevation


Project Number	
Date	
Drawn By	
Checked By	

S-50


Scale

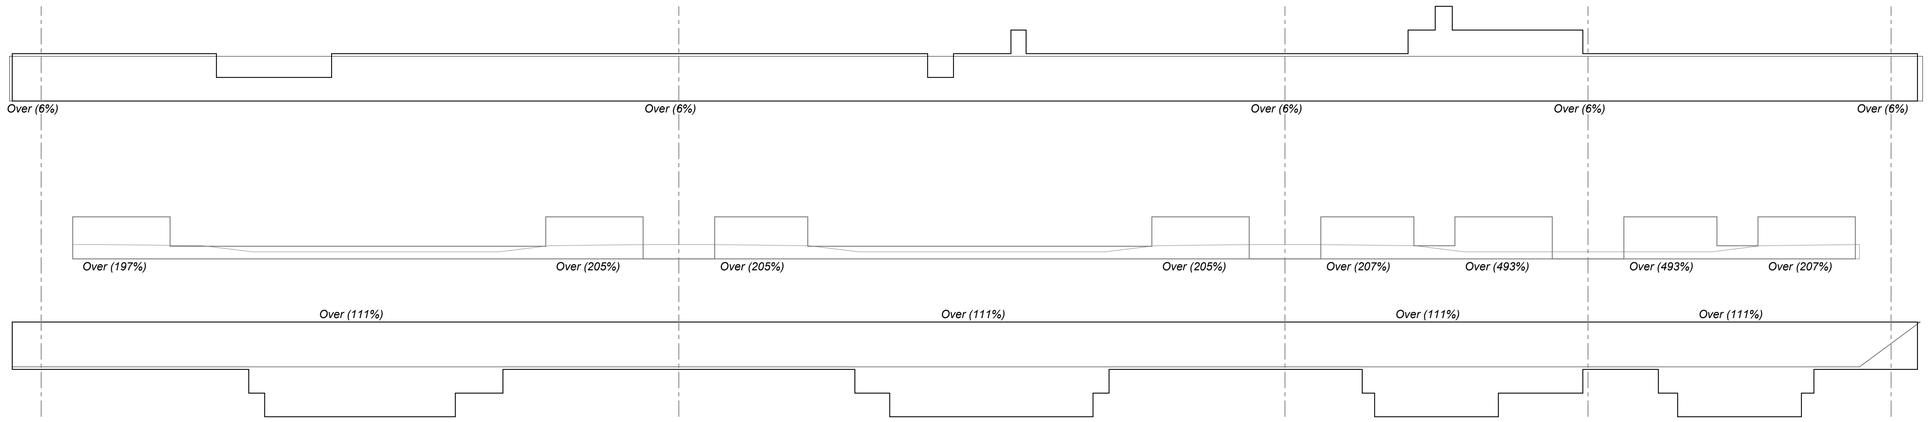


CB-5:Rebar Profiles
(Scale = 1"=3'-0")

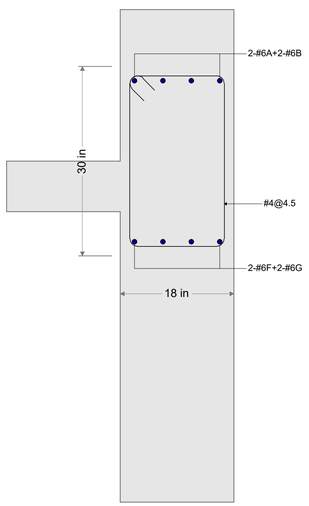


CB-5:Section-1
(Scale = 1"=1'-0")

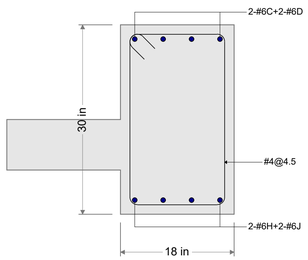

CB-5:Section-2
(Scale = 1"=1'-0")

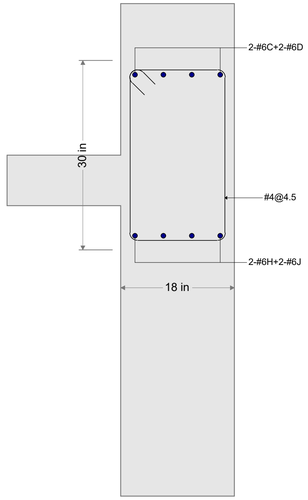

CB-5:Section-3
(Scale = 1"=1'-0")

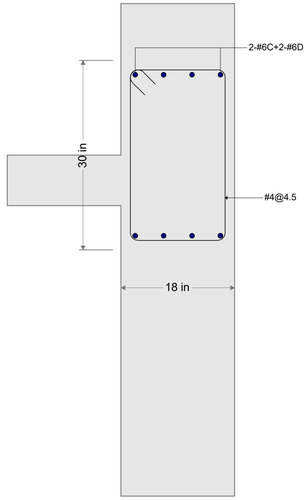

CB-5:Section-4
(Scale = 1"=1'-0")

www.csiamerica.com

No	Description	Date

CB-5:Rebar Profiles

Project Number	
Date	
Drawn By	
Checked By	

S-51

Scale

Story4:CB-5 - Rebar Table

Beam Label	Span/Support	Width	Depth	Bar A	Bar B	Bar C	Bar D	Bar E	Bar F	Bar G	Zone A	Zone B	Zone C	Zone D	Zone E	Elevation Type
CB-5	Support-1	-	-	2-#6A	2-#6B	-	-	-	-	-	-	-	-	-	-	Elevation 1
-	Span-1	18	30	-	-	-	-	-	-	-	#4@4.5	#4@14	#4@15	#4@14	#4@4.5	-
-	Support-2	-	-	-	-	2-#6C	2-#6D	-	-	-	-	-	-	-	-	-
-	Span-2	18	30	-	-	-	-	-	-	-	#4@4.5	#4@14	#4@15	#4@14	#4@4.5	-
-	Support-3	-	-	-	-	2-#6C	2-#6D	-	-	-	-	-	-	-	-	-
-	Span-3	18	30	-	-	-	-	-	-	-	#4@4.5	-	#4@14	-	#4@4.5	-
-	Support-4	-	-	-	-	2-#6C	2-#6D	-	-	-	-	-	-	-	-	-
-	Span-4	18	30	-	-	-	-	-	-	-	#4@4.5	-	#4@14	-	#4@4.5	-
-	Support-5	-	-	2-#6A	2-#6B	-	-	-	-	-	-	-	-	-	-	-

Story4:CB-5-BOQ Summary

Sr. No.	Item	Quantity	Unit
1	Longitudinal Bars	0.55	ton
2	Ties and Stirrups	0.36	ton
3	Total Rebars	0.91	ton
4	Total Beam Length	72	ft
5	Total Beam Volume	270	cu ft
6	Weight/Volume	6.73	lb/cu ft
Note	Does not include weight of Typical Bars		

Story4:CB-5-Rebar Weight Summary

Sr. No.	Size	Area (in²)	Length (ft)	Weight (ton)
1	#4	0.2	1,065.14	0.36
2	#6	0.44	730.39	0.55
Note	Does not include Typical Bars			



CB-6:Elevation (No bars)
(Scale = 1"=3'-0")

www.csiamerica.com


No	Description	Date

CB-5:Beam Table


Project Number	
Date	
Drawn By	
Checked By	

S-52


Scale

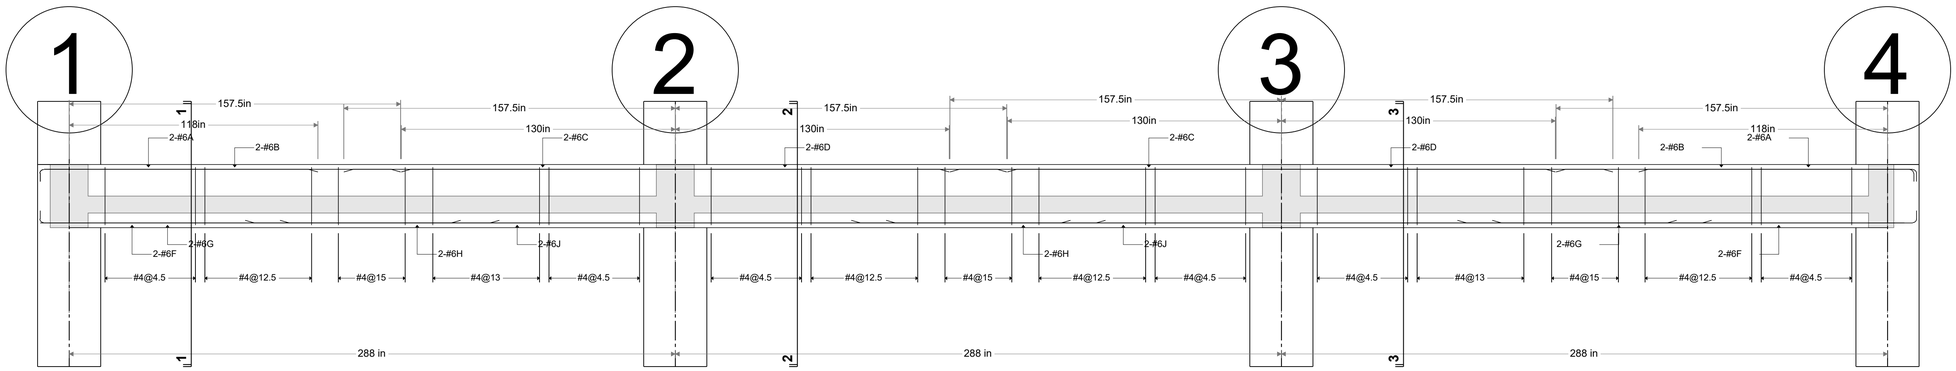

CB-6:Elevation
(Scale = 1"=3'-0")

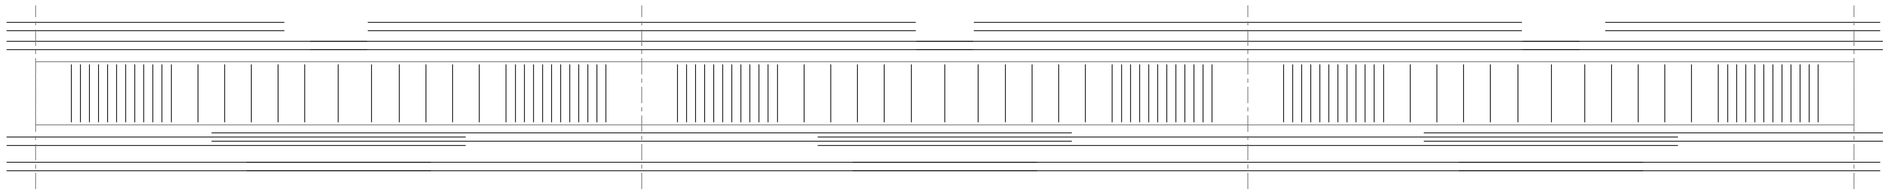

CB-6:Elevation-All Bars
(Scale = 1"=3'-0")

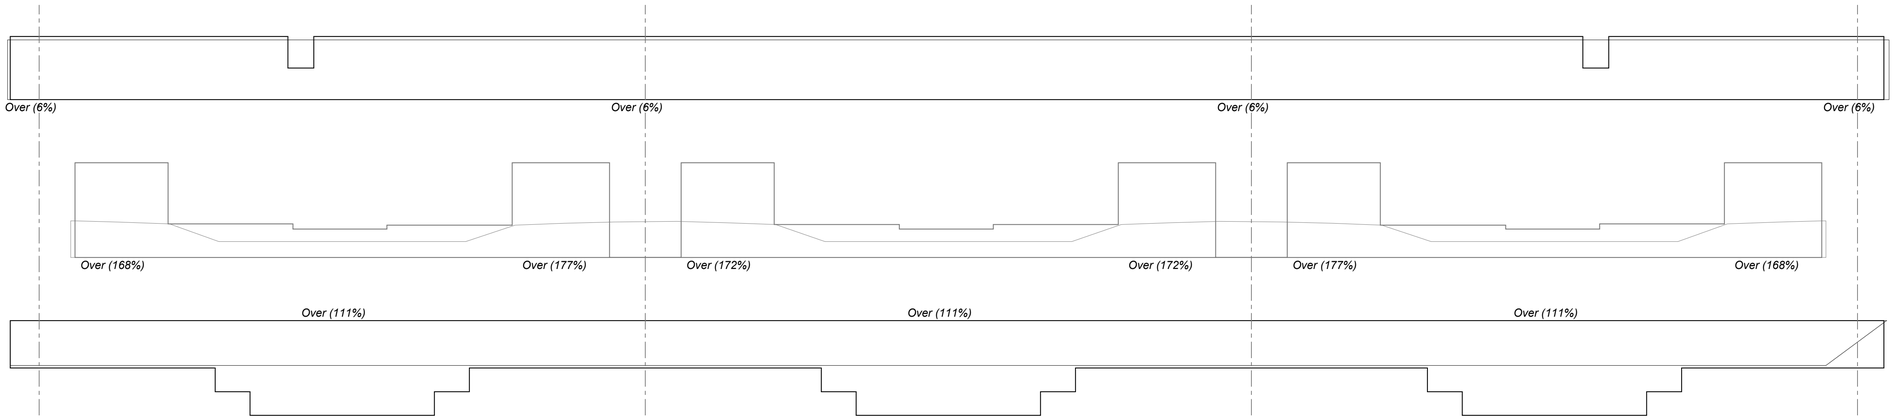

CB-6:Rebar Profiles
(Scale = 1"=3'-0")

www.csiamerica.com


No	Description	Date

CB-6:Elevation


Project Number	
Date	
Drawn By	
Checked By	

S-53


Scale

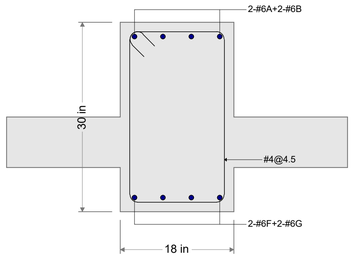

CB-6:Section-1
(Scale = 1"=1'-0")

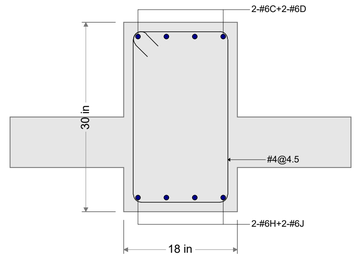

CB-6:Section-2
(Scale = 1"=1'-0")

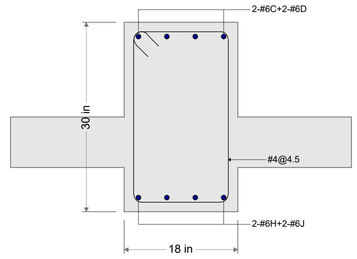

CB-6:Section-3
(Scale = 1"=1'-0")

Story4:CB-6 - Rebar Table

Beam Label	Span/Support	Width	Depth	Bar A	Bar B	Bar C	Bar D	Bar E	Bar F	Bar G	Zone A	Zone B	Zone C	Zone D	Zone E	Elevation Type
CB-6	Support-1	-	-	2-#6A	2-#6B	-	-	-	-	-	-	-	-	-	-	Elevation 1
-	Span-1	18	30	-	-	-	-	-	-	-	#4@4.5	#4@12.5	#4@15	#4@13	#4@4.5	-
-	Support-2	-	-	-	-	2-#6C	2-#6D	-	-	-	-	-	-	-	-	-
-	Span-2	18	30	-	-	-	-	-	-	-	#4@4.5	#4@12.5	#4@15	#4@12.5	#4@4.5	-
-	Support-3	-	-	-	-	2-#6C	2-#6D	-	-	-	-	-	-	-	-	-
-	Span-3	18	30	-	-	-	-	-	-	-	#4@4.5	#4@13	#4@15	#4@12.5	#4@4.5	-
-	Support-4	-	-	2-#6A	2-#6B	-	-	-	-	-	-	-	-	-	-	-

Story4:CB-6-BOQ Summary

Sr. No.	Item	Quantity	Unit
1	Longitudinal Bars	0.52	ton
2	Ties and Stirrups	0.28	ton
3	Total Rebars	0.8	ton
4	Total Beam Length	72	ft
5	Total Beam Volume	270	cu ft
6	Weight/Volume	5.9	lb/cu ft
Note	Does not include weight of Typical Bars		

Story4:CB-6-Rebar Weight Summary

Sr. No.	Size	Area (in²)	Length (ft)	Weight (ton)
1	#4	0.2	815.85	0.28
2	#6	0.44	693.83	0.52
Note	Does not include Typical Bars			

www.csiamerica.com


No	Description	Date

CB-6:Section-1


Project Number	
Date	
Drawn By	
Checked By	

S-54


Scale

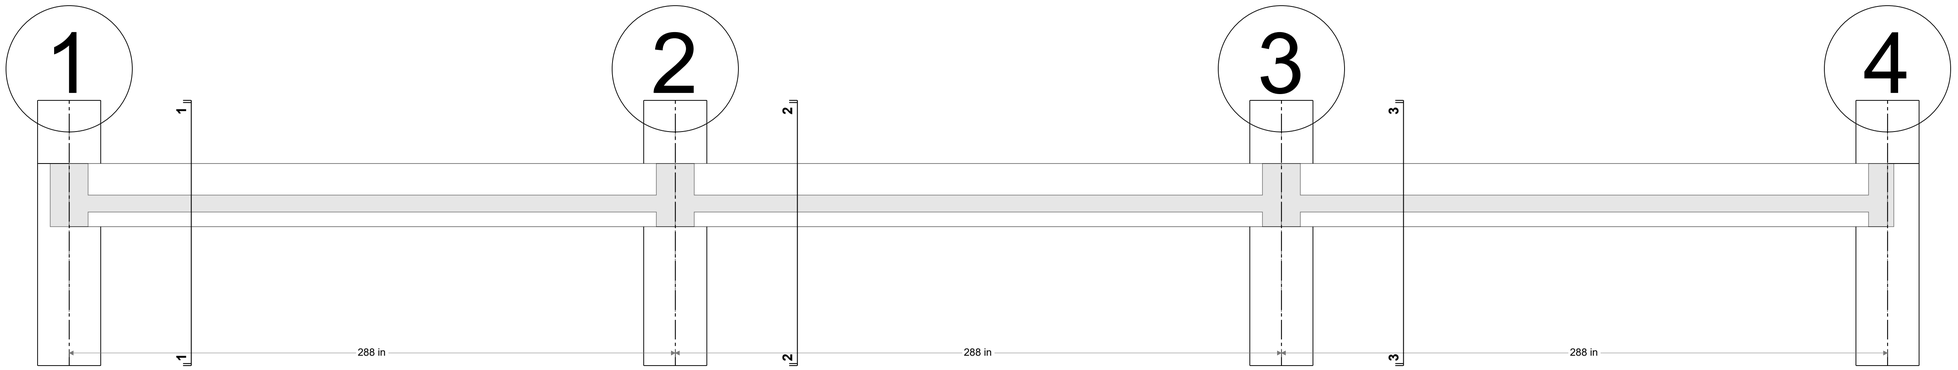

CB-7:Elevation (No bars)
(Scale = 1"=3'-0")

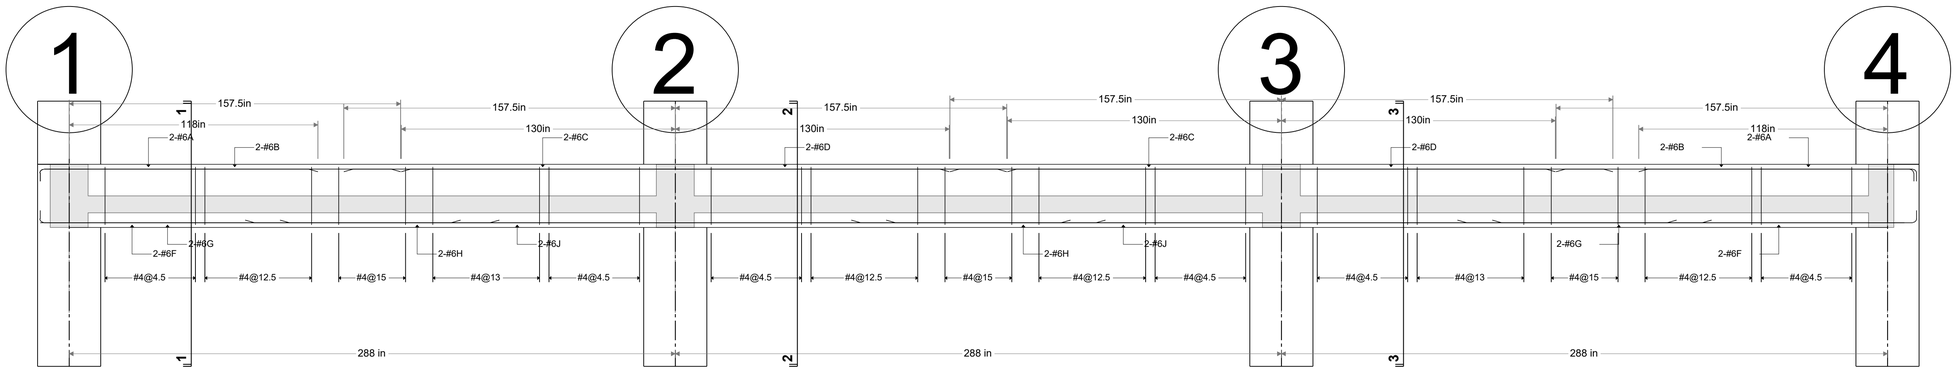

CB-7:Elevation
(Scale = 1"=3'-0")

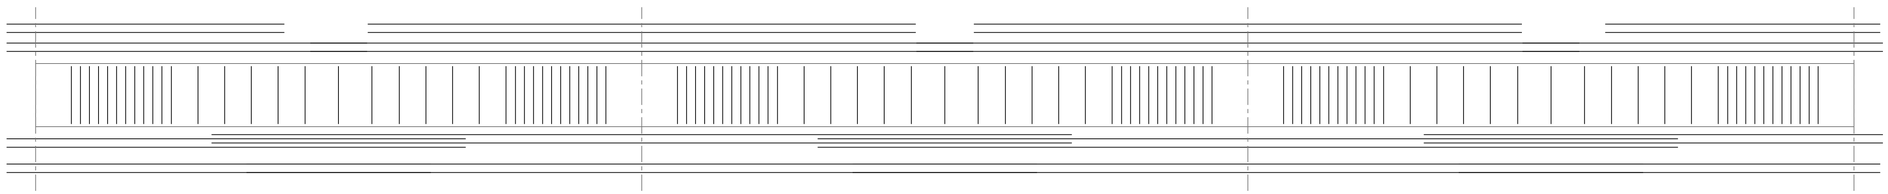

CB-7:Elevation-All Bars
(Scale = 1"=3'-0")

www.csiamerica.com


No	Description	Date

CB-7:Elevation (No bars)

Project Number	
Date	
Drawn By	
Checked By	


S-55

Scale

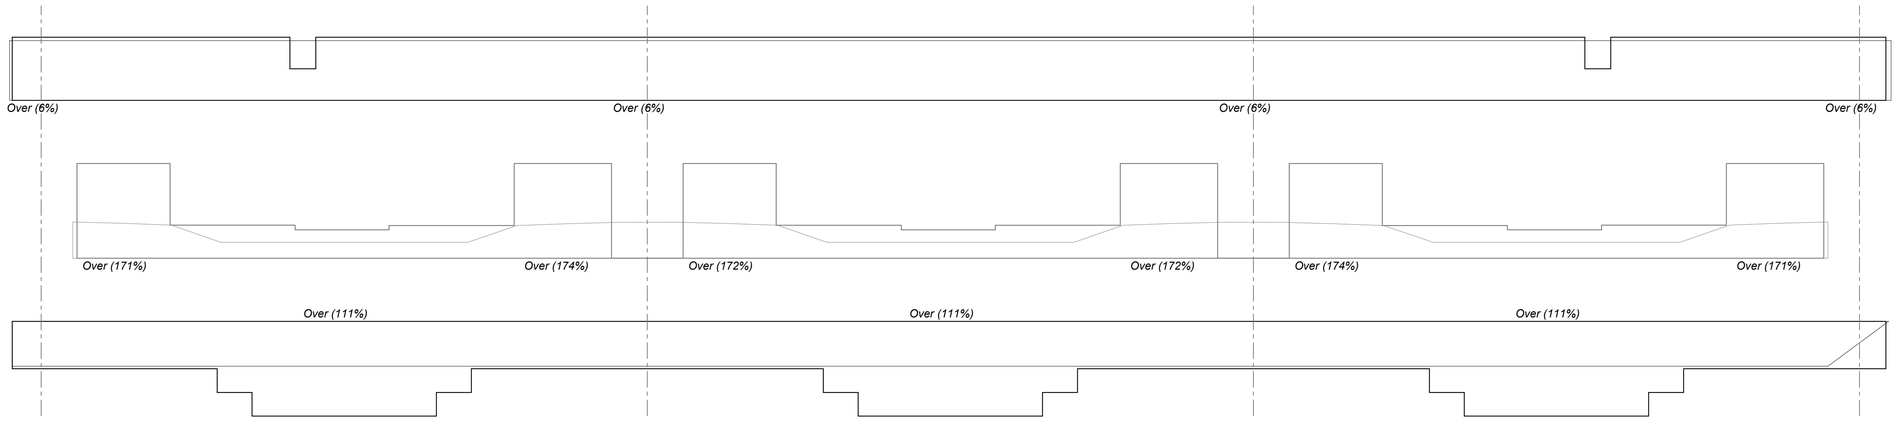


CB-7:Rebar Profiles

(Scale = 1"=3'-0")

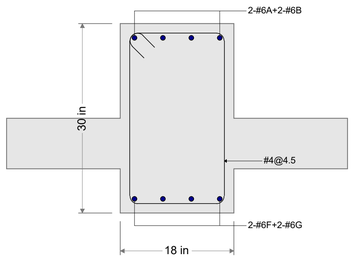


CB-7:Section-1

(Scale = 1"=1'-0")

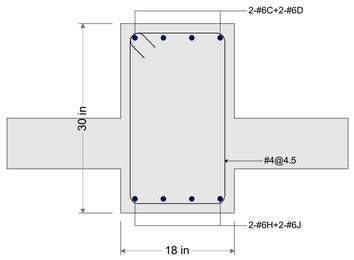

CB-7:Section-2

(Scale = 1"=1'-0")

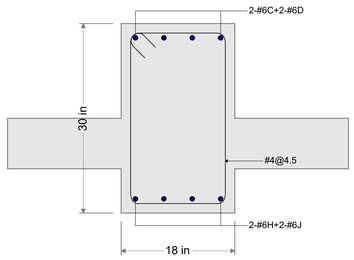

CB-7:Section-3

(Scale = 1"=1'-0")

Story4:CB-7 - Rebar Table

Beam Label	Span/Support	Width	Depth	Bar A	Bar B	Bar C	Bar D	Bar E	Bar F	Bar G	Zone A	Zone B	Zone C	Zone D	Zone E	Elevation Type
CB-7	Support-1	-	-	2-#6A	2-#6B	-	-	-	-	-	-	-	-	-	-	Elevation 1
-	Span-1	18	30	-	-	-	-	-	-	-	#4@4.5	#4@12.5	#4@15	#4@13	#4@4.5	-
-	Support-2	-	-	-	-	2-#6C	2-#6D	-	-	-	-	-	-	-	-	-
-	Span-2	18	30	-	-	-	-	-	-	-	#4@4.5	#4@12.5	#4@15	#4@12.5	#4@4.5	-
-	Support-3	-	-	-	-	2-#6C	2-#6D	-	-	-	-	-	-	-	-	-
-	Span-3	18	30	-	-	-	-	-	-	-	#4@4.5	#4@13	#4@15	#4@12.5	#4@4.5	-
-	Support-4	-	-	2-#6A	2-#6B	-	-	-	-	-	-	-	-	-	-	-

www.csiamerica.com

No	Description	Date

CB-7:Rebar Profiles

Project Number	
Date	
Drawn By	
Checked By	

S-56


Scale

Story4:CB-7-BOQ Summary

Sr. No.	Item	Quantity	Unit
1	Longitudinal Bars	0.52	ton
2	Ties and Stirrups	0.28	ton
3	Total Rebars	0.8	ton
4	Total Beam Length	72	ft
5	Total Beam Volume	270	cu ft
6	Weight/Volume	5.9	lb/cu ft
Note	Does not include weight of Typical Bars		

Story4:CB-7-Rebar Weight Summary

Sr. No.	Size	Area (in²)	Length (ft)	Weight (ton)
1	#4	0.2	815.85	0.28
2	#6	0.44	693.83	0.52
Note	Does not include Typical Bars			

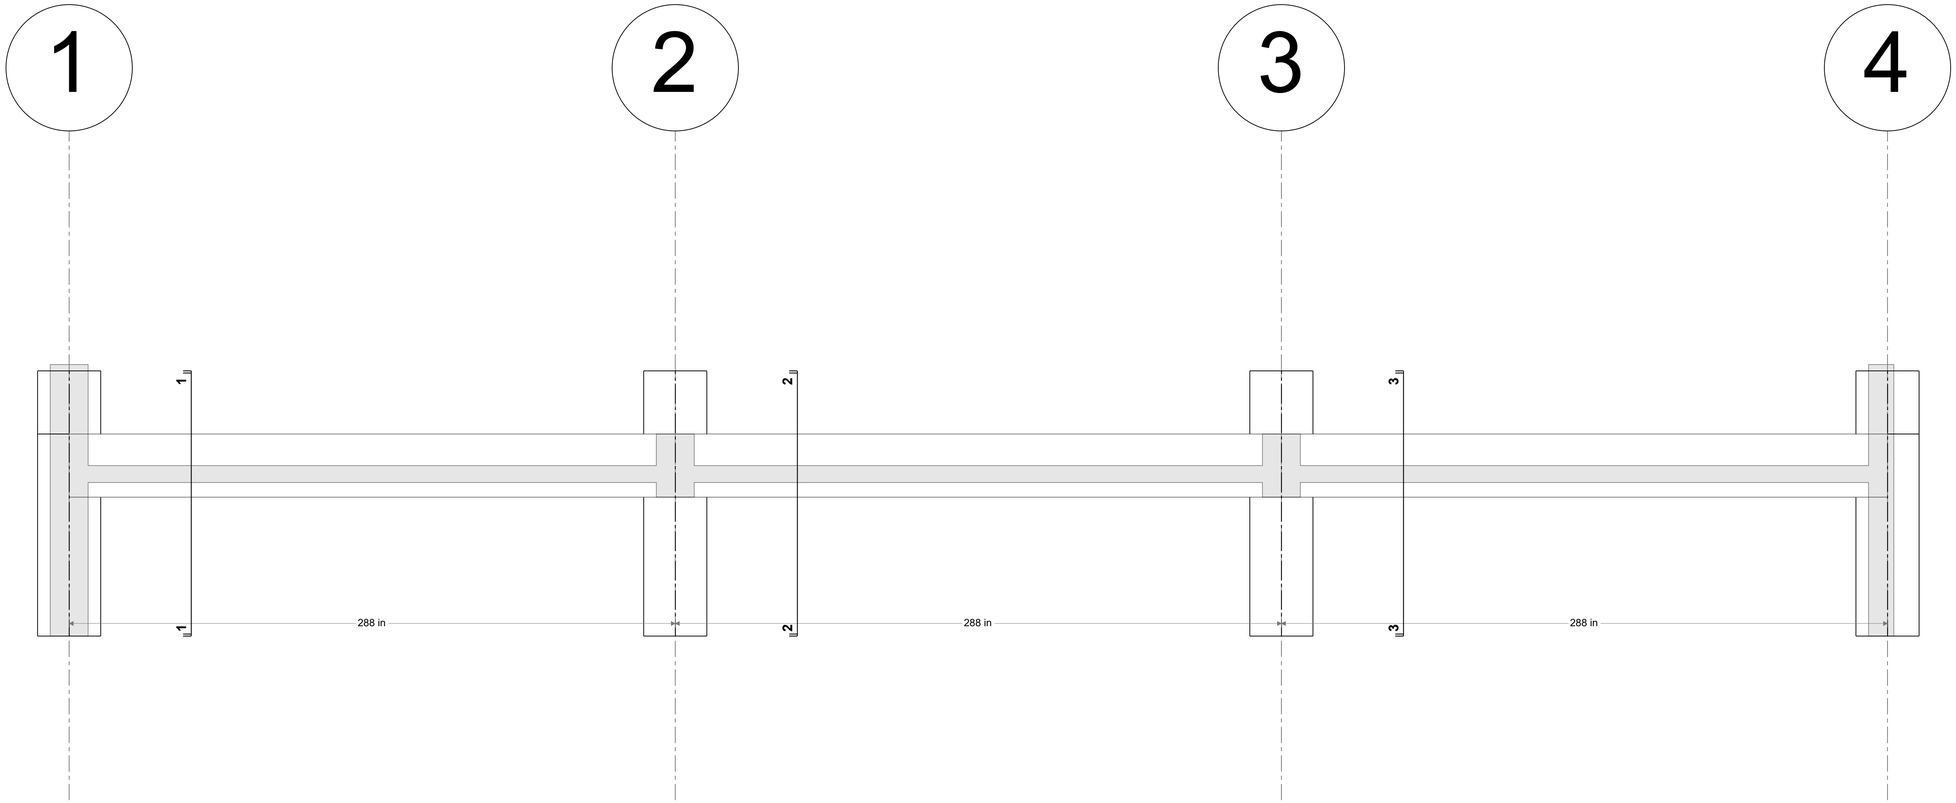

CB-8:Elevation (No bars)
(Scale = 1"=3'-0")

www.csiamerica.com


No	Description	Date

CB-7:BOQ


Project Number	
Date	
Drawn By	
Checked By	

S-57

Scale

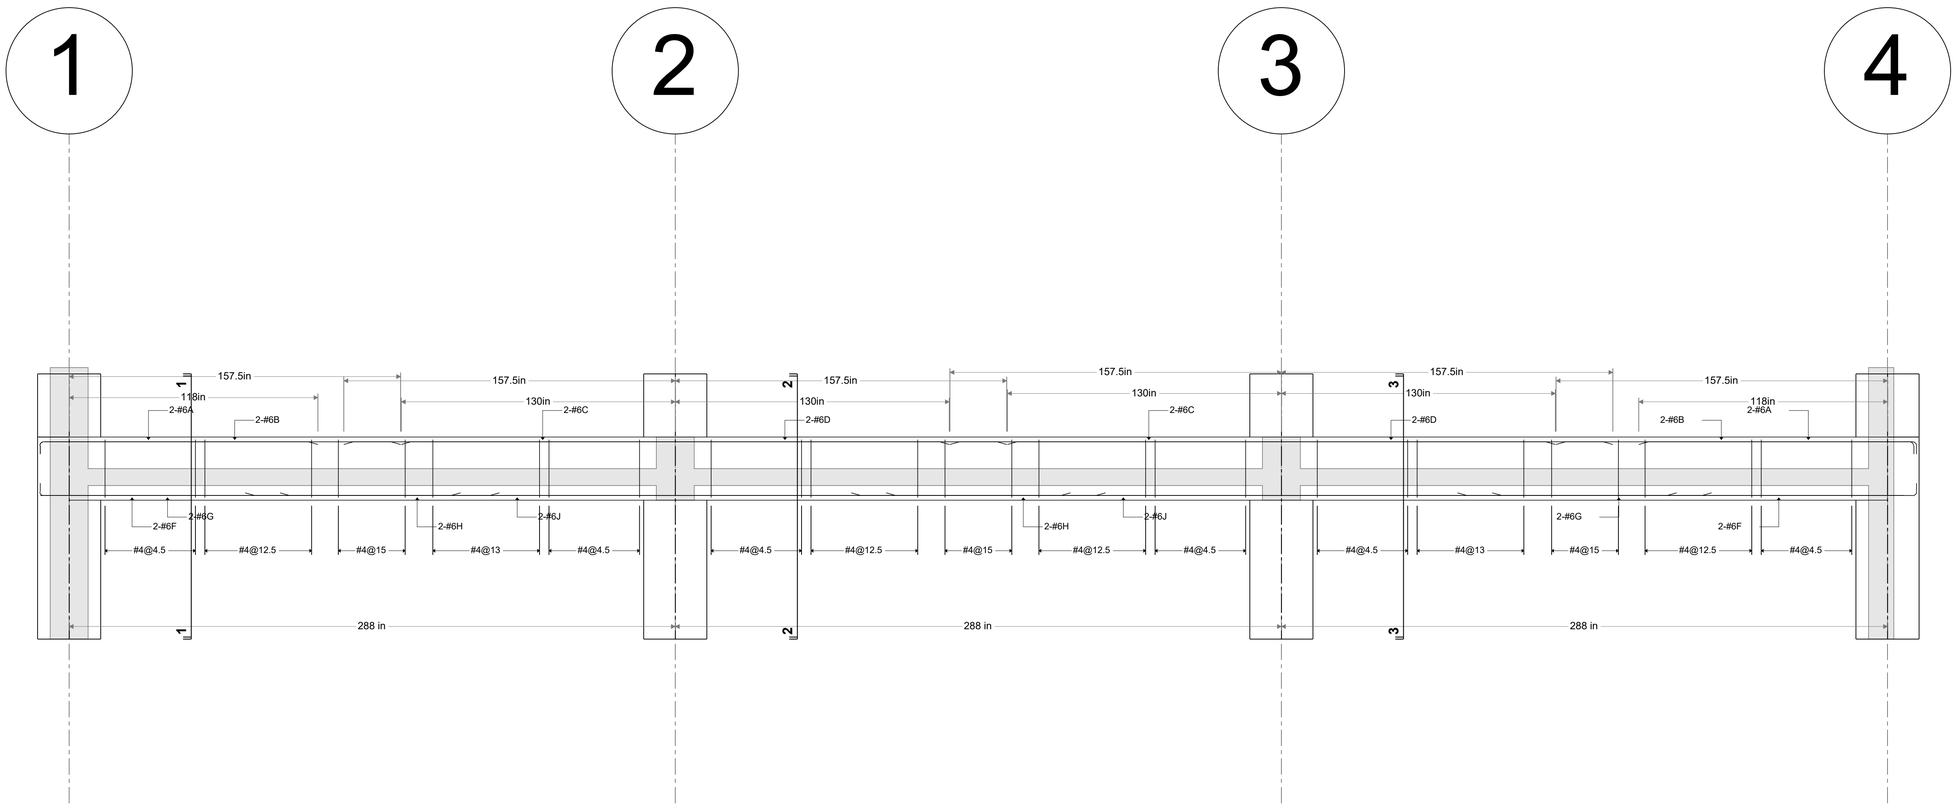

CB-8:Elevation
(Scale = 1"=3'-0")

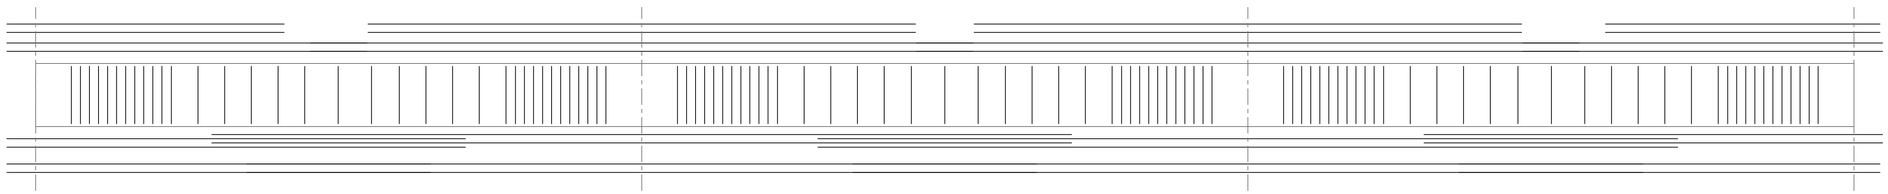

CB-8:Elevation-All Bars
(Scale = 1"=3'-0")

www.csiamerica.com


No	Description	Date

CB-8:Elevation


Project Number	
Date	
Drawn By	
Checked By	

S-58


Scale

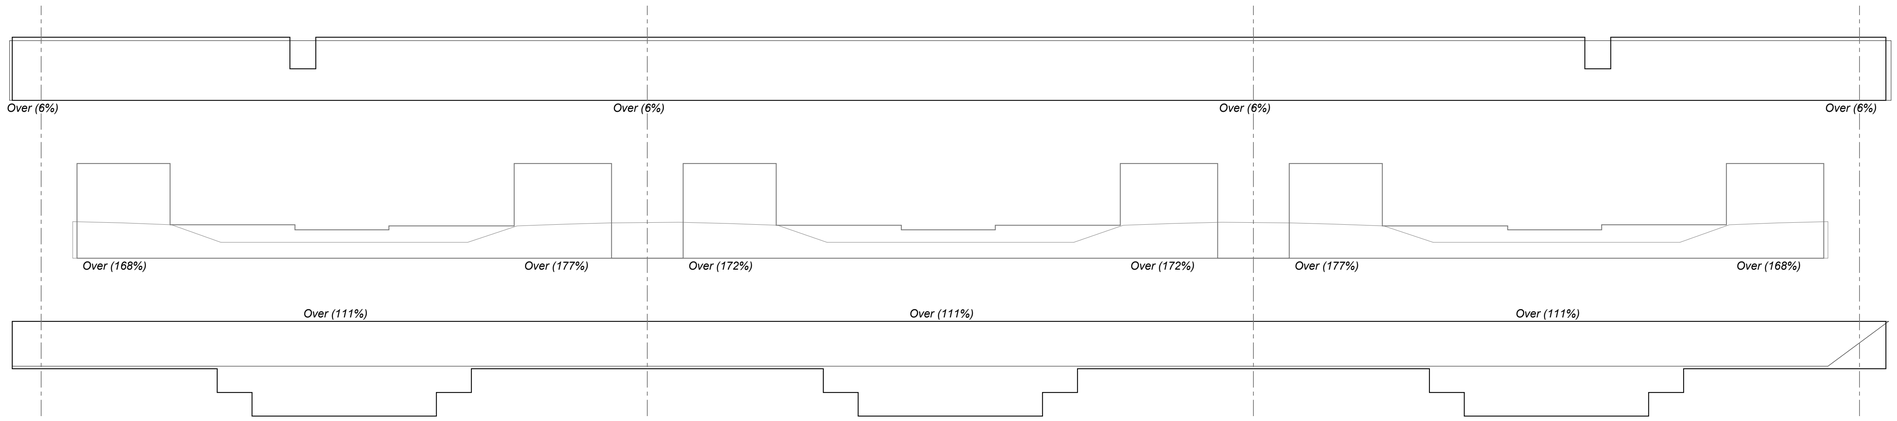


CB-8:Rebar Profiles
(Scale = 1"=3'-0")

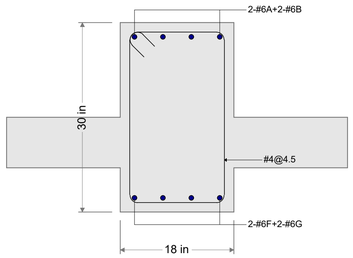

CB-8:Section-1
(Scale = 1"=1'-0")

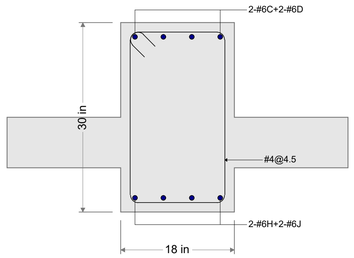

CB-8:Section-2
(Scale = 1"=1'-0")

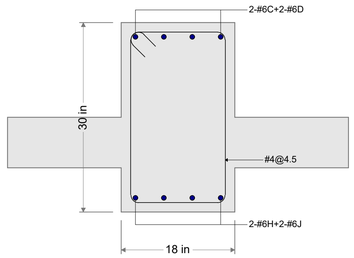

CB-8:Section-3
(Scale = 1"=1'-0")

Story4:CB-8 - Rebar Table

Beam Label	Span/Support	Width	Depth	Bar A	Bar B	Bar C	Bar D	Bar E	Bar F	Bar G	Zone A	Zone B	Zone C	Zone D	Zone E	Elevation Type
CB-8	Support-1	-	-	2-#6A	2-#6B	-	-	-	-	-	-	-	-	-	-	Elevation 1
-	Span-1	18	30	-	-	-	-	-	-	-	#4@4.5	#4@12.5	#4@15	#4@13	#4@4.5	-
-	Support-2	-	-	-	-	2-#6C	2-#6D	-	-	-	-	-	-	-	-	-
-	Span-2	18	30	-	-	-	-	-	-	-	#4@4.5	#4@12.5	#4@15	#4@12.5	#4@4.5	-
-	Support-3	-	-	-	-	2-#6C	2-#6D	-	-	-	-	-	-	-	-	-
-	Span-3	18	30	-	-	-	-	-	-	-	#4@4.5	#4@13	#4@15	#4@12.5	#4@4.5	-
-	Support-4	-	-	2-#6A	2-#6B	-	-	-	-	-	-	-	-	-	-	-

www.csiamerica.com

No	Description	Date

CB-8:Rebar Profiles

Project Number	
Date	
Drawn By	
Checked By	

S-59

Scale

Story4:CB-8-BOQ Summary


Sr. No.	Item	Quantity	Unit
1	Longitudinal Bars	0.52	ton
2	Ties and Stirrups	0.28	ton
3	Total Rebars	0.8	ton
4	Total Beam Length	72	ft
5	Total Beam Volume	270	cu ft
6	Weight/Volume	5.9	lb/cu ft
Note	Does not include weight of Typical Bars		

Story4:CB-8-Rebar Weight Summary

Sr. No.	Size	Area (in²)	Length (ft)	Weight (ton)
1	#4	0.2	815.85	0.28
2	#6	0.44	693.83	0.52
Note	Does not include Typical Bars			



CB-9:Elevation (No bars)
(Scale = 1"=3'-0")

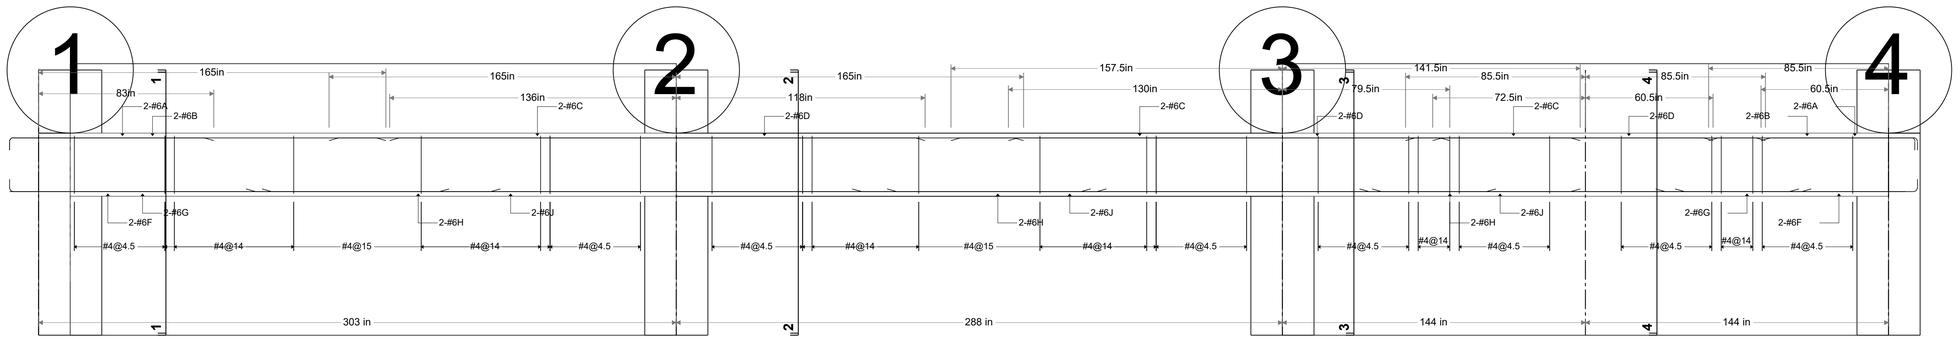

CB-9:Elevation
(Scale = 1"=3'-0")

www.csiamerica.com


No	Description	Date

CB-8:BOQ


Project Number	
Date	
Drawn By	
Checked By	

S-60

Scale

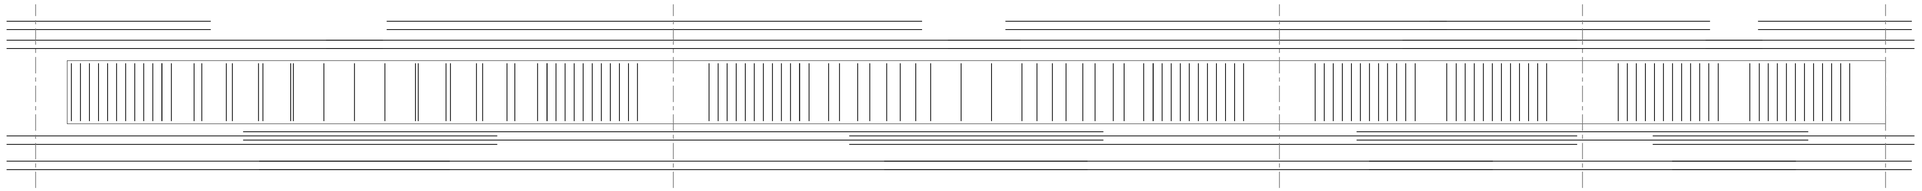

CB-9:Elevation-All Bars
(Scale = 1"=3'-0")

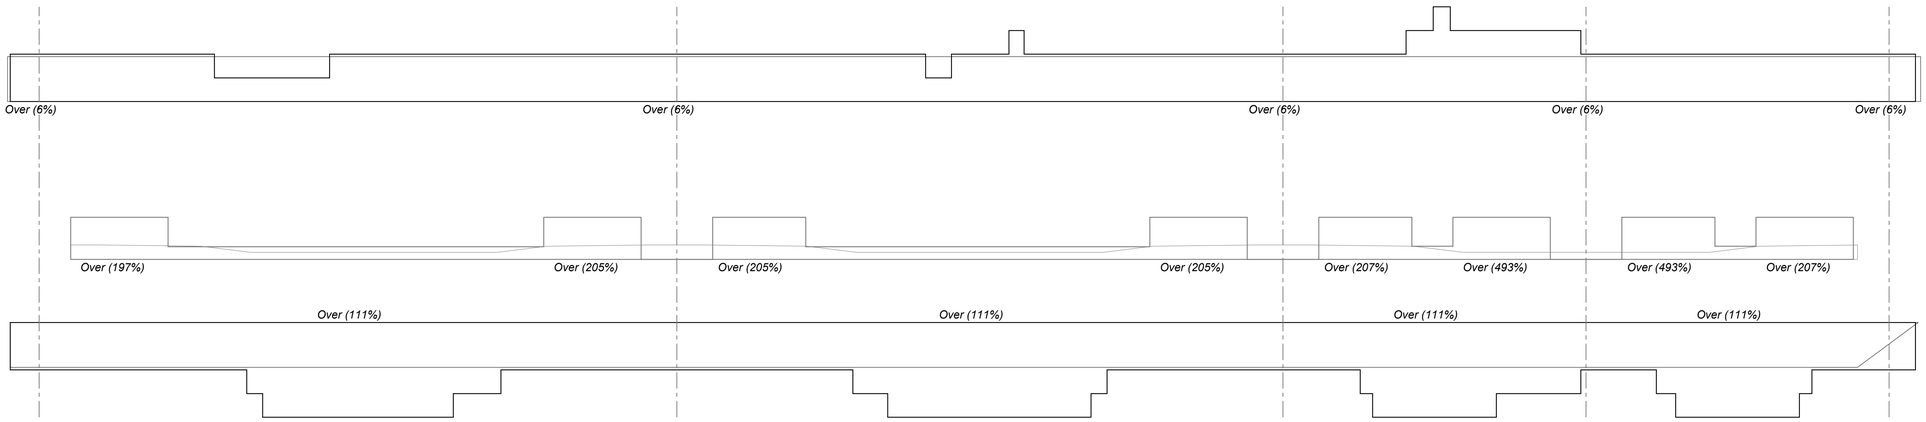

CB-9:Rebar Profiles
(Scale = 1"=3'-0")

www.csiamerica.com


No	Description	Date

CB-9:Elevation-All Bars


Project Number	
Date	
Drawn By	
Checked By	

S-61


Scale

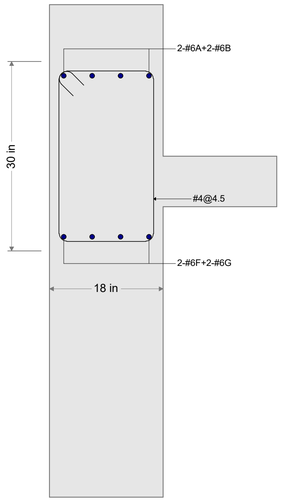


CB-9:Section-1
(Scale = 1"=1'-0")

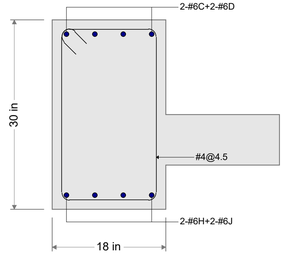

CB-9:Section-2
(Scale = 1"=1'-0")

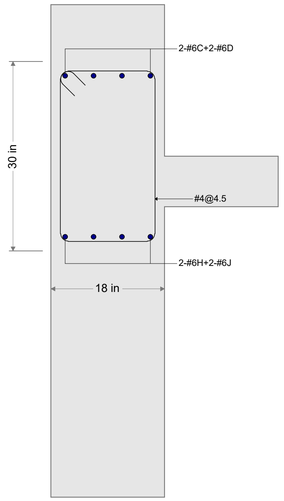

CB-9:Section-3
(Scale = 1"=1'-0")

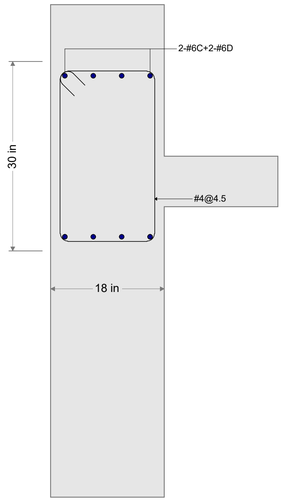

CB-9:Section-4
(Scale = 1"=1'-0")

Story4:CB-9 - Rebar Table

Beam Label	Span/Support	Width	Depth	Bar A	Bar B	Bar C	Bar D	Bar E	Bar F	Bar G	Zone A	Zone B	Zone C	Zone D	Zone E	Elevation Type
CB-9	Support-1	-	-	2-#6A	2-#6B	-	-	-	-	-	-	-	-	-	-	Elevation 1
-	Span-1	18	30	-	-	-	-	-	-	-	#4@4.5	#4@14	#4@15	#4@14	#4@4.5	-
-	Support-2	-	-	-	-	2-#6C	2-#6D	-	-	-	-	-	-	-	-	-
-	Span-2	18	30	-	-	-	-	-	-	-	#4@4.5	#4@14	#4@15	#4@14	#4@4.5	-
-	Support-3	-	-	-	-	2-#6C	2-#6D	-	-	-	-	-	-	-	-	-
-	Span-3	18	30	-	-	-	-	-	-	-	#4@4.5	-	#4@14	-	#4@4.5	-
-	Support-4	-	-	-	-	2-#6C	2-#6D	-	-	-	-	-	-	-	-	-
-	Span-4	18	30	-	-	-	-	-	-	-	#4@4.5	-	#4@14	-	#4@4.5	-
-	Support-5	-	-	2-#6A	2-#6B	-	-	-	-	-	-	-	-	-	-	-

Story4:CB-9-BOQ Summary

Sr. No.	Item	Quantity	Unit
1	Longitudinal Bars	0.55	ton
2	Ties and Stirrups	0.36	ton
3	Total Rebars	0.91	ton
4	Total Beam Length	72	ft
5	Total Beam Volume	270	cu ft
6	Weight/Volume	6.73	lb/cu ft
Note	Does not include weight of Typical Bars		

www.csiamerica.com


No	Description	Date

CB-9:Section-1


Project Number	
Date	
Drawn By	
Checked By	

S-62


Scale

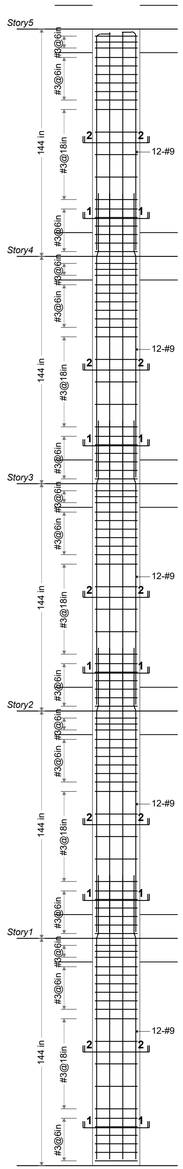


CS-11:Full Elevation-2
(Scale = 1"=4'-0")

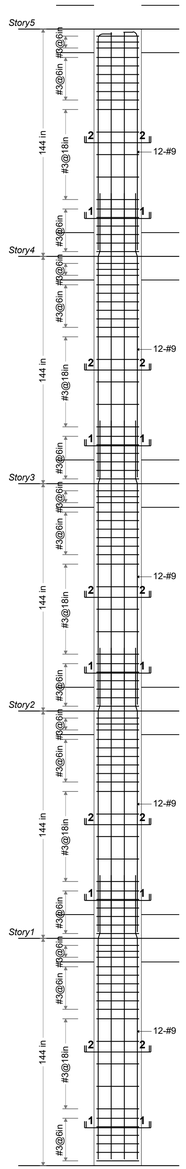


CS-11:Full Elevation-3
(Scale = 1"=4'-0")

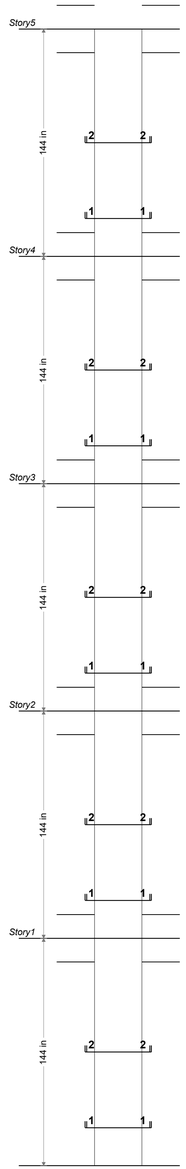

CS-11:Full Elevation-2 (No Bars)
(Scale = 1"=4'-0")

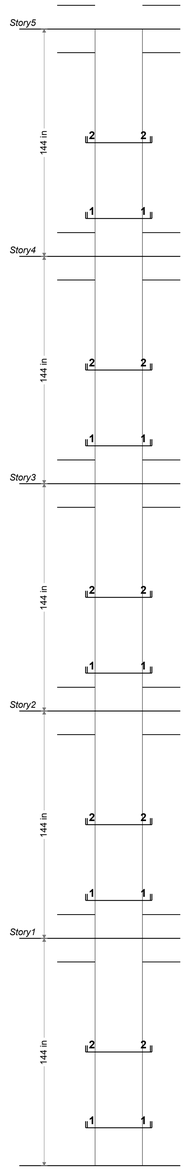

CS-11:Full Elevation-3 (No Bars)
(Scale = 1"=4'-0")

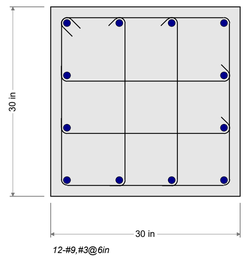

CS-11: Section-1
(Scale = 1"=1'-0")

Story4:CB-9-Rebar Weight Summary

Sr. No.	Size	Area (in²)	Length (ft)	Weight (ton)
1	#4	0.2	1,065.14	0.36
2	#6	0.44	730.39	0.55
Note	Does not include Typical Bars			

www.csiamerica.com


No	Description	Date

CB-9:Rebar Weights

Project Number	
Date	
Drawn By	
Checked By	

S-63

Scale

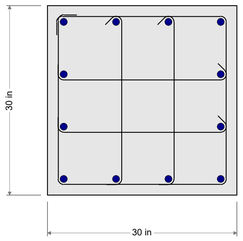


CS-11: Section-2
(Scale = 1"=1'-0")

CS-11-BOQ Summary


Sr. No.	Item	Quantity	Unit
1	Longitudinal Bars	1.46	ton
2	Ties and Stirrups	0.29	ton
3	Total Rebars	1.75	ton
4	Total Column Length	60	ft
5	Total Column Volume	375	cu ft
6	Weight/Volume	9.35	lb/cu ft

CS-11-Rebar Weight Summary

Sr. No.	Size	Area (in²)	Length (ft)	Weight (ton)
1	#3	0.11	1,572.01	0.29
2	#9	1	480	0.82

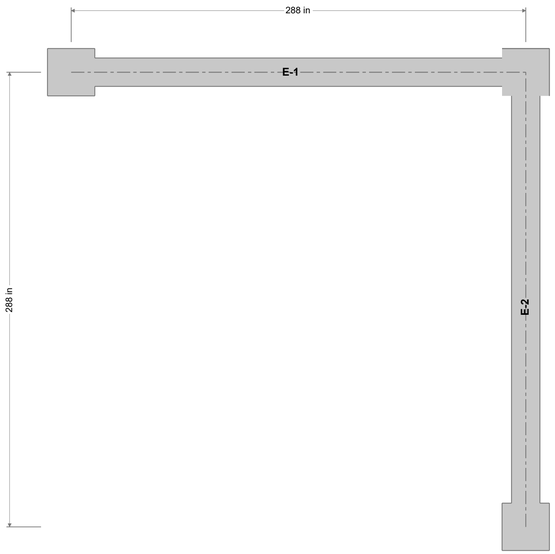

WS-1:Base Plan
(Scale = 1"=4'-0")

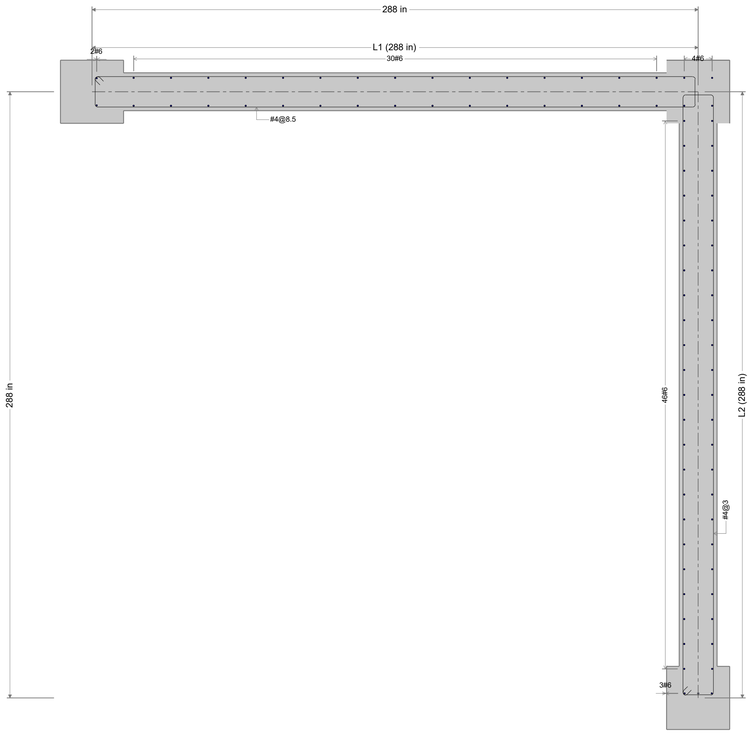

WS-1:Section-Story1
(Scale = 1"=3'-0")

www.csiamerica.com


No	Description	Date

CS-11: Section-2


Project Number	
Date	
Drawn By	
Checked By	

S-64

Scale

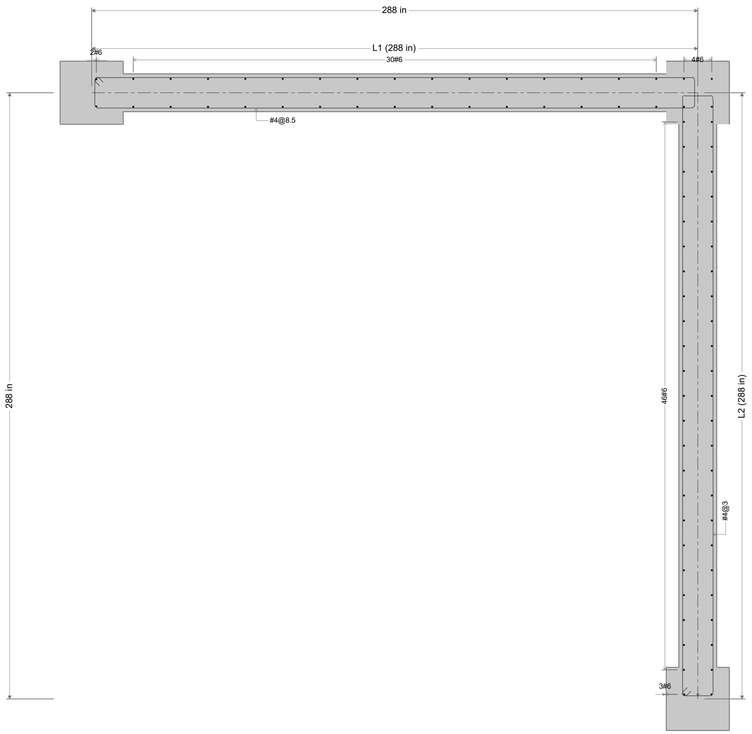

WS-1:Section-Story2
(Scale = 1"=3'-0")

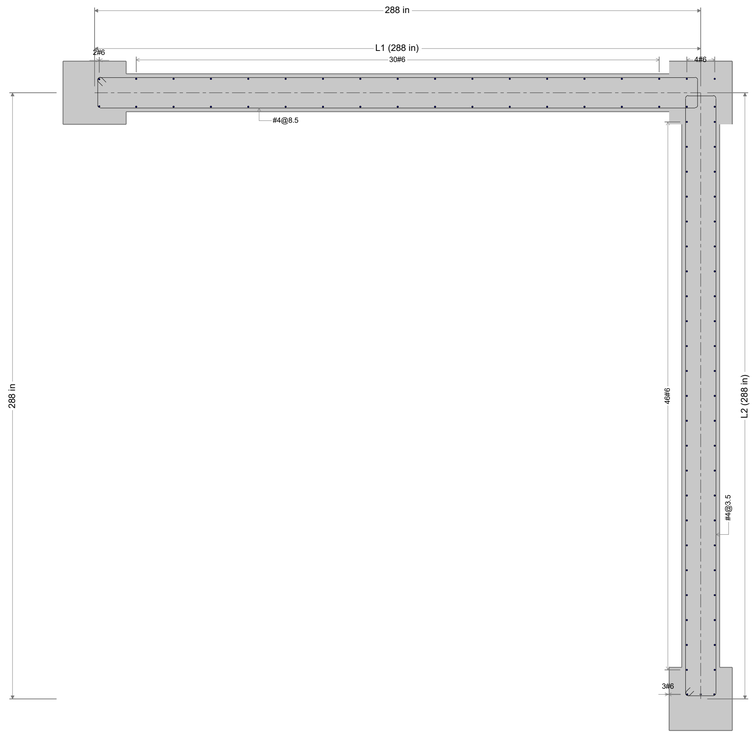

WS-1:Section-Story3
(Scale = 1"=3'-0")

www.csiamerica.com


No	Description	Date

WS-1:Section-Story2


Project Number	
Date	
Drawn By	
Checked By	

S-65

Scale

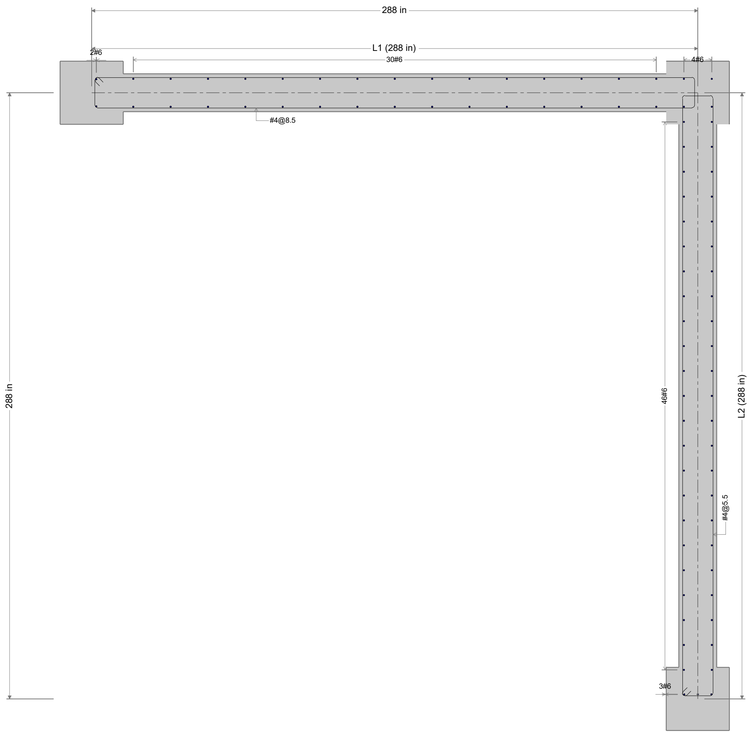

WS-1:Section-Story4
(Scale = 1"=3'-0")

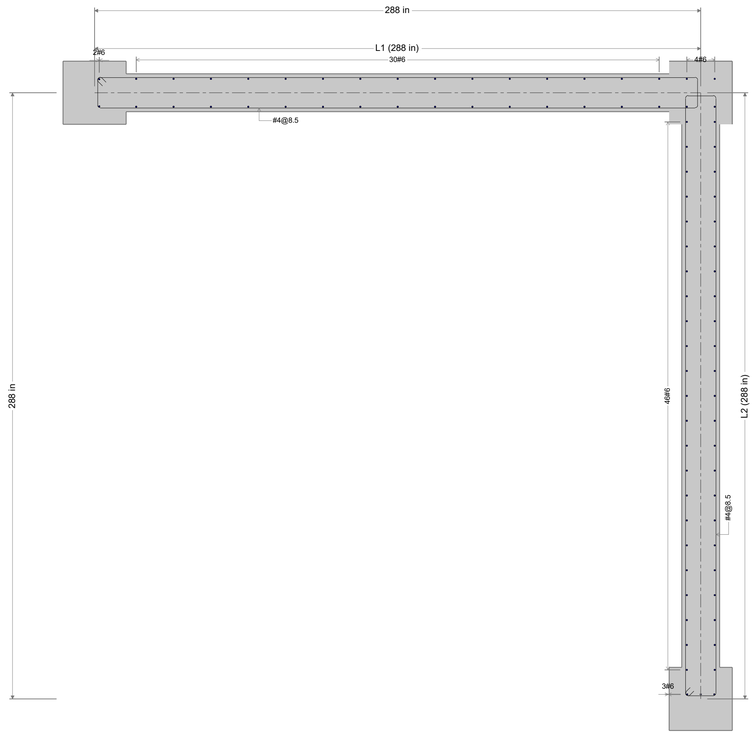

WS-1:Section-Story5
(Scale = 1"=3'-0")

www.csiamerica.com


No	Description	Date

WS-1:Section-Story4


Project Number	
Date	
Drawn By	
Checked By	

S-66

Scale

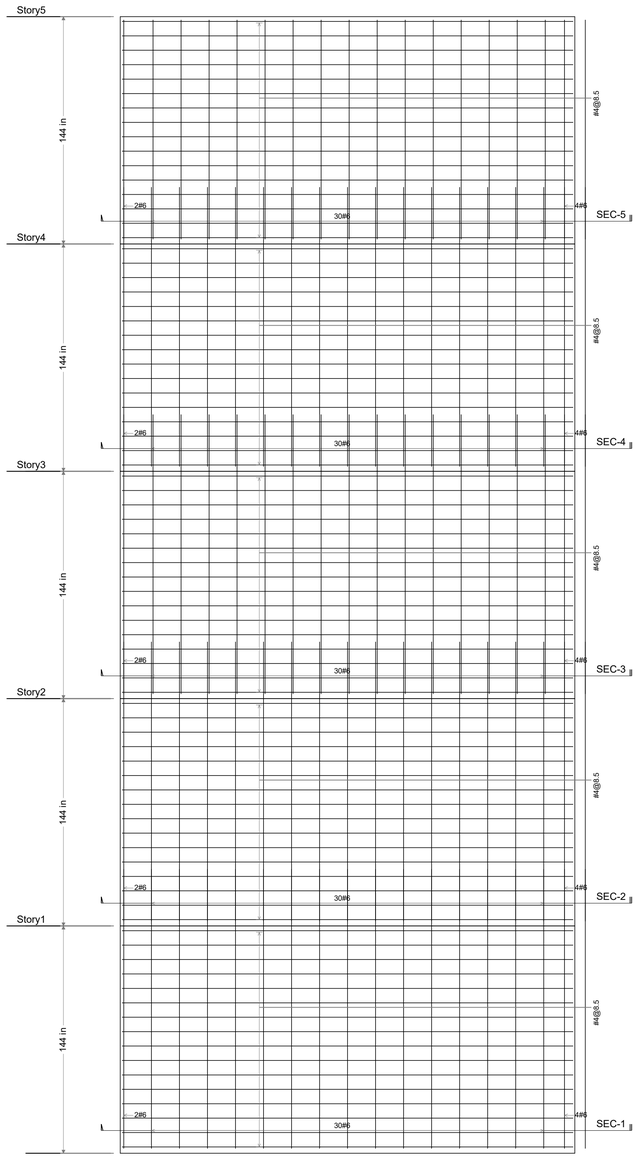

WS-1:E-1
(Scale = 1"=4'-0")

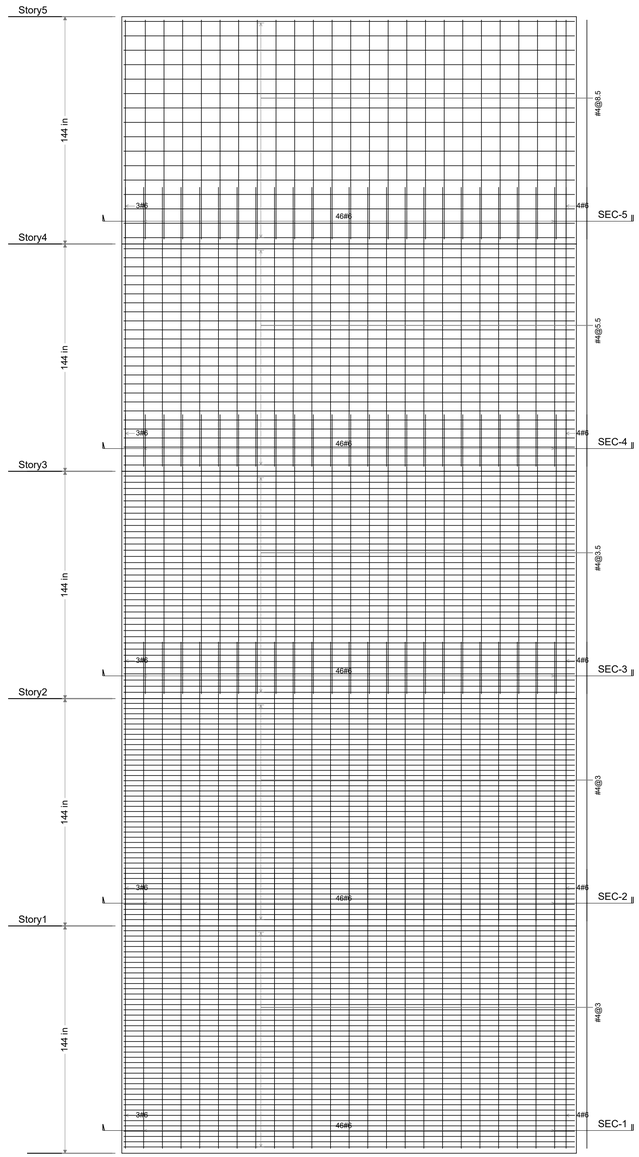

WS-1:E-2
(Scale = 1"=4'-0")

www.csiamerica.com


No	Description	Date

WS-1:E-1


Project Number	
Date	
Drawn By	
Checked By	

S-67

Scale	

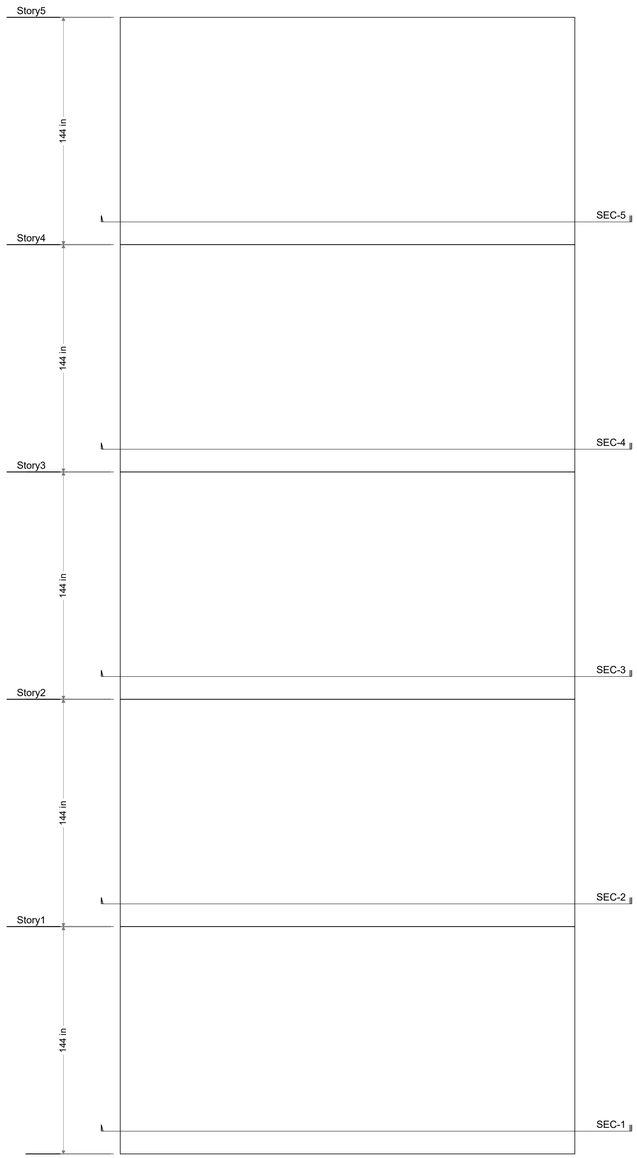

WS-1:E-1 (No Bars)
(Scale = 1"=4'-0")

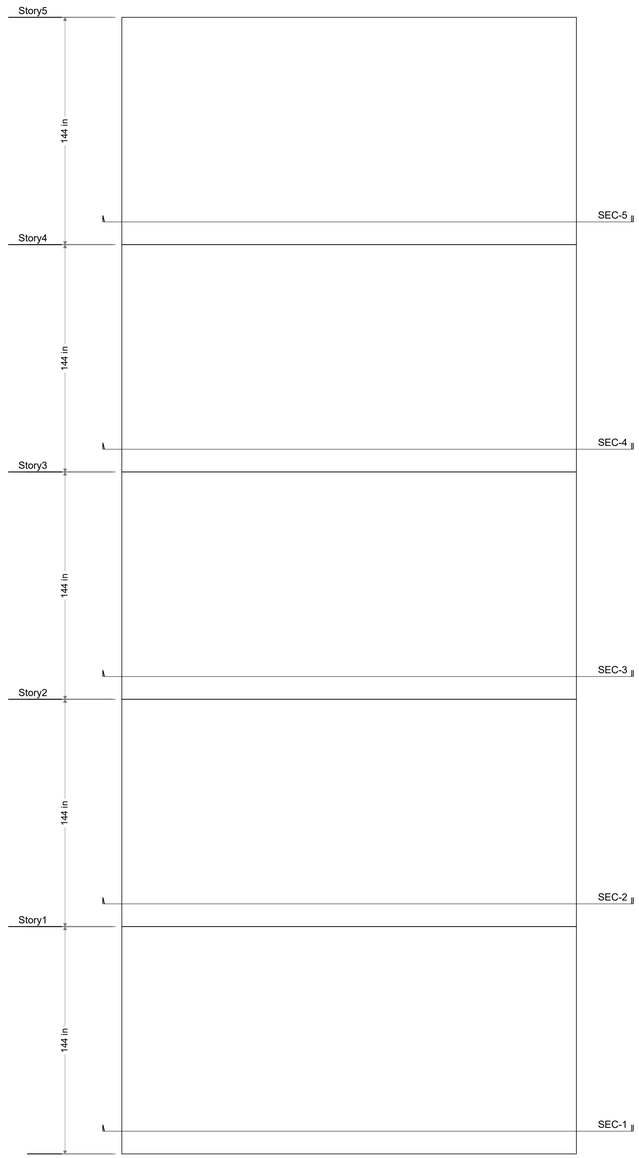

WS-1:E-2 (No Bars)
(Scale = 1"=4'-0")

WS-1-BOQ Summary

Sr. No.	Item	Quantity	Unit
1	Longitudinal Bars	4.57	ton
2	Ties and Stirrups	4.28	ton
3	Total Rebars	8.85	ton

WS-1-Rebar Weight Summary

Sr. No.	Size	Area (in²)	Length (ft)	Weight (ton)
1	#4	0.2	12,567.33	4.28
2	#6	0.44	6,105.83	4.57

www.csiamerica.com

No	Description	Date

WS-1:E-1 (No Bars)

Project Number	
Date	
Drawn By	
Checked By	

S-68

Scale