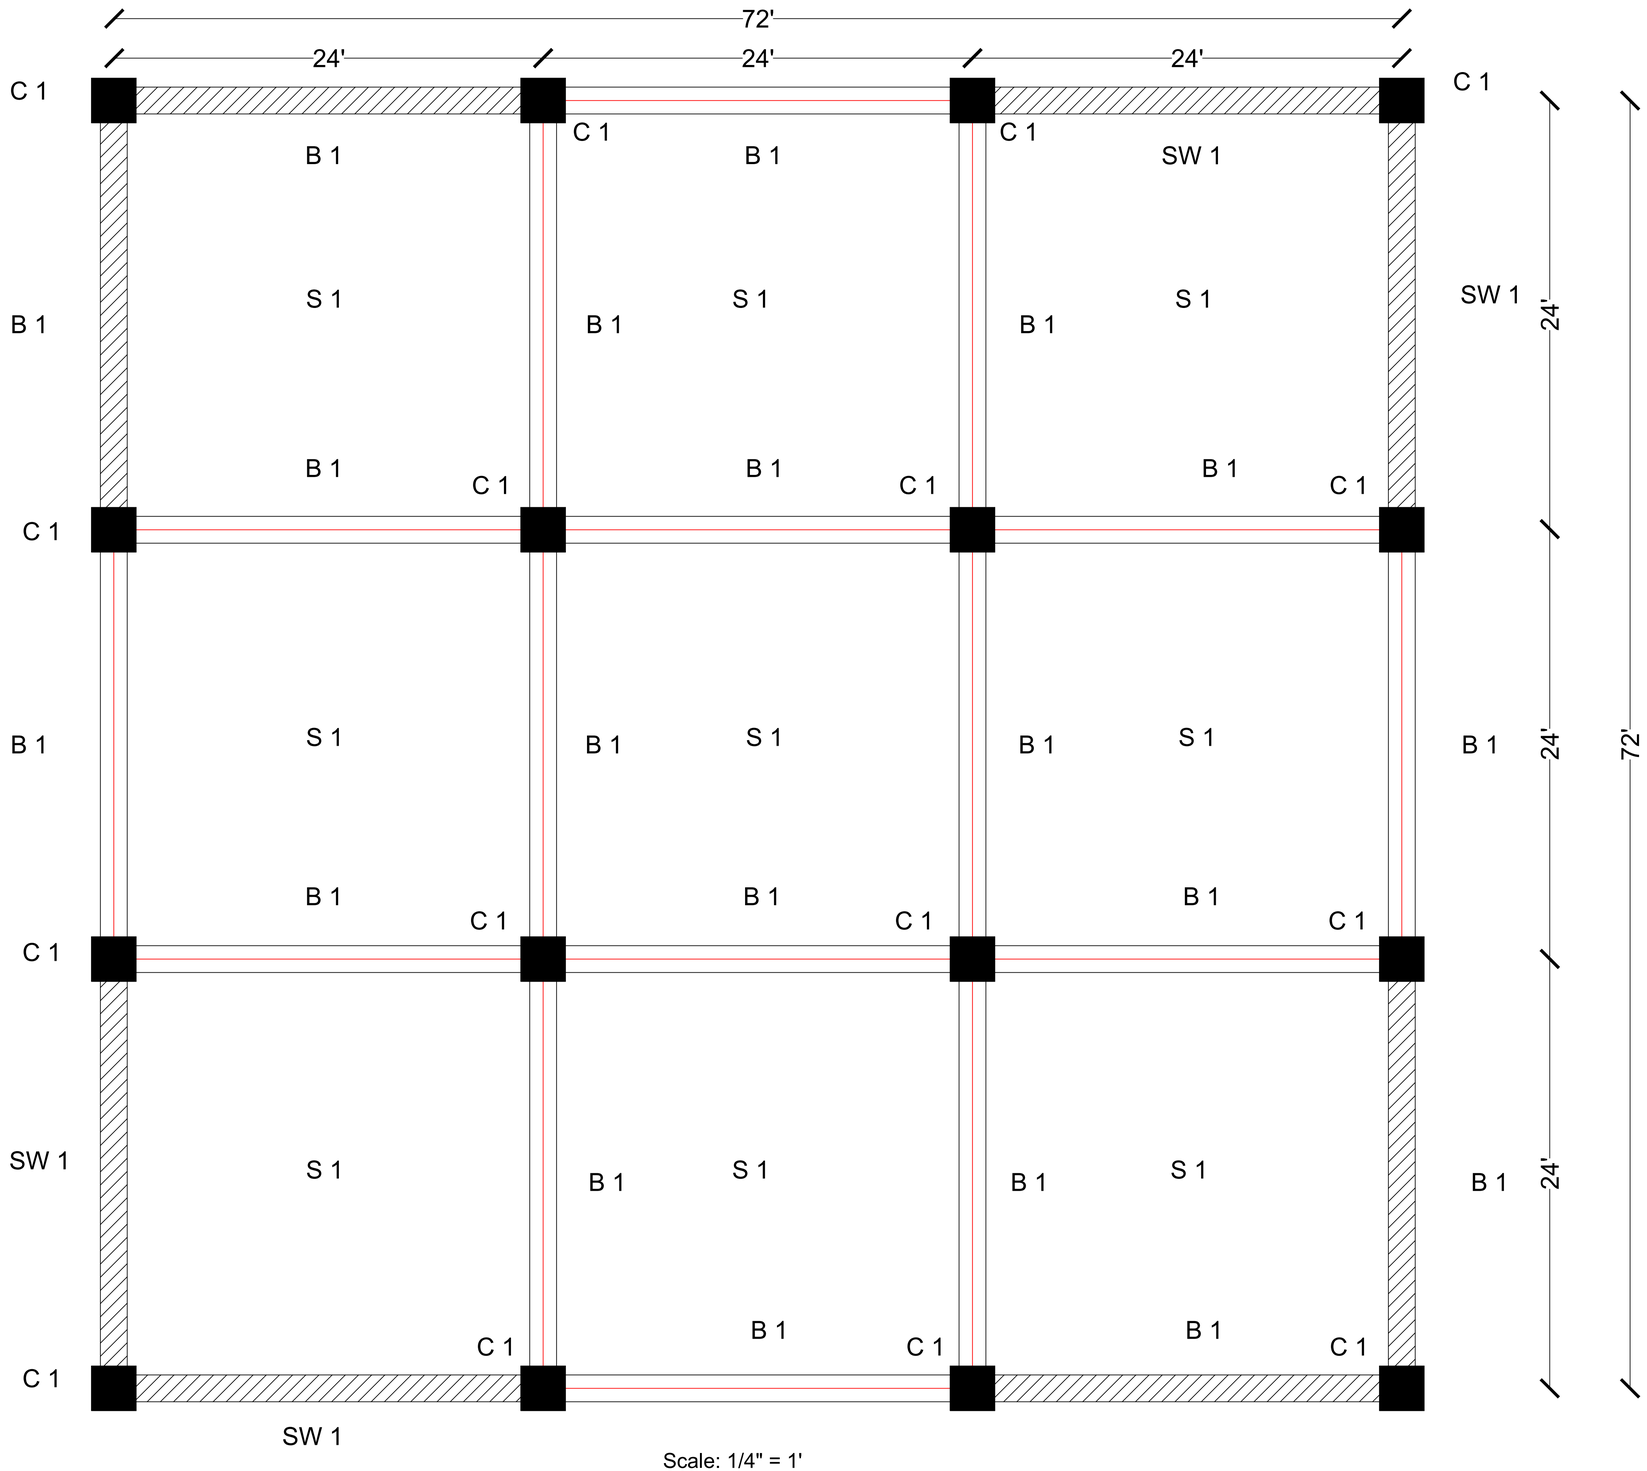


Beam Column Layout Plan

General Notes

MEMBER SCHEDULE:

(f'c=4 ksi, fy=60 ksi)

C1 Column: 30"x30"
12-#9 vert
#4 hoops+xties @4"(lo)
/ 6"(mid)

B1 Beam: 18"x30"
3-#7 T&B
#4 hoops @5"(hinge)
/ 12"(mid)

SW1 Wall: 18" x 24'-0"
#4 @8" EF vert
#5 @8" EF horiz
9 #9 ea end
#4 xties @16"
bndry ties @<=8"

S1: Slab 8"
#5 @7-1/2" col-strip top;
#5 @16" elsewhere E.W.


No.	Revision/Issue	Date

Firm Name and Address

Project Name and Address

5 Story RC Building
San Francisco
California
94105


Project	Sheet
RC Dual System	1
Date: 11/2/2026	
Scale: As Noted	

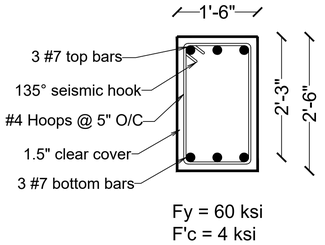

Fy = 60 ksi
F'c = 4 ksi

Scale: 3/4" = 1'

Beam Section (hinge zone)

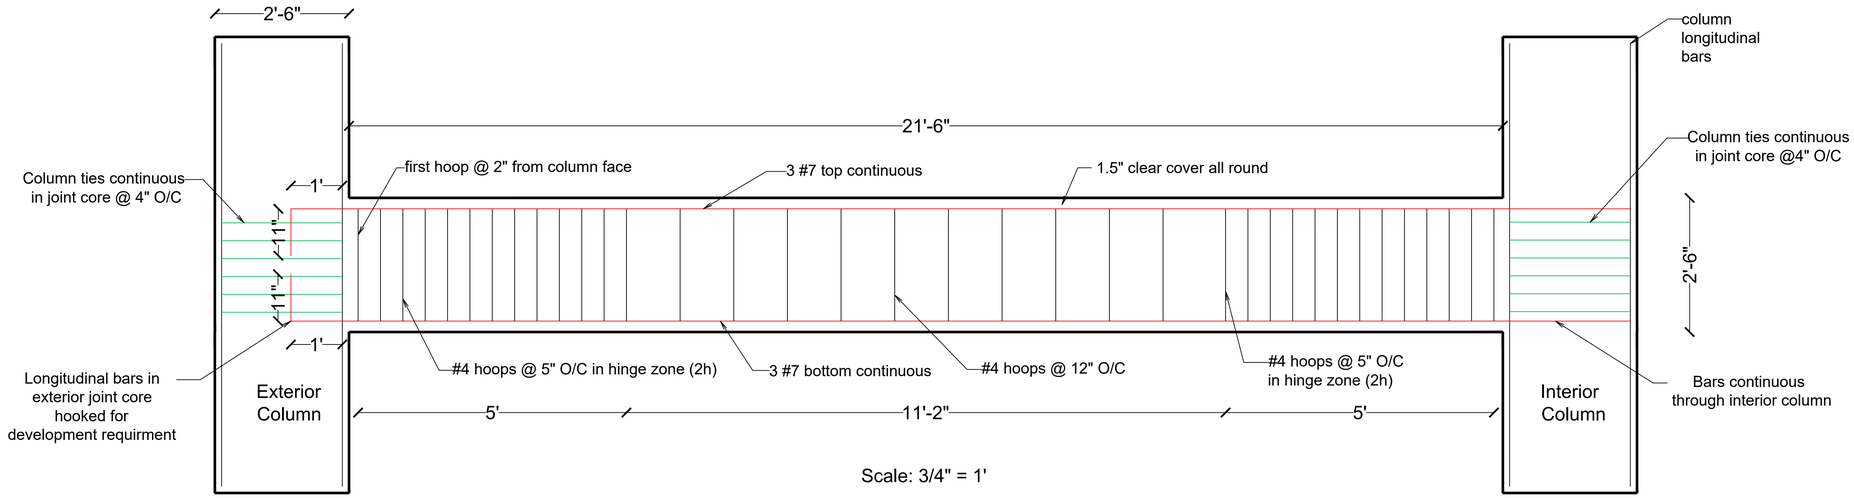

Scale: 3/4" = 1'

Special Moment Resisting Frame / Beam Elevation

General Notes


No.	Revision/Issue	Date

Firm Name and Address

Project Name and Address

5 Story RC Building
San Francisco
California
94105


Project	Sheet
RC Dual System	2
Date: 11/2/2026	
Scale: As Noted	

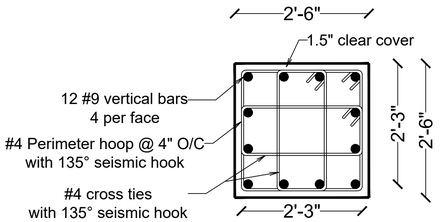

Fy = 60 ksi
F'c = 4 ksi

Scale: 3/4" = 1'

Column Section (hinge zone)

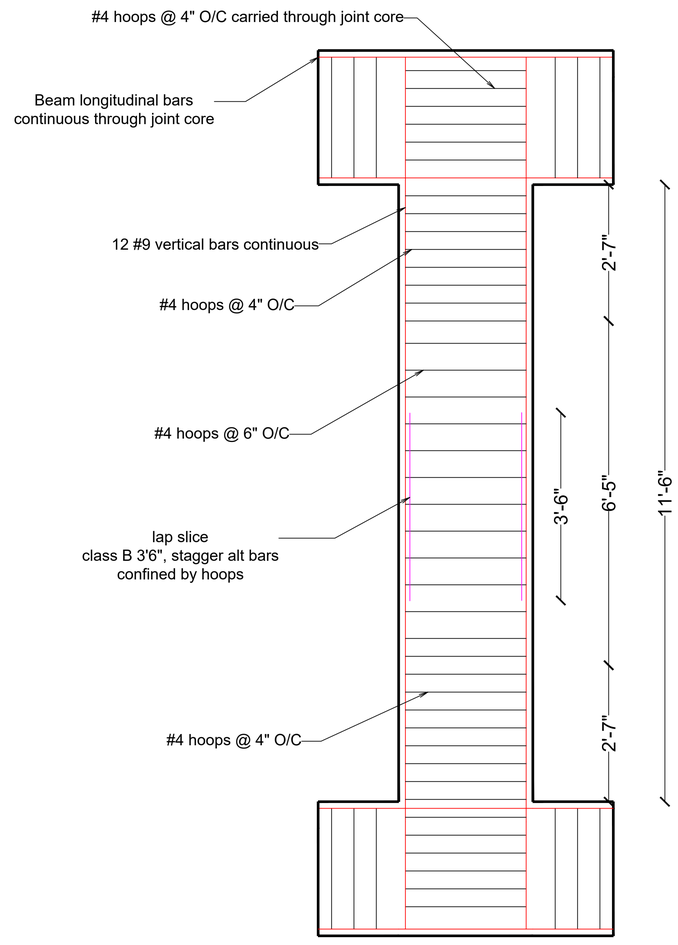

Scale: 3/4" = 1'

Column Elevation

General Notes


No.	Revision/Issue	Date

Firm Name and Address

Project Name and Address

5 Story RC Building
San Francisco
California
94105

Project	Sheet
RC Dual System	3
Date: 11/2/2026	
Scale: As Noted	

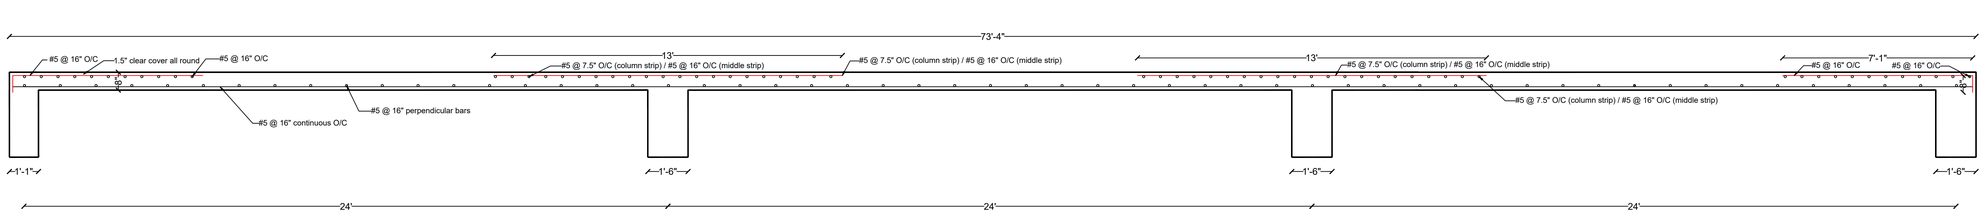

Scale: 3/8" = 1'

Slab Section

General Notes


No.	Revision/Issue	Date

Firm Name and Address

Project Name and Address

5 Story RC Building
San Francisco
California
94105

Project	Sheet
RC Dual System	4
Date: 11/2/2026	
Scale: As Noted	

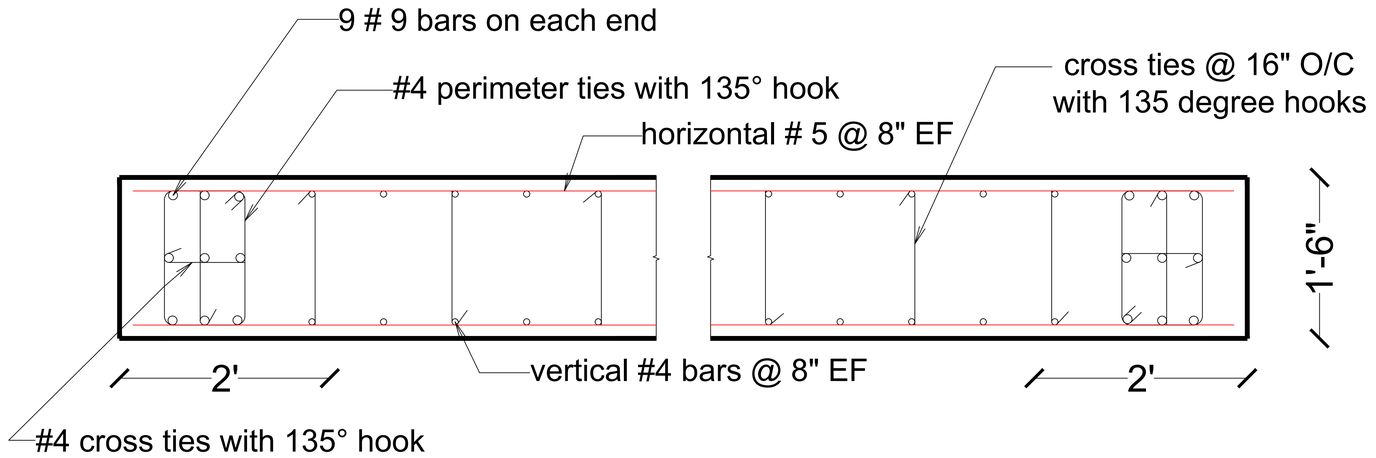

Scale: 1 - 1/2" = 1'

Shear Wall horizontal Section

General Notes


No.	Revision/Issue	Date

Firm Name and Address

Project Name and Address

5 Story RC Building
San Francisco
California
94105

Project: RC Dual System	Sheet: 5
Date: 11/2/2026	
Scale: As Noted	

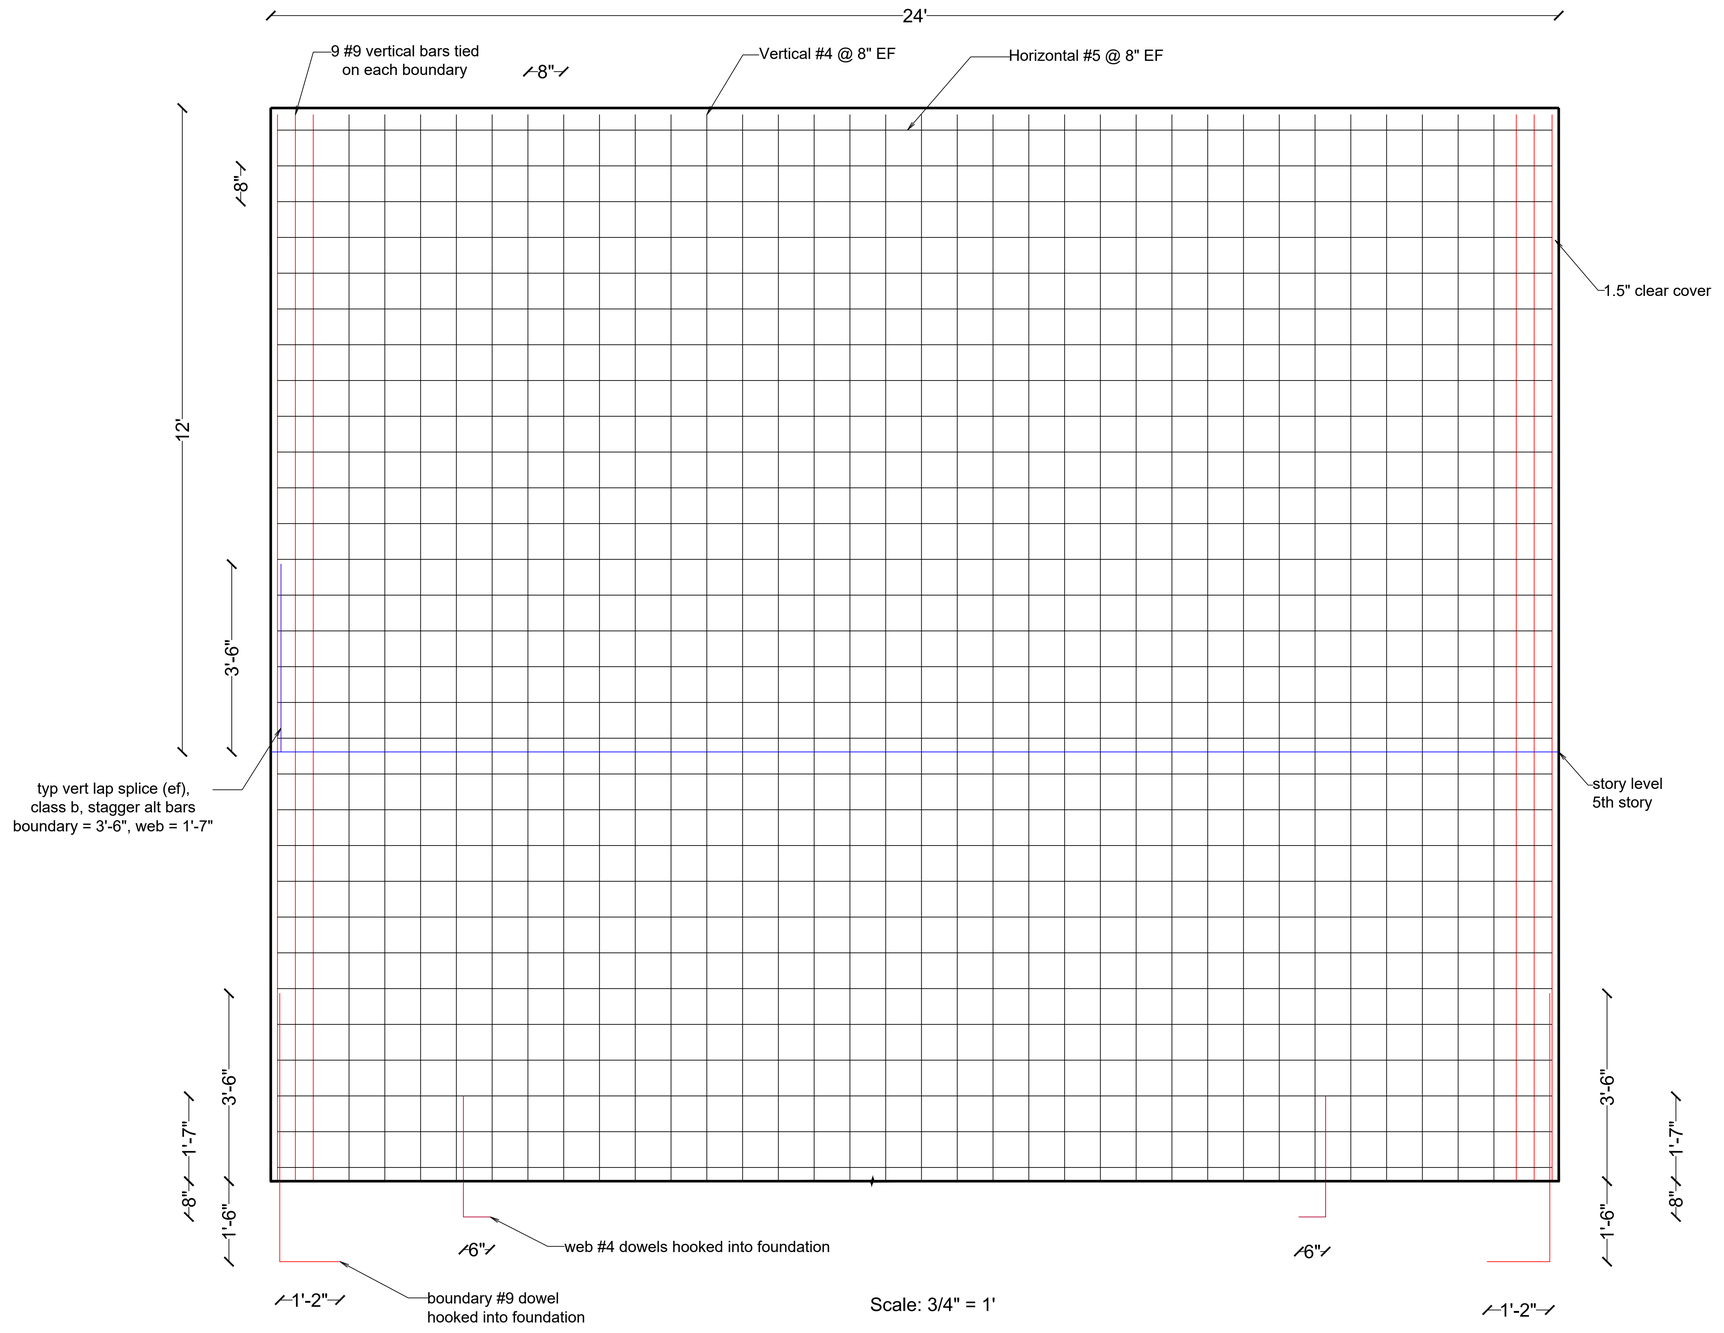

Scale: 3/4" = 1'

Shear Wall horizontal Section

General Notes

Only first story details and base is shown because of symmetry

No.	Revision/Issue	Date

Firm Name and Address

Project Name and Address

5 Story RC Building
San Francisco
California
94105

Project: RC Dual System
Date: 11/2/2026
Scale: As Noted
Sheet: 6